

DETALHES DE PILARES ESPECIAIS
ESCALA 1:25

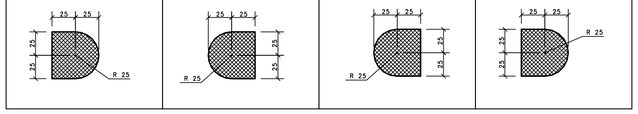

DETALHE TÍPICO DOS BLOCOS JUNTO AOS PONTOS DE CARGA

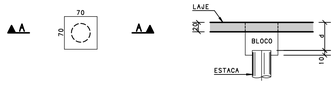

CORRESPONDÊNCIA ENTRE A CLASSE DE AGRESSIVIDADE E A QUALIDADE DO CONCRETO

CLASSE DE AGRESSIVIDADE ADOTADA: III

CONCRETO[a]	TIPO[b,c]	CLASSE DE AGRESSIVIDADE			
		I	II	III	IV
RELAÇÃO ÁGUA/CIMENTO EM MASSA	CA	≤0,65	≤0,60	≤0,55	≤0,45
	CP	≤0,60	≤0,55	≤0,50	≤0,45
CLASSE DE CONCRETO (ABNT NBR 8953)	CA	≥C20	≥C25	≥C30	≥C40
	CP	≥C25	≥C30	≥C35	≥C40
CONSUMO DE CIMENTO POR METRO CÚBICO DE CONCRETO	CA e CP	≥260kg/m³	≥280kg/m³	≥320kg/m³	≥360kg/m³

[a] O CONCRETO EMPREGADO NA EXECUÇÃO DAS ESTRUTURAS DEVE CUMPRIR COM OS REQUISITOS ESTABELECIDOS NA ABNT NBR 12655.
[b] CA CORRESPONDE A COMPONENTES E ELEMENTOS ESTRUTURAIS DE CONCRETO ARMADO
[c] CP CORRESPONDE A COMPONENTES E ELEMENTOS ESTRUTURAIS DE CONCRETO PROTENDIDO


INCÊNDIO - TEMPO REQUERIDO DE RESISTÊNCIA AO FOGO (TRRF)

A)- ALTURA DA EDIFICAÇÃO ACIMA DO ESCAPE (TÉRREO) = 40.19 METROS
B)- TRRF = 120 MINUTOS (DE ACORDO COM A NBR 14432)

OBSERVAÇÕES GERAIS SOBRE ESCORAMENTO

O ESCORAMENTO, O RE-ESCORAMENTO E O CIMBRAMENTO DESTA ESTRUTURA DE CONCRETO DEVERÁ SER OBJETO DE UM PROJETO ADICIONAL ESPECÍFICO, DE RESPONSABILIDADE DO EXECUTANTE DA ESTRUTURA, O QUAL DEVERÁ RESPEITAR TANTO A RESISTÊNCIA COMO A MATURIDADE DOS CONCRETOS, SEM ULTRAPASSAR OS CARREGAMENTOS MÁXIMOS CONSIDERADOS NO PROJETO ESTRUTURAL. ESPECIAL ATENÇÃO DEVERÁ SER DADA PARA NÃO CAUSAR CARREGAMENTOS INADEQUADOS, TAMPOUCO SUBMETER O CONCRETO A AÇÕES NÃO PREVISTAS EM IDADE PRECOCE, O QUE PODERÁ AUMENTAR SIGNIFICATIVAMENTE AS DEFORMAÇÕES LENTAS APRESENTADAS PELA ESTRUTURA.

DETALHE DOS FUROS NAS VIGAS

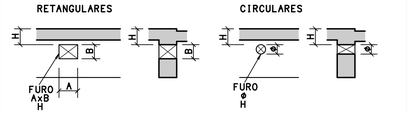

NOTA: ESTÃO MARCADOS NESTA PLANTA OS FUROS EM LAJES E VIGAS QUE NECESSITAM DE REFORÇO ESTRUTURAL. DEMAIS VER PROJETO ESPECÍFICO DE FURAÇÃO.

OBSERVAÇÕES GERAIS SOBRE A EXECUÇÃO DAS ALVENARIAS

A)- EXECUTAR AS ALVENARIAS DE ACORDO COM A NORMA NBR-8545/84 DA ABNT.
B)- AS ALVENARIAS SÓ PODERÃO SER INICIADAS 28 DIAS APÓS A EXECUÇÃO DA ESTRUTURA DE APOIO (VIGAS E LAJES)
C)- O ENCUNHAMENTO DAS ALVENARIAS DEVERÁ SER EXECUTADO NO MÍNIMO APÓS 20 DIAS DA EXECUÇÃO DAS MESMAS.
D)- EM LOCAIS ONDE HOUVER ENCHIMENTO NAS LAJES OU OUTRO ACRÉSCIMO DE CARGA PERMANENTE, ESTE DEVERÁ SER FEITO ANTES DO ENCUNHAMENTO DAS ALVENARIAS RESPEITANDO-SE O PRAZO MÍNIMO DE 20 DIAS.
E)- O REBOCO DAS ALVENARIAS DEVERÃO SER EXECUTADOS APÓS A CURA E RETRAÇÃO DA ARGAMASSA DE ENCUNHAMENTO.

OBSERVAÇÕES GERAIS SOBRE A EXECUÇÃO DA ESTRUTURA

A)- AS COTAS DE IMPLANTAÇÃO, AS DIMENSÕES DAS COTAS E OS NÍVEIS DAS FORMAS DEVERÃO SER VERIFICADAS E ACEITAS PELO RESPONSÁVEL TÉCNICO DA OBRA ANTES DA EXECUÇÃO DAS MESMAS
B)- AS CARGAS INDICADAS EQUIVALEM À SIMPLES SOMA DA CARGA ACIDENTAL COM A CARGA PERMANENTE, PODENDO TER SIDO ADOTADA A REDUÇÃO PREVISTA NA NBR 6120/19
C)- AS QUANTIDADES DE MATERIAIS CONSTANTES EM CADA PRANCHA SÃO INDICATIVAS DEVENDO SER VERIFICADAS PELO RESPONSÁVEL TÉCNICO DA OBRA TANTO PARA FINS DE ORÇAMENTO COMO PARA COMPRA DE MATERIAL.
D)- AS DOBRAS E OS DIÂMETROS DE CURVATURA DOS GANCHOS DEVERÃO ATENDER O PRESCRITO NA NBR-6118/2023.
E)- QUALQUER MODIFICAÇÃO OU DÚVIDA DEVERÁ SER IMEDIATAMENTE COMUNICADA POR ESCRITO AO PROJETISTA ESTRUTURAL.

SOBRECARGAS CONSIDERADAS NESTE PAVIMENTO

1 - PAREDES DE:
- A)- ALVENARIA DE TIJOLOS MACIÇOS = 1700 kgf/m³
- B)- ALVENARIA DE TIJOLOS FURADOS = 1300 kgf/m³
- C)- GESSO ACARTONADO (DRY WALL) = 50 kgf/m²

2 - SOBRECARGAS PERMANENTES
- A)- PISO E CONTRAPISO = 150 kgf/m²
- B)- REBOCO DE TETO = 25 kgf/m²

3 - SOBRECARGA DE UTILIZAÇÃO
- A)- QUANDO NÃO INDICADO AS CARGAS DE UTILIZAÇÃO DEVERÃO RESPEITAR O PRESCRITO NA NORMA NBR 6120/2019

PROPRIEDADES DO CONCRETO

VALORES ESTIMADOS DE MÓDULO DE ELASTICIDADE EM FUNÇÃO DA RESISTÊNCIA CARACTERÍSTICA À COMPRESSÃO DO CONCRETO, CONSIDERANDO O USO DO GRANITO COMO AGREGADO GRAÚDO

CLASSE DE RESISTÊNCIA	C25	C30	C35	C40	C45	C50
Eci (GPa)	28	31	33	35	38	40
Ecs (GPa)	24	27	29	32	34	37

VUP(VIDA ÚTIL DE PROJETO)=50 ANOS, CONFORME TABELA 7 DA NBR 15575-1/13

COBRIMENTOS DAS ARMADURAS

VIGAS = 3.5 cm
LAJES = 3.0 cm (ARMADURA NEGATIVA)
LAJES = 3.0 cm (ARMADURA POSITIVA)
PILARES = 3.5 cm

CONVENÇÕES

- PILAR QUE NASCE NESTE PAVIMENTO
- PILAR QUE MORRE NESTE PAVIMENTO
- PILAR QUE PASSA PELO PAVIMENTO
- INDICA QUE O EIXO DA VIGA É O MESMO DO PILAR
- INDICA QUE A VIGA ESTÁ NA FACE DO PILAR

VOLUMES DE CONCRETO

VIGAS	-----	m³
LAJES	-----	m³
PILARES	-----	m³
RESERVATÓRIOS	-----	m³
TOTAL	-----	m³

NIVEIS (m.)

8,88 | 9,18


FAIXA PARA CONCRETAGEM EM 2a ETAPA

VOLUMES DE CONCRETO - VER PLANTA 7-202

DET. TÍPICO P/ SEÇÃO DAS VIGAS DIRETAS, EXCETO JUNTO A LAJES EM DESNÍVEL OU SE FOREM INVERTIDAS.



PAVIMENTO TÉRREO PARTE 1 DA ESTRUTURA, VER PLANTA 7-202

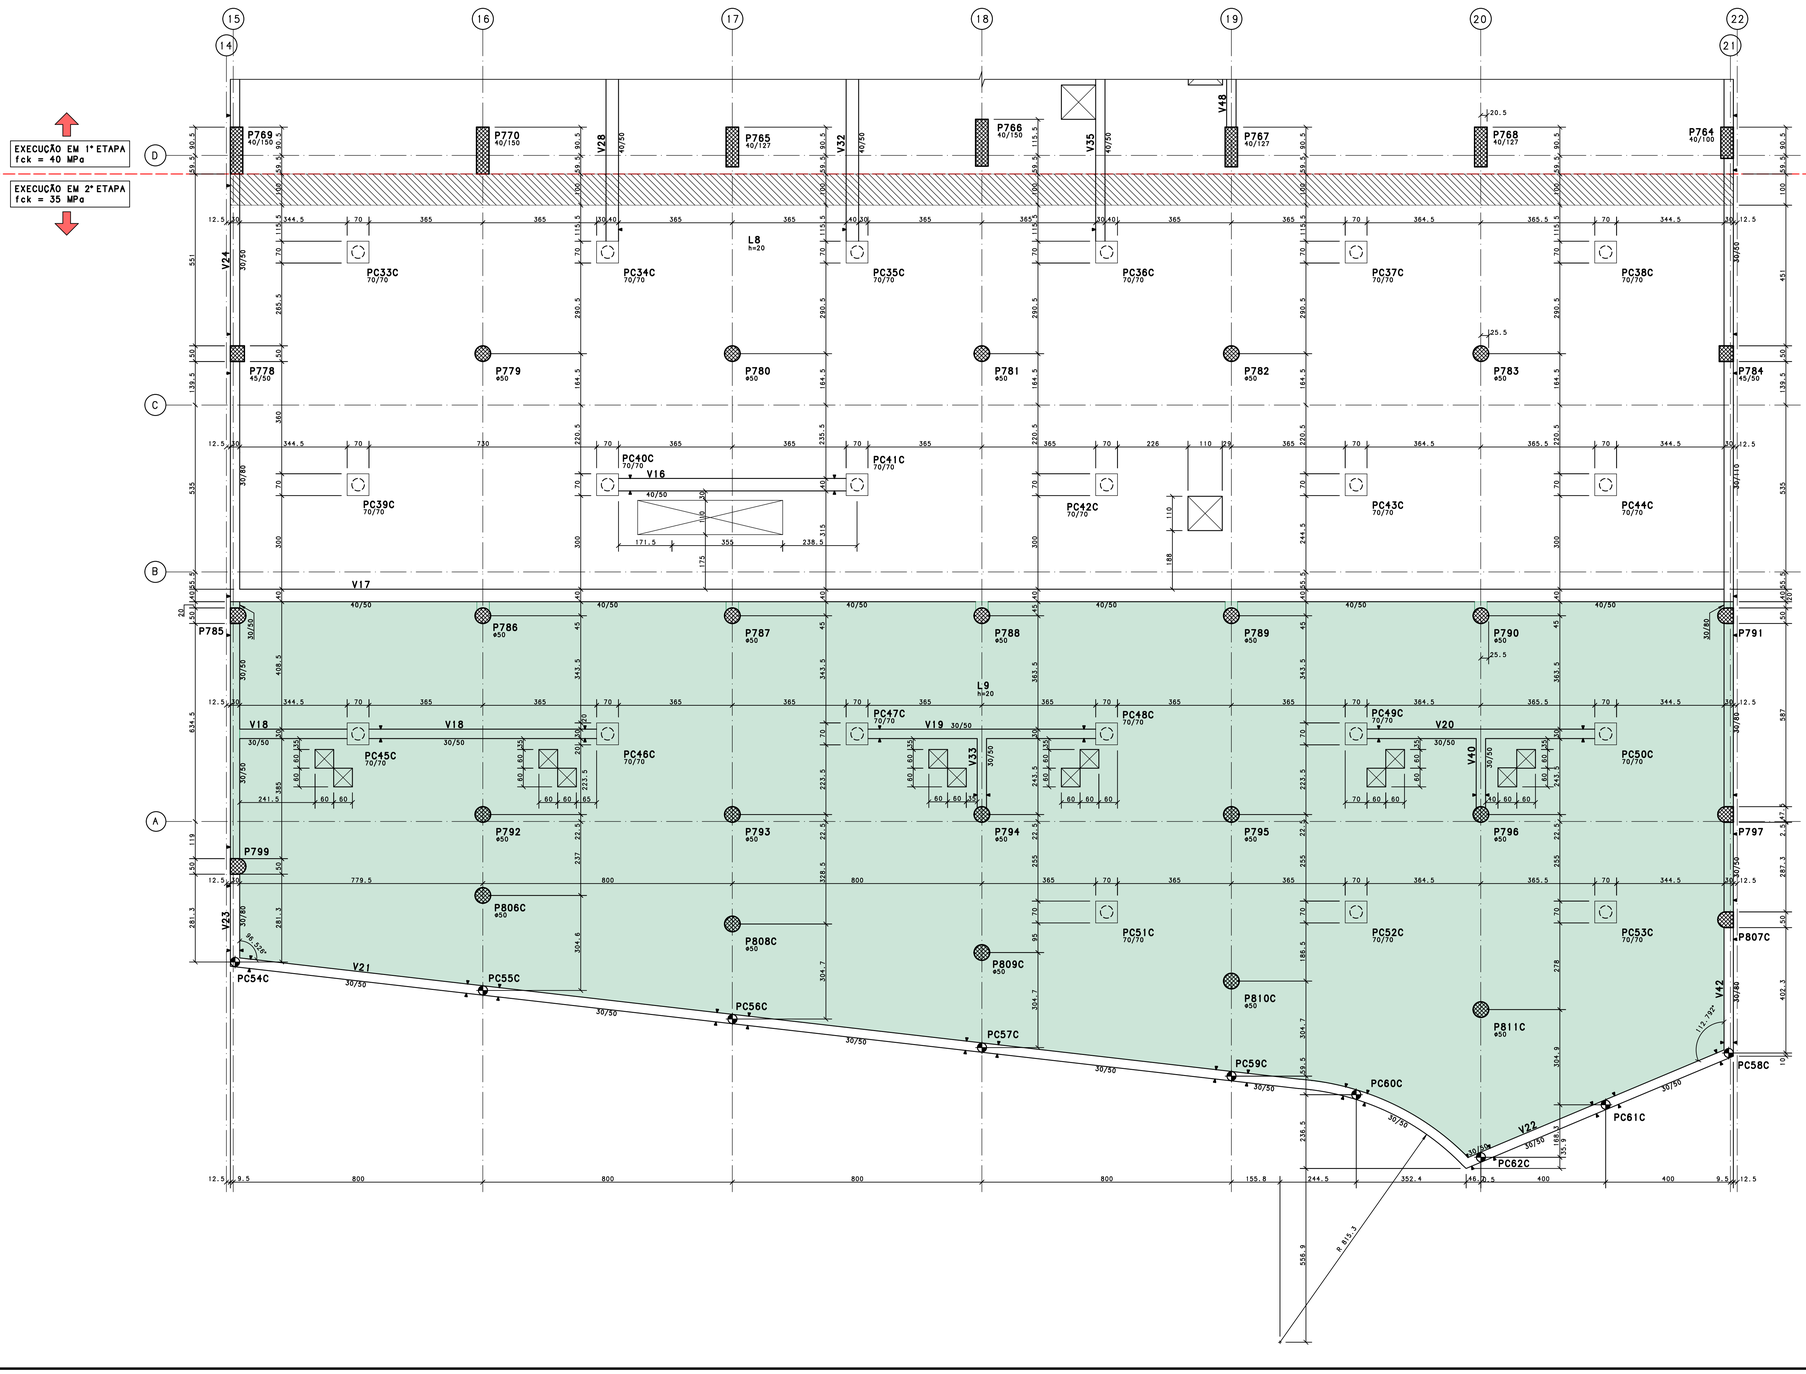

01	20/07/26	MODIF. GERAIS	FLP
00	11/05/26	EMISSÃO INICIAL	MVJ
REV.	DATA	ALTERAÇÃO	VISTO

PROCALK ESTRUTURAS

RESP. TÉCNICOS
Eng. Edemir C. Simonetto
CREA-RS 63038
Eng. Carlos R.M. Morais
CREA-RS 74695

Rua João Abbott, 473/401
Porto Alegre - CEP 90460-150
T (51)3013.3200
procalk@procalk.com.br
www.procalk.com.br

Obra: WERT PORTO BELO RESIDENCES
PORTO BELO - SC
Assunto: FORMAS - MULTI 02 - SETOR 7
PAVIMENTO TÉRREO - PARTE 2
Conteúdo

Cliente: WERT
Número: 24-1454
Desenho: 7-214/1
Identificação: WPBR-EST-EX-7214-PLN-MU2-S07-TE-R01
Desenho: MARCUS
Escala: 1:75
Tok: 40 MPa
Data: 11/05/2026

PARA PLOTAGEM UTILIZAR EXCLUSIVAMENTE O ARQUIVO PLT DO PDF.

Direitos Autorais Reservados Lei N 9174/66

110/75

PROCALK ESTRUTURAS PL PDF20071341.PLT 20/07/2026 10:28:13