V1

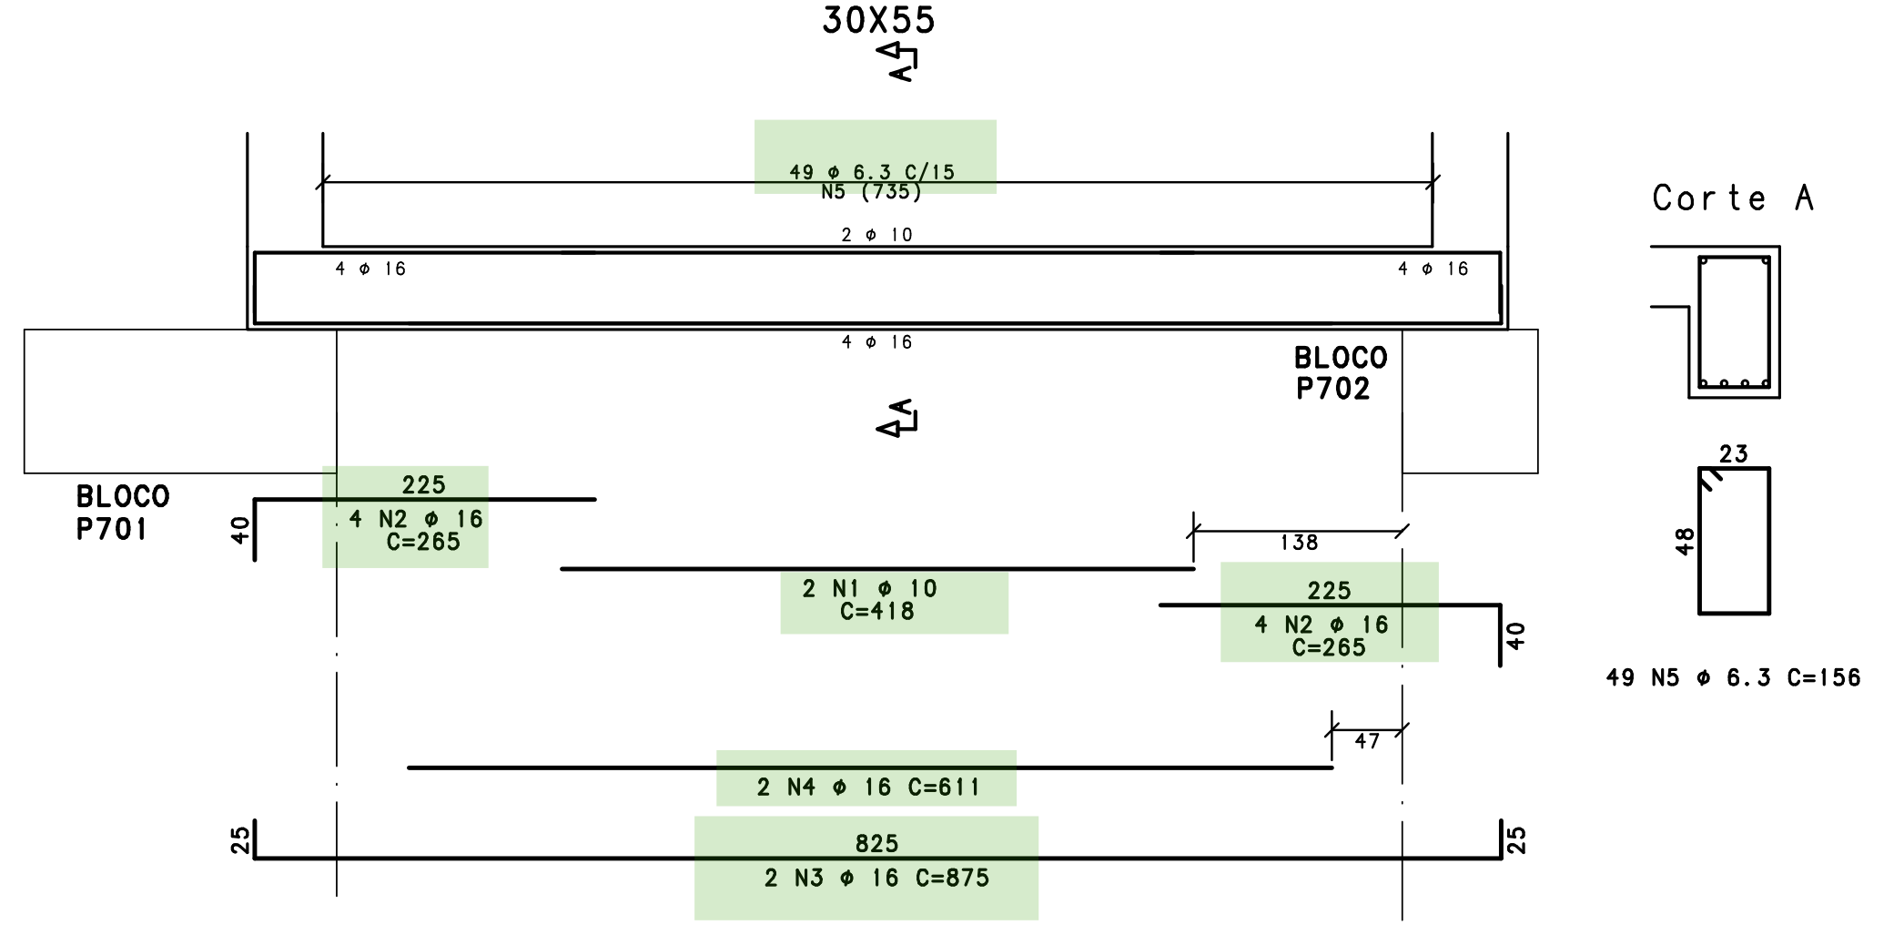

V2

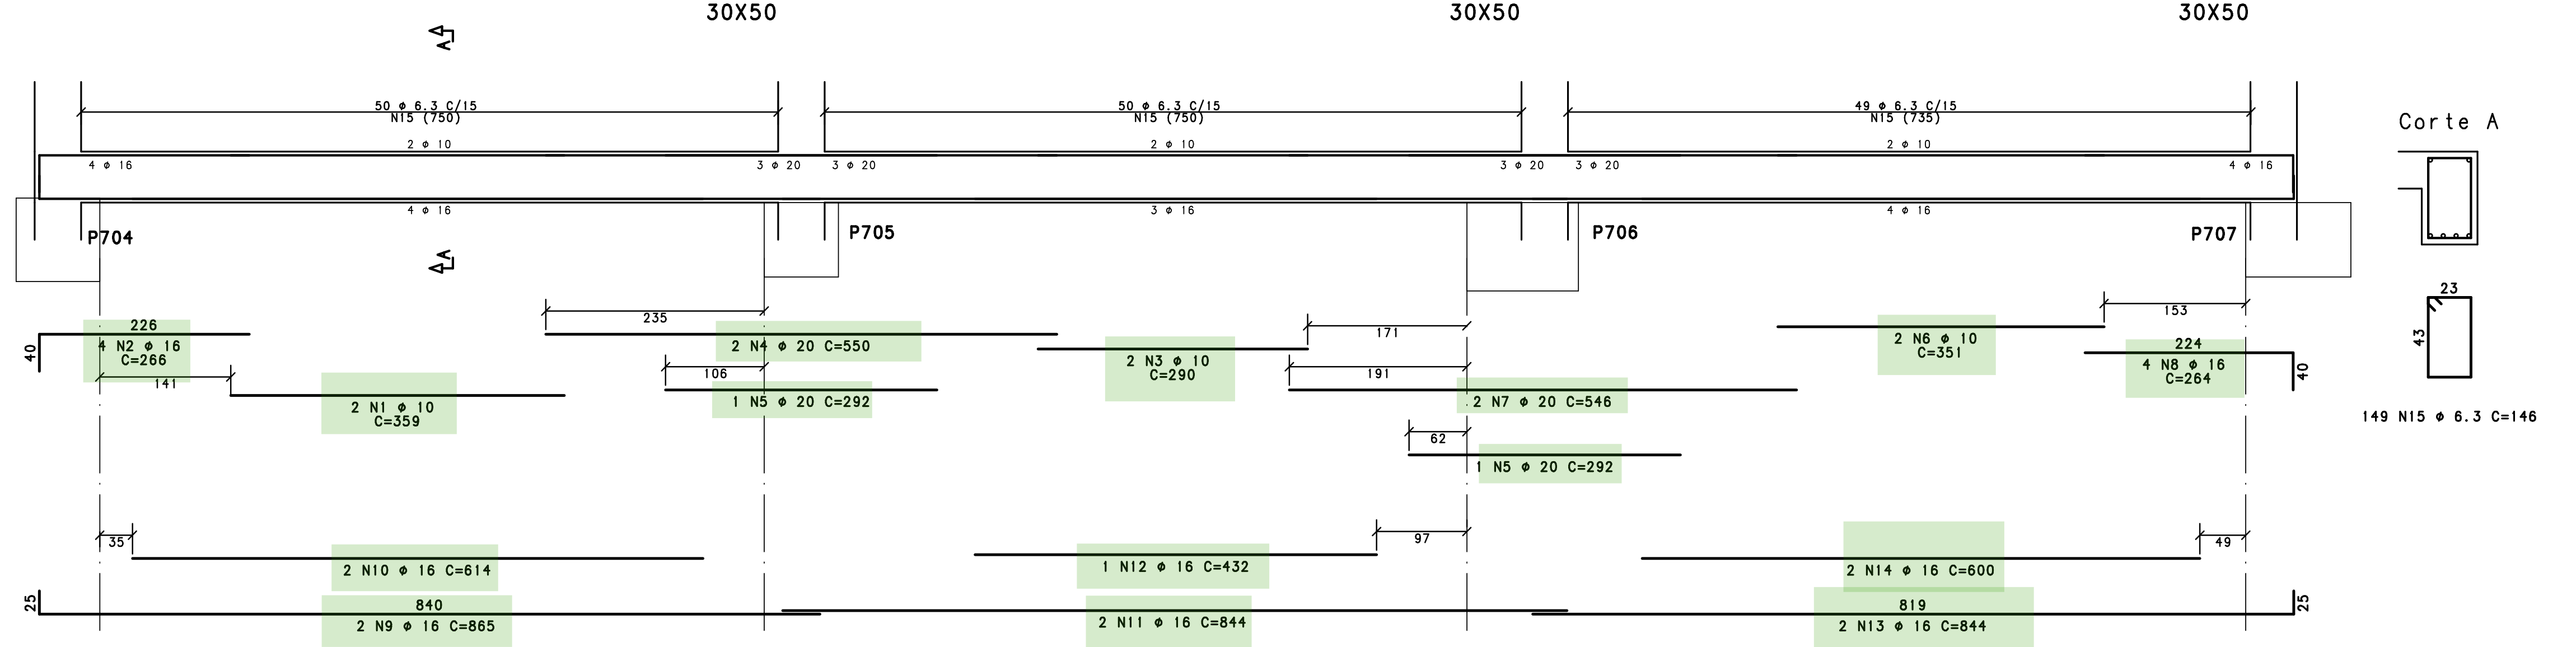

V3

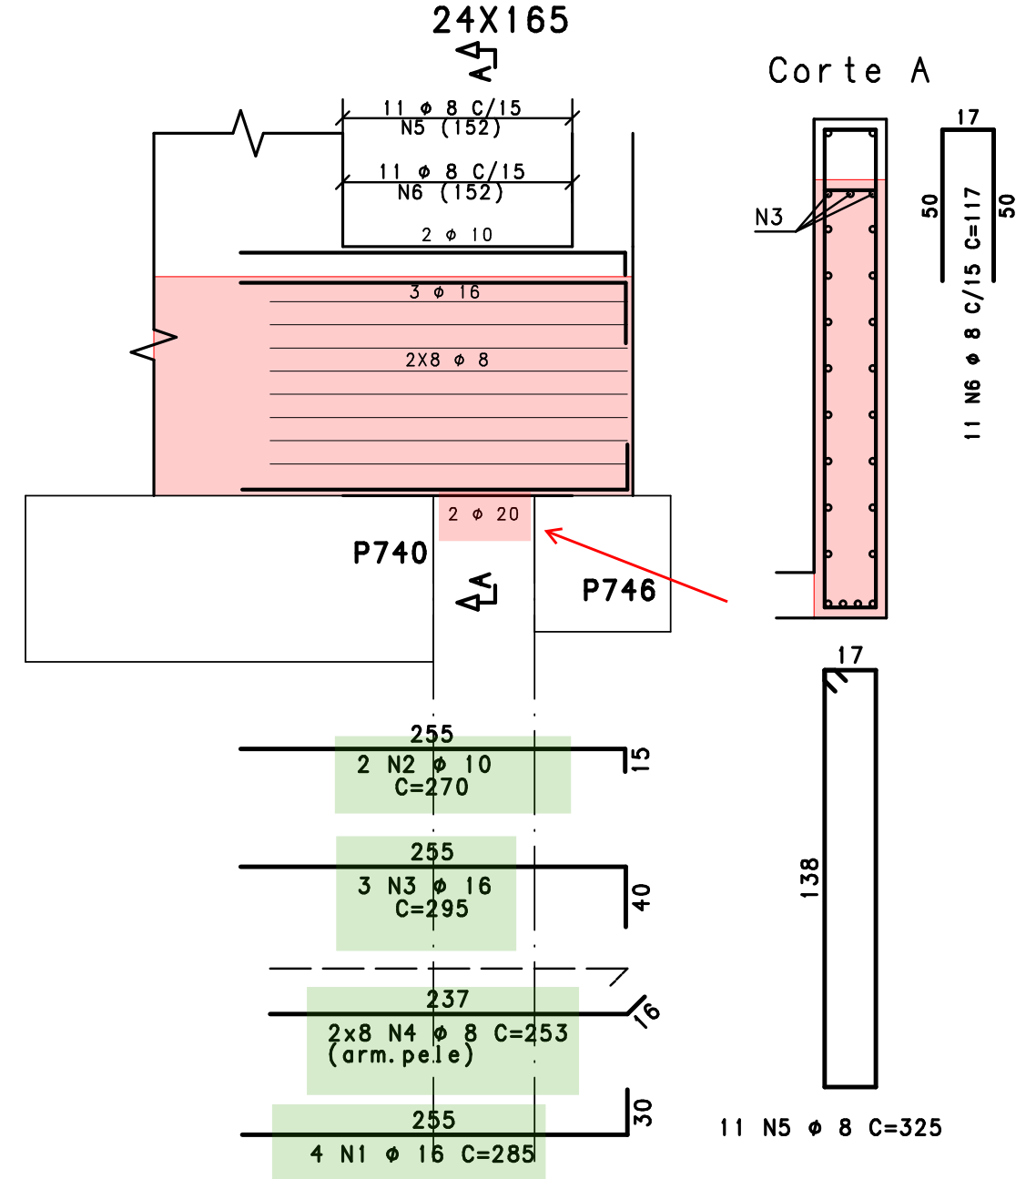

V4

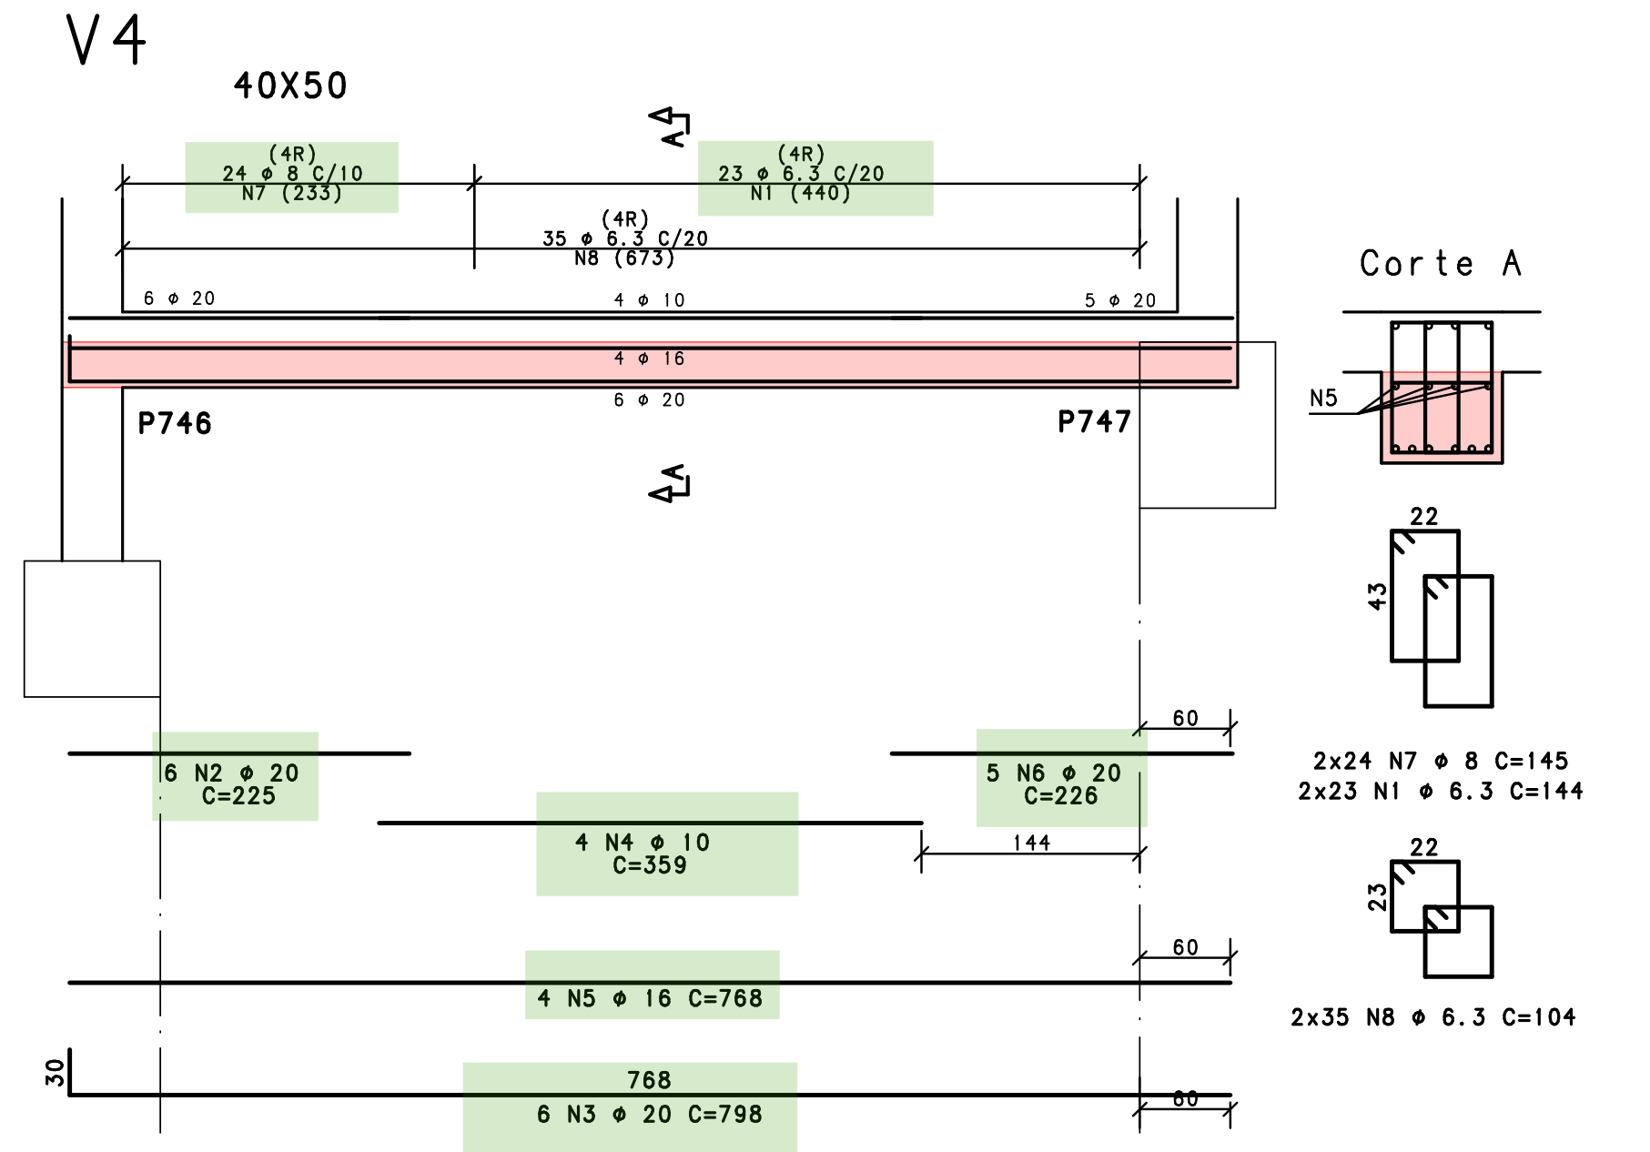

V5

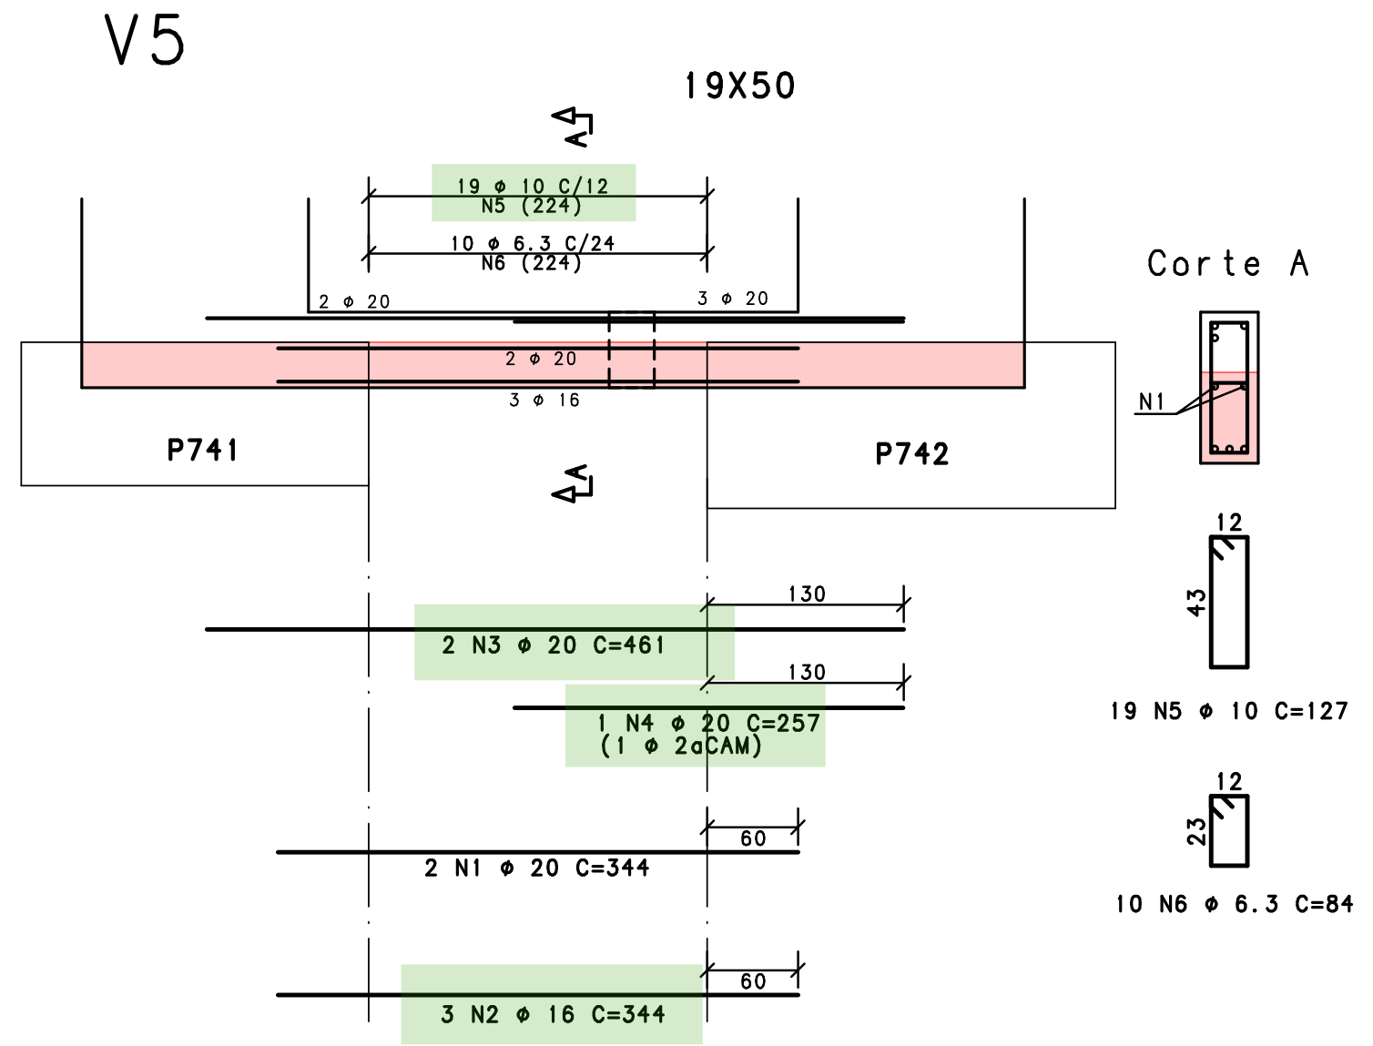

V6

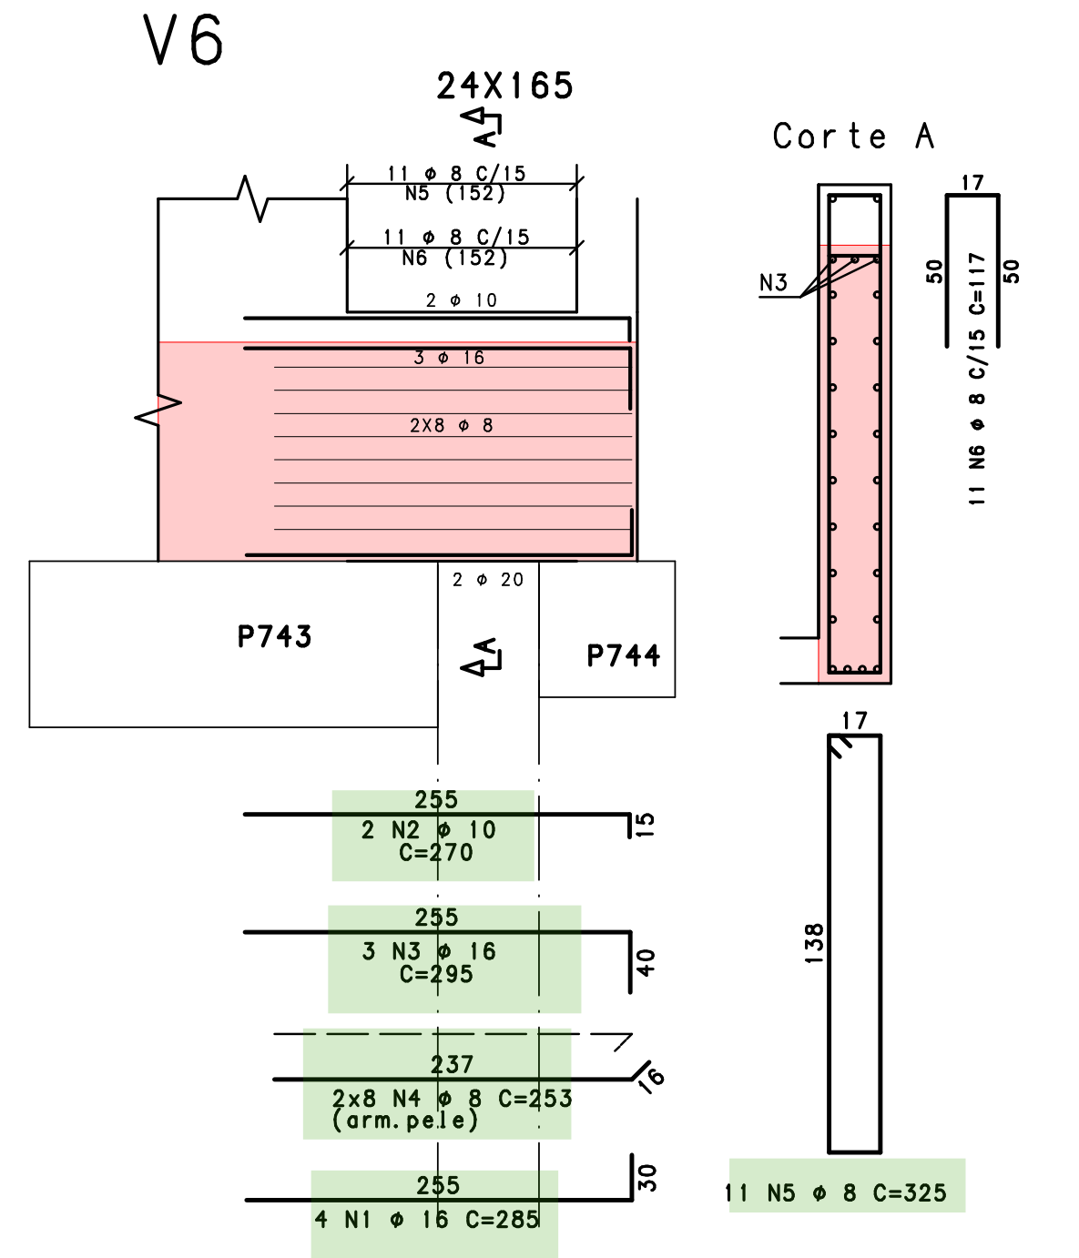

V7=V8=V9=V10

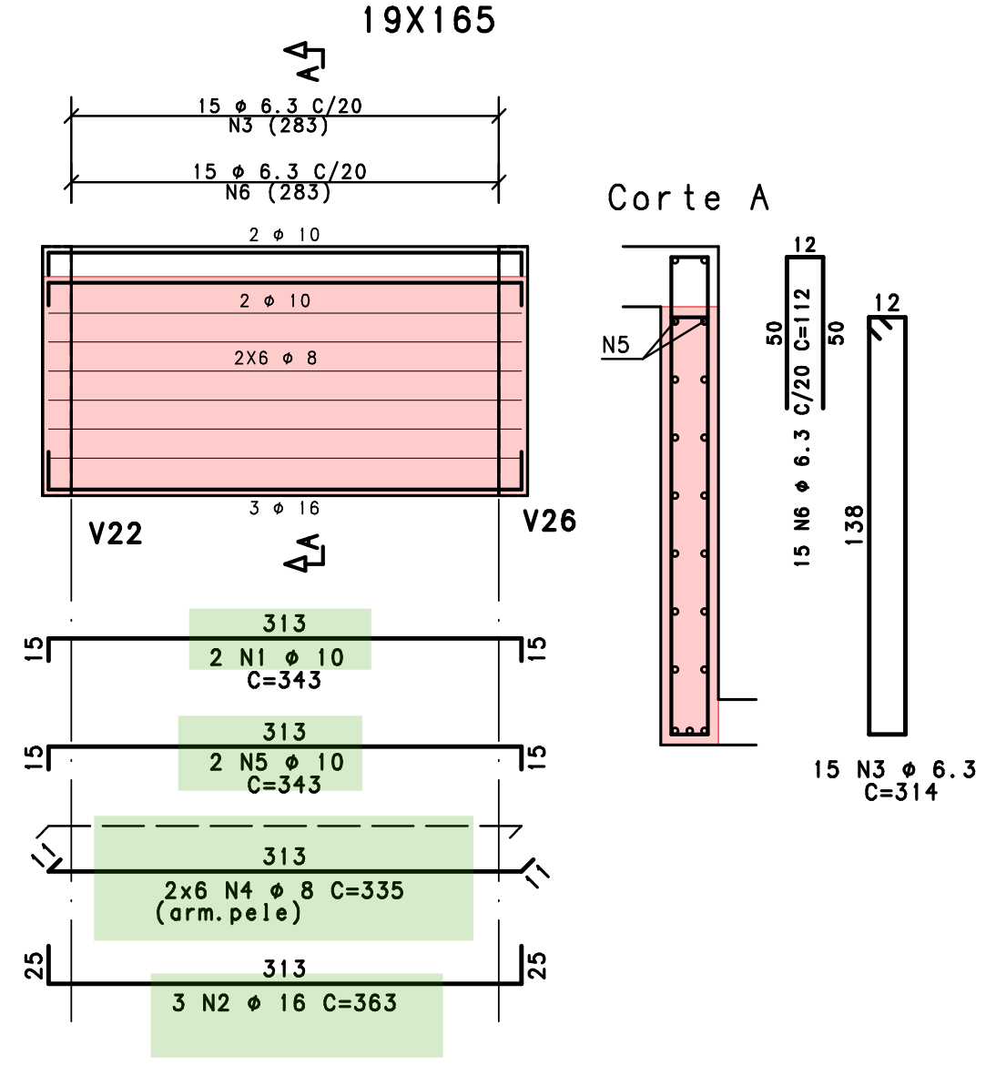

V11

* AS DOBRAS DAS ARMADURAS, EM PLANTA, ACOMPANHAM A INCLINAÇÃO DA FORMA JUNTO AO P754

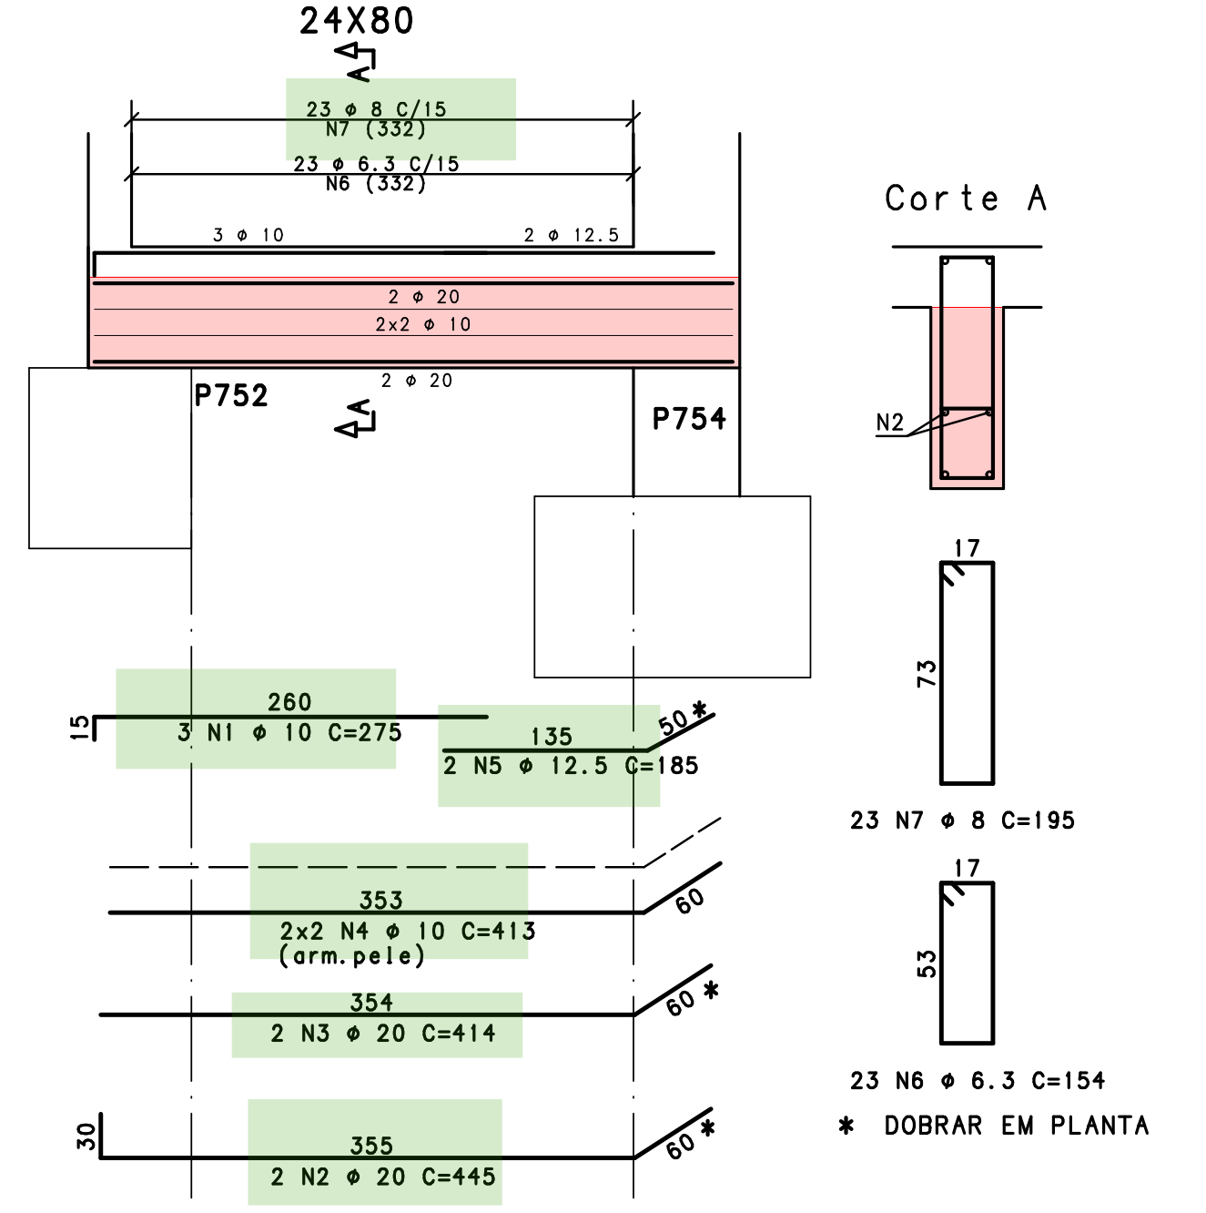

V12=V13

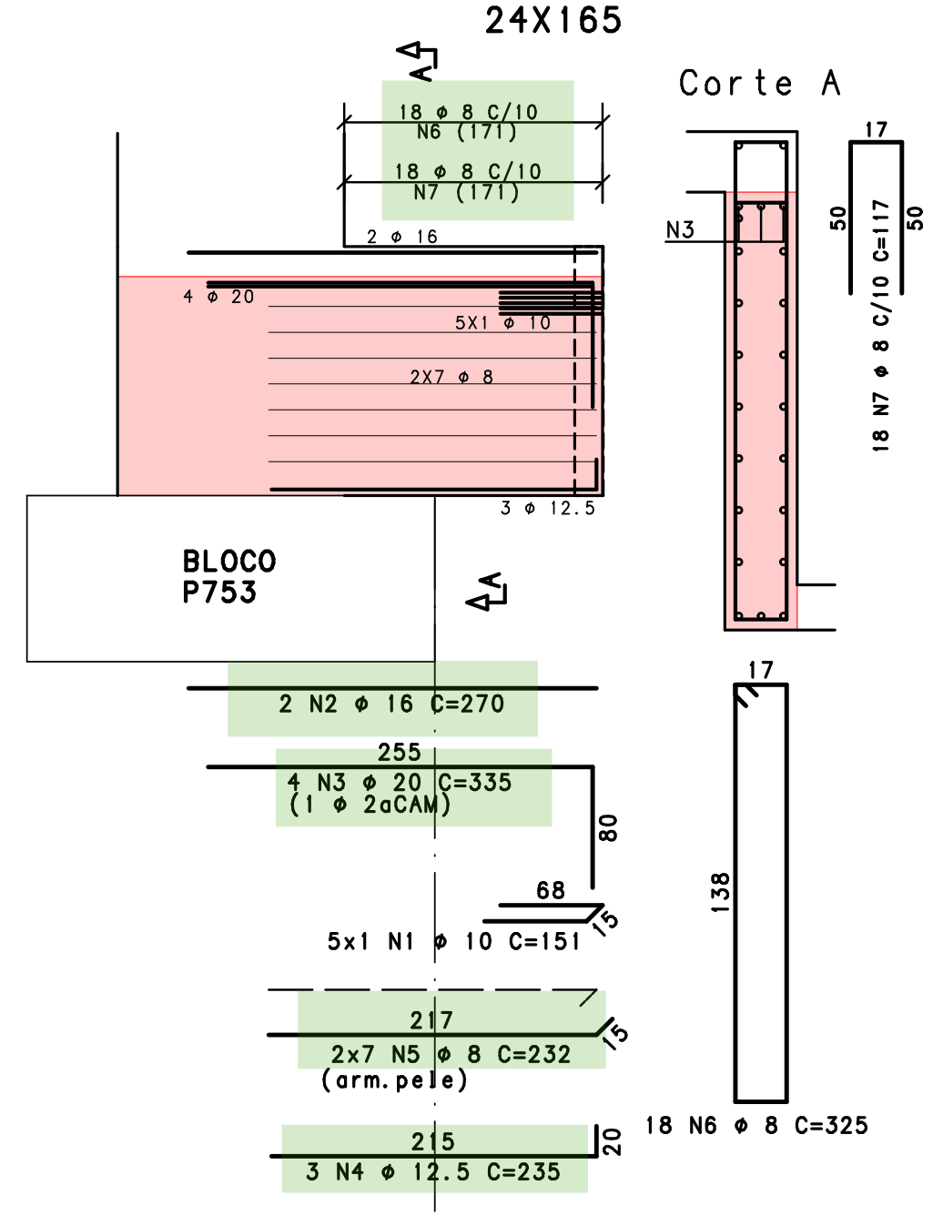

V14

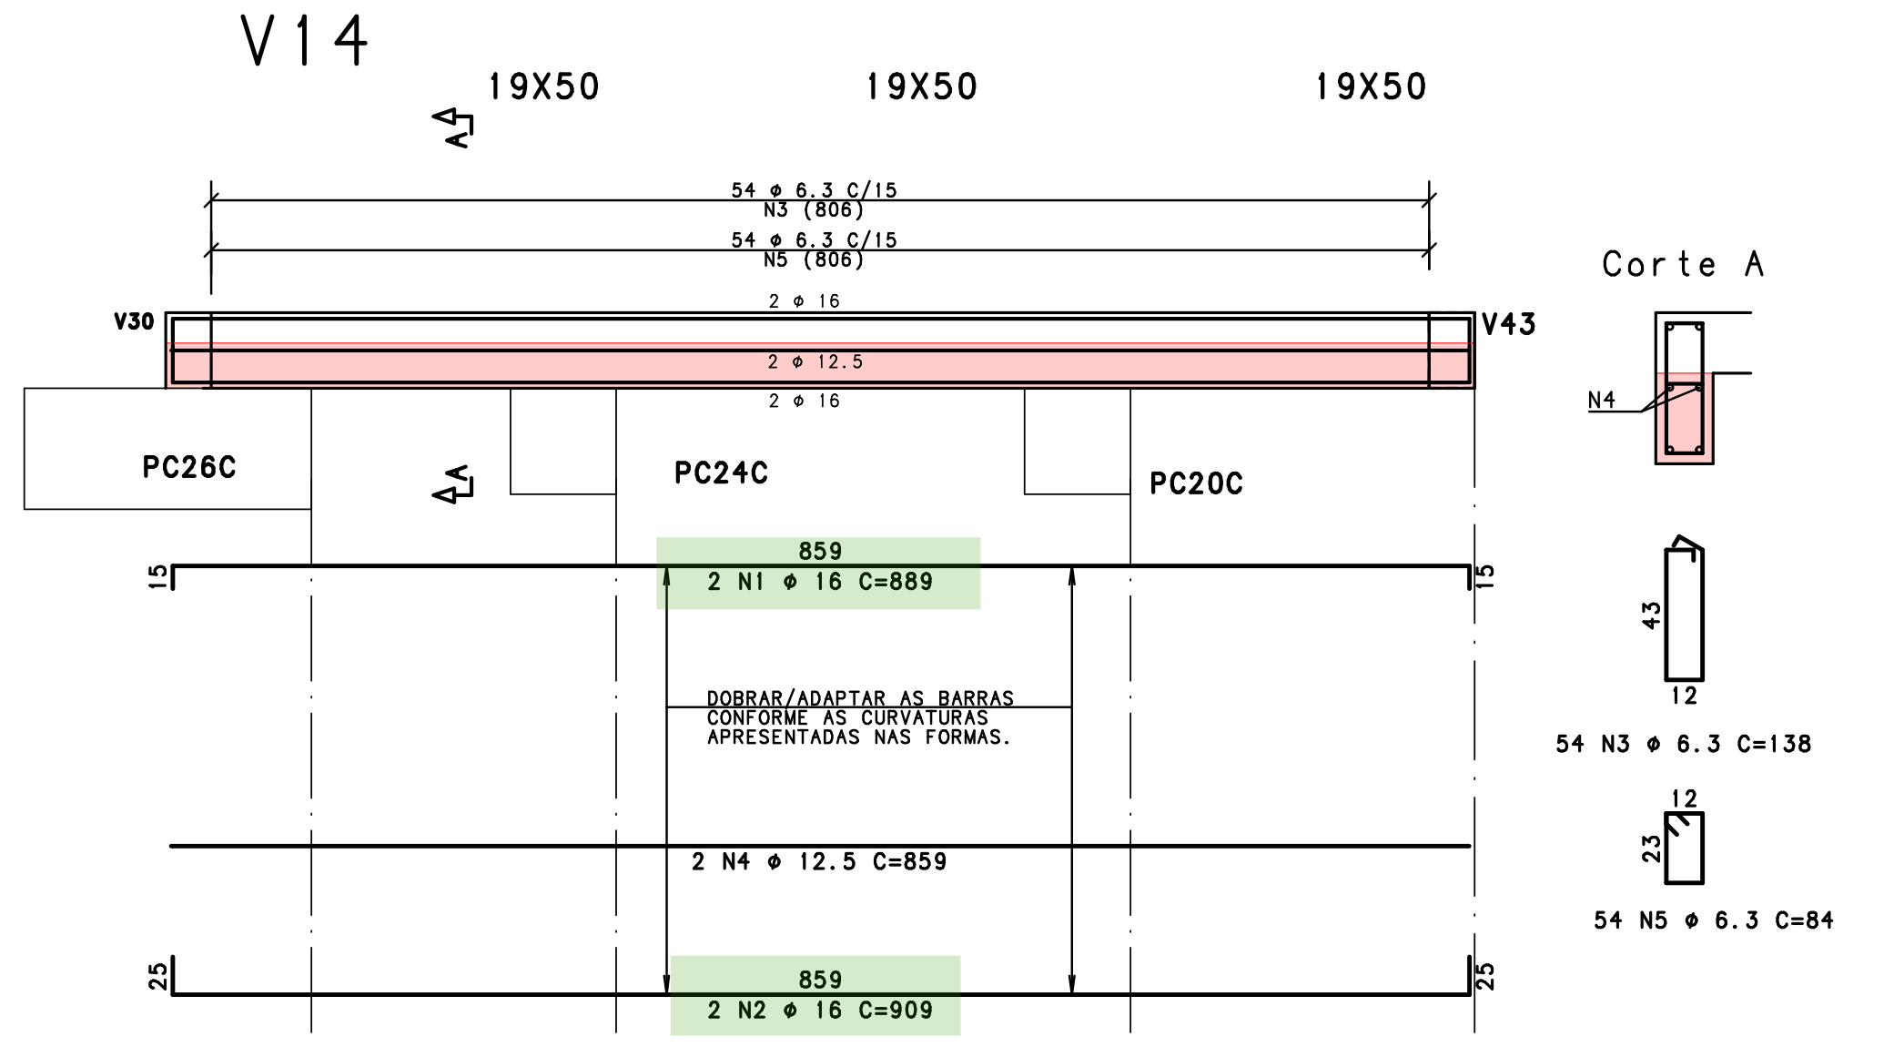

V15

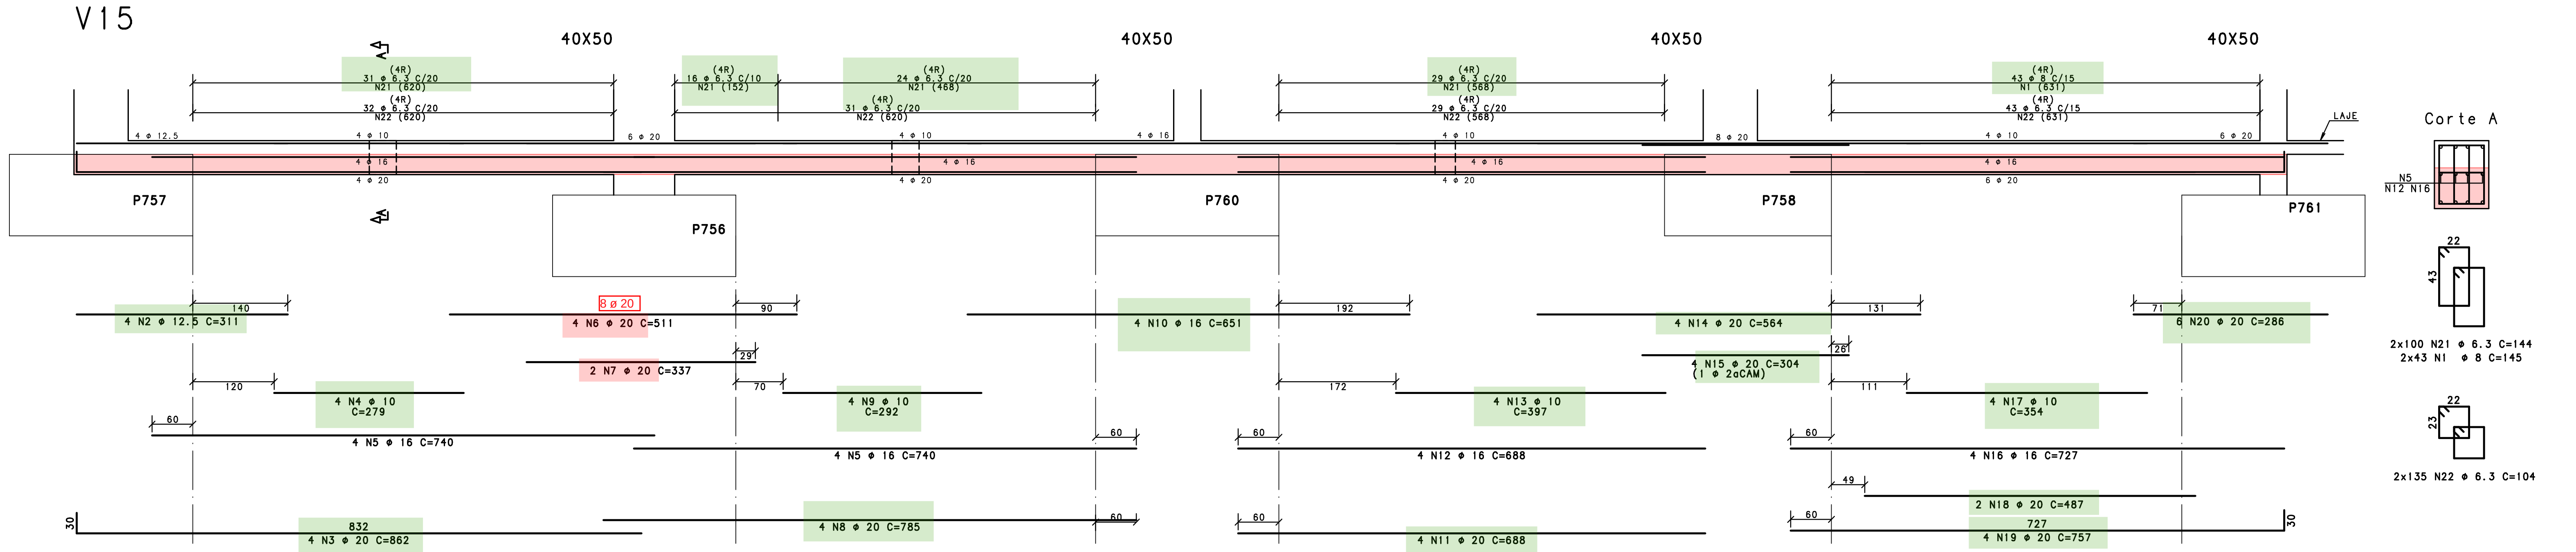

V16

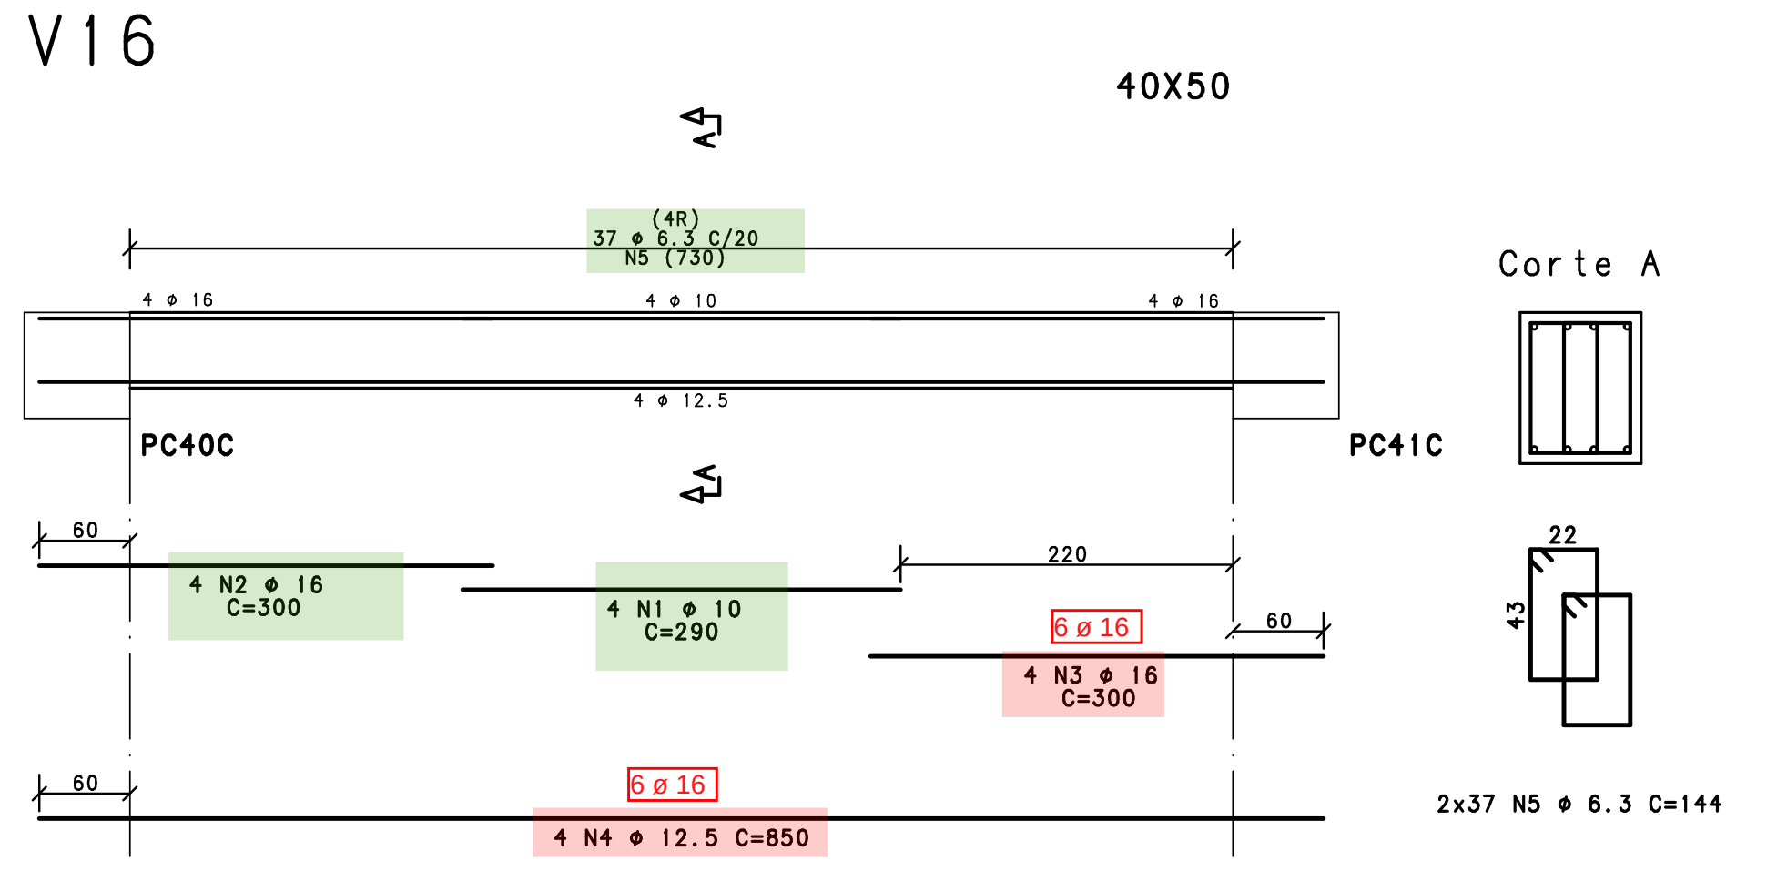

V18

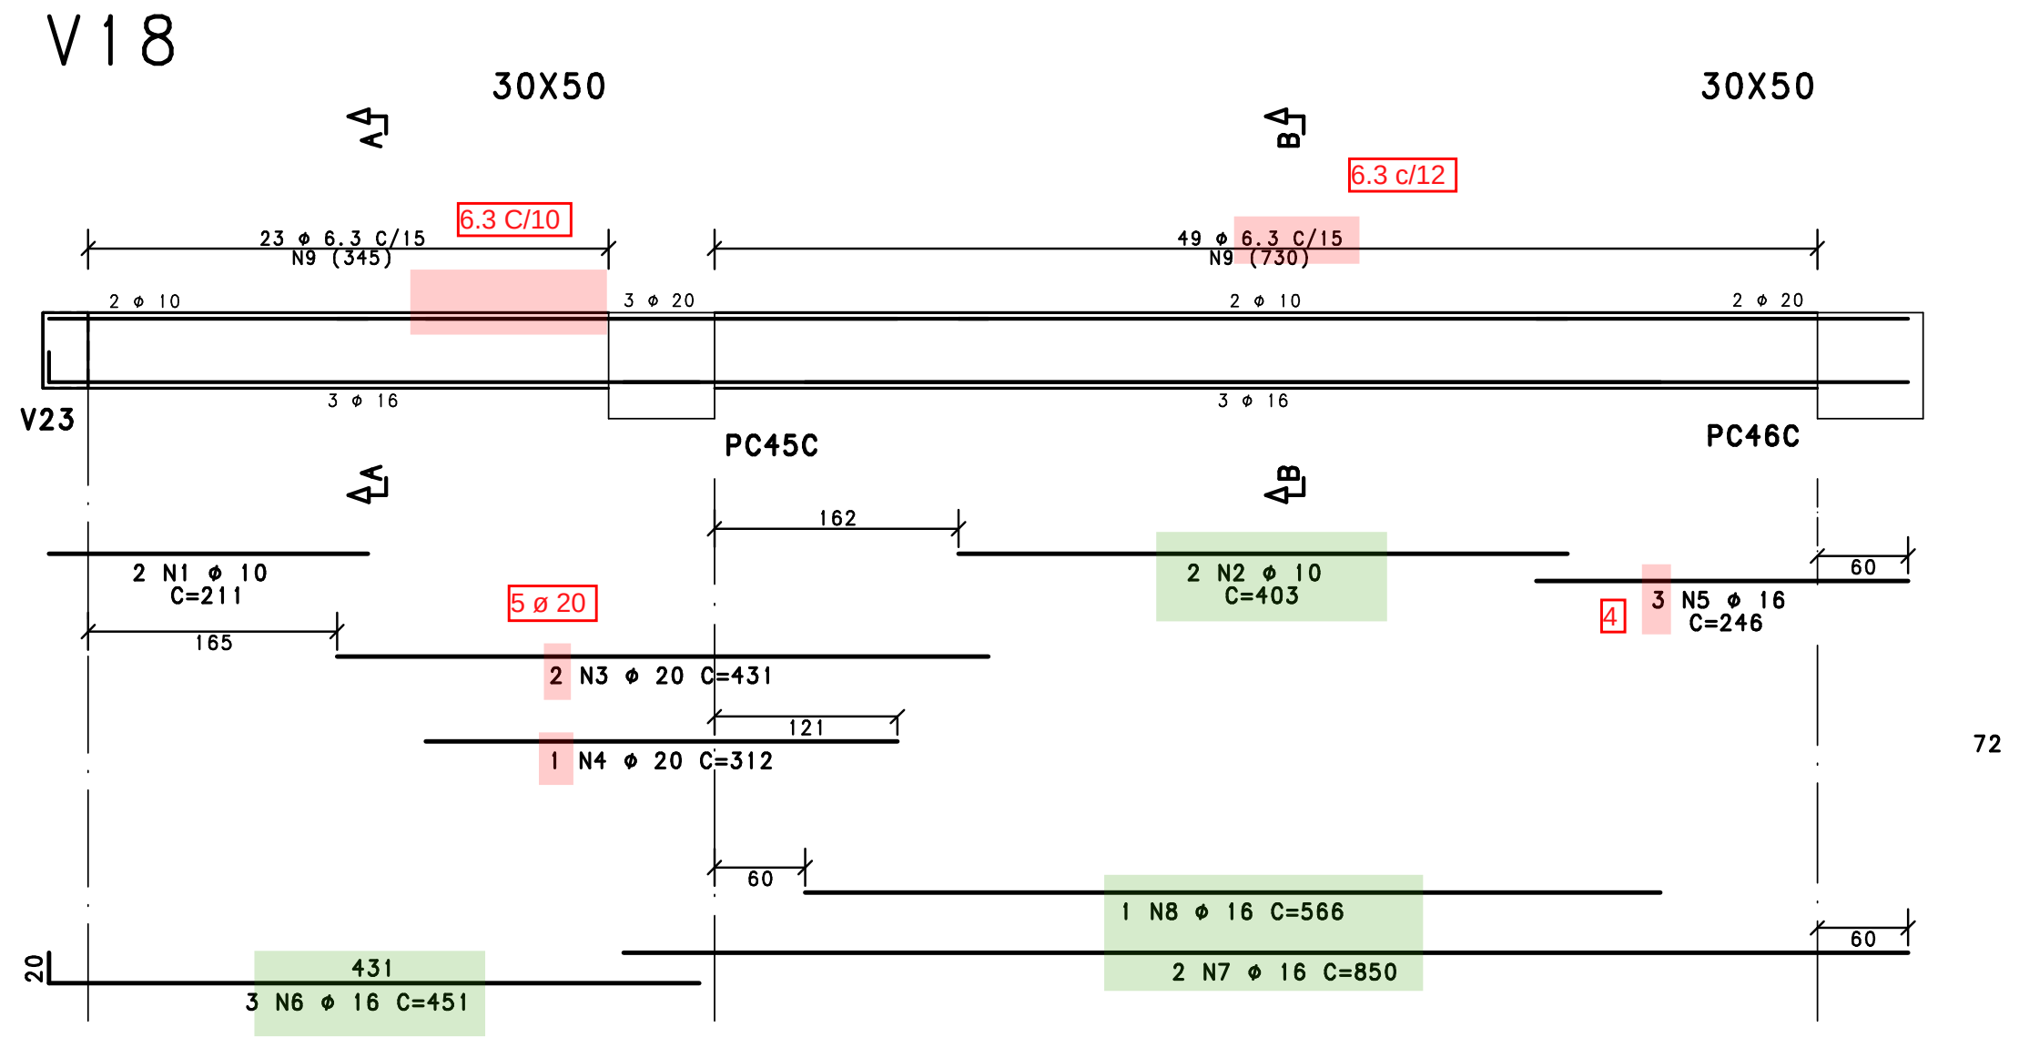

V19=V20

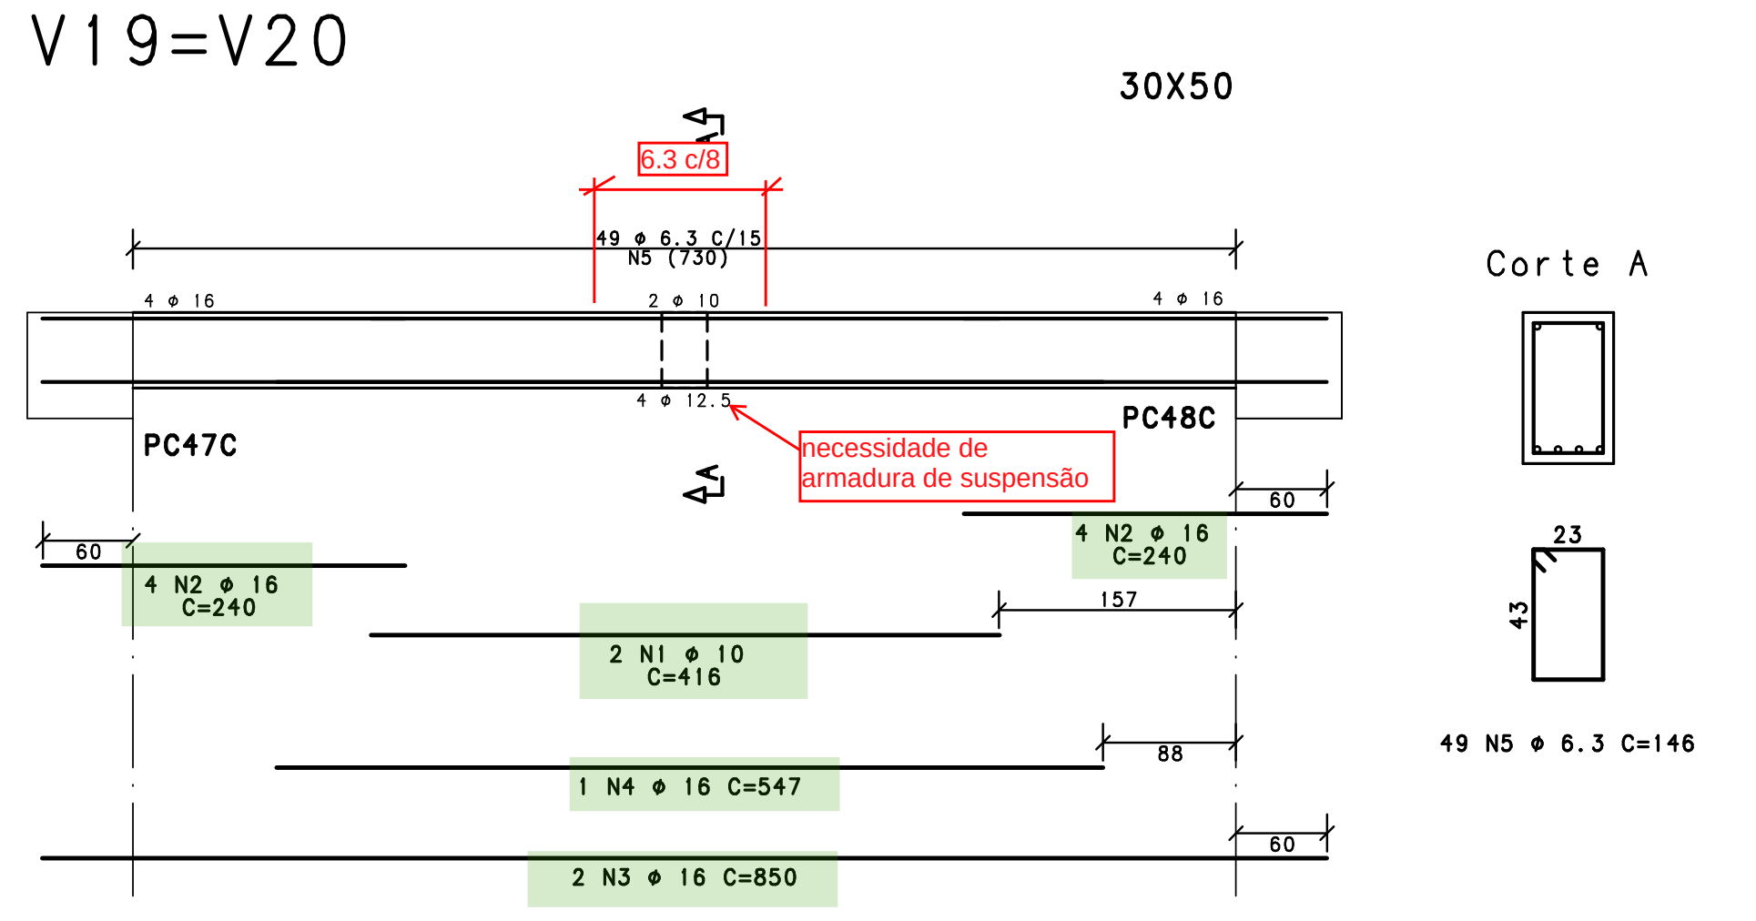

V17

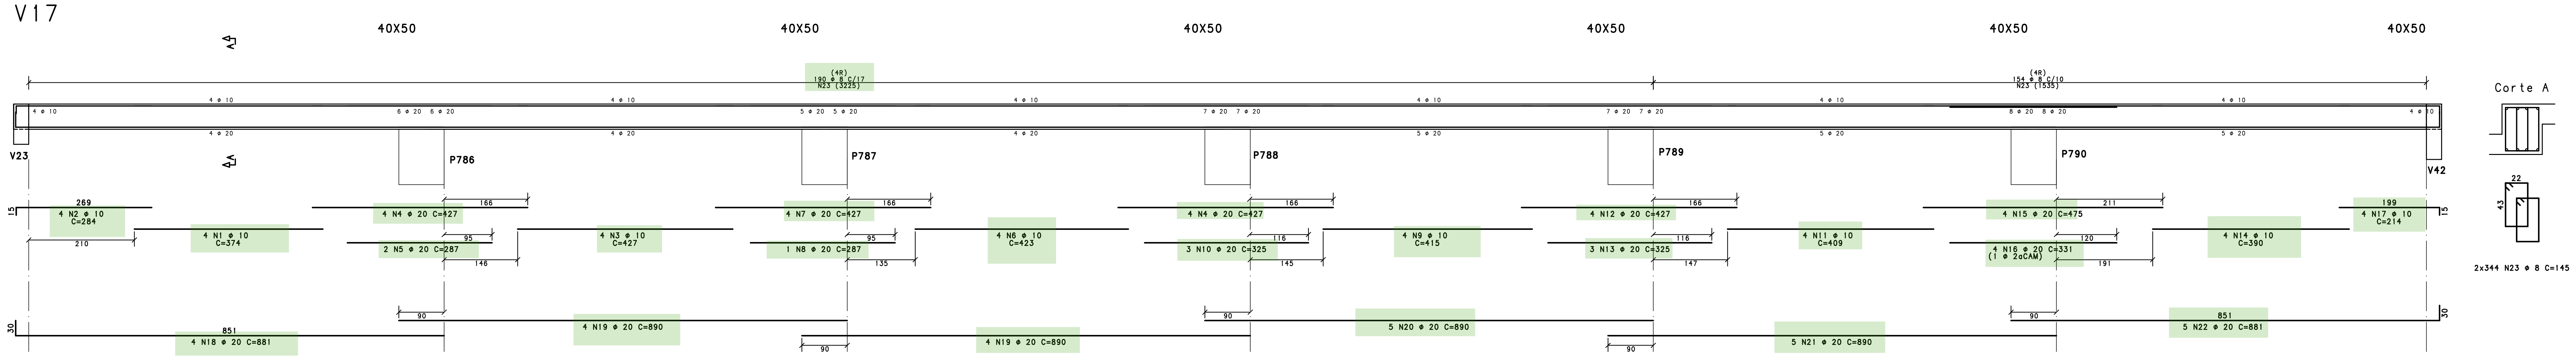

	AÇO	POS	QUANT	BIT (mm)	COMPRIMENTO	
					UNIT (cm)	TOTAL (cm)
V1						
	50A	1	2	10	418	836
	50A	2	8	16	265	2120
	50A	3	2	16	875	1750
	50A	4	2	16	611	1222
	50A	5	49	6.3	156	7644
V2						
	50A	1	2	10	359	718
	50A	2	4	16	266	1064
	50A	3	2	10	290	580
	50A	4	2	20	550	1100
	50A	5	2	20	292	584
	50A	6	2	10	351	702
	50A	7	2	20	546	1092
	50A	8	4	16	264	1056
	50A	9	2	16	865	1730
	50A	10	2	16	614	1228
	50A	11	2	16	844	1688
	50A	12	1	16	432	432
	50A	13	2	16	844	1688
	50A	14	2	16	600	1200
	50A	15	149	6.3	146	21754
V3						
	50A	1	4	16	285	1140
	50A	2	2	10	270	540
	50A	3	3	16	295	885
	50A	4	16	8	253	4048
	50A	5	11	8	325	3575
	50A	6	11	8	117	1287
V4						
	50A	1	46	6.3	144	6624
	50A	2	6	20	225	1350
	50A	3	6	20	798	4788
	50A	4	4	10	359	1436
	50A	5	4	16	768	3072
	50A	6	5	20	226	1130
	50A	7	48	8	145	6960
	50A	8	70	6.3	104	7280
V5						
	50A	1	2	20	344	688
	50A	2	3	16	344	1032
	50A	3	2	20	461	922
	50A	4	1	20	257	257
	50A	5	19	10	127	2413
	50A	6	10	6.3	84	840
V6						
	50A	1	4	16	285	1140
	50A	2	2	10	270	540
	50A	3	3	16	295	885
	50A	4	16	8	253	4048
	50A	5	11	8	325	3575
	50A	6	11	8	117	1287
V7=V8=V9=V10 (X4)						
	50A	1	8	10	343	2744
	50A	2	12	16	363	4356
	50A	3	60	6.3	314	18840
	50A	4	48	8	335	16080
	50A	5	8	10	343	2744
	50A	6	60	6.3	112	6720
V11						
	50A	1	3	10	275	825
	50A	2	2	20	445	890
	50A	3	2	20	414	828
	50A	4	4	10	413	1652
	50A	5	2	12.5	185	370
	50A	6	23	6.3	154	3542
	50A	7	23	8	195	4485

	AÇO	POS	QUANT	BIT (mm)	COMPRIMENTO	
					UNIT (cm)	TOTAL (cm)
V12=V13 (X2)						
	50A	1	10	10	151	1510
	50A	2	4	16	270	1080
	50A	3	8	20	335	2680
	50A	4	6	12.5	235	1410
	50A	5	28	8	232	6496
	50A	6	36	8	325	11700
	50A	7	36	8	117	4212
V14						
	50A	1	2	16	889	1778
	50A	2	2	16	909	1818
	50A	3	54	6.3	138	7452
	50A	4	2	12.5	859	1718
	50A	5	54	6.3	84	4536
V15						
	50A	1	86	8	145	12470
	50A	2	4	12.5	311	1244
	50A	3	4	20	862	3448
	50A	4	4	10	279	1116
	50A	5	8	16	740	5920
	50A	6	4	20	511	2044
	50A	7	2	20	337	674
	50A	8	4	20	785	3140
	50A	9	4	10	292	1168
	50A	10	4	16	651	2604
	50A	11	4	20	688	2752
	50A	12	4	16	688	2752
	50A	13	4	10	397	1588
	50A	14	4	20	564	2256
	50A	15	4	20	304	1216
	50A	16	4	16	727	2908
	50A	17	4	10	354	1416
	50A	18	2	20	487	974
	50A	19	4	20	757	3028
	50A	20	6	20	286	1716
	50A	21	200	6.3	144	28800
	50A	22	270	6.3	104	28080
V16						
	50A	1	4	10	290	1160
	50A	2	4	16	300	1200
	50A	3	4	16	300	1200
	50A	4	4	12.5	850	3400
	50A	5	74	6.3	144	10656
V17						
	50A	1	4	10	374	1496
	50A	2	4	10	284	1136
	50A	3	4	10	427	1708
	50A	4	8	20	427	3416
	50A	5	2	20	287	574
	50A	6	4	10	423	1692
	50A	7	4	20	427	1708
	50A	8	1	20	287	287
	50A	9	4	10	415	1660
	50A	10	3	20	325	975
	50A	11	4	10	409	1636
	50A	12	4	20	427	1708
	50A	13	3	20	325	975
	50A	14	4	10	390	1560
	50A	15	4	20	475	1900
	50A	16	4	20	331	1324
	50A	17	4	10	214	856
	50A	18	4	20	881	3524
	50A	19	8	20	890	7120
	50A	20	5	20	890	4450
	50A	21	5	20	890	4450
	50A	22	5	20	881	4405
	50A	23	688	8	145	99760
V18						
	50A	1	2	10	211	422
	50A	2	2	10	403	806
	50A	3	2	20	431	862
	50A	4	1	20	312	312
	50A	5	3	16	246	738
	50A	6	3	16	451	1353
	50A	7	2	16	850	1700
	50A	8	1	16	566	566
	50A	9	72	6.3	146	10512
V19=V20 (X2)						
	50A	1	4	10	416	1664
	50A	2	16	16	240	3840
	50A	3	4	16	850	3400
	50A	4	2	16	547	1094
	50A	5	98	6.3	146	14308

RESUMO TOTAL AÇO CA 50-60			
AÇO	BIT (mm)	COMPR (m)	PESO (kg)
50A	6.3	1776	435
50A	8	1800	711
50A	10	383	236
50A	12.5	81	78
50A	16	616	973
50A	20	755	1863
Peso Total		50A =	4297 kgf

LEGENDA

🟥 REGIÃO A SER CONCRETADA EM 1° ETAPA

REV.	DATA	ALTERAÇÃO	VISTO
00	17/07/26	EMISSÃO INICIAL	FLP

PROCALK
ESTRUTURAS

RESP. TÉCNICOS
Eng. Edemir C. Simonato
CREA-RS 63038
Eng. Carlos R.M. Morais
CREA-RS 74695

Rua João Abbott, 473/401
Porto Alegre - CEP 90460-150
F. (51)3013.3200
procalk@procalk.com.br
www.procalk.com.br

Obra: WERT PORTO BELO RESIDENCES
PORTO BELO - SC
Assunto: VIGAS - MULTI 02 - SETOR 7
TÉRREO
Conteúdo: V1 / V2 / V3 / V4 / V5 / V6 / V7=V8=V9=V10
V11 / V12=V13 / V14 / V15 / V16 / V17 / V18
V19=V20
Cliente: WERT
Número: 24-1454
Desenho: 7-401/0
Identificação: WPBR-EST-EX-7401-PLN-MU2-S07-TE-R00
Desenho: FILIPE
Escala: 1:50
fck: 40/35 MPa
Data: 17/07/2026

PARA PLOTAGEM UTILIZAR EXCLUSIVAMENTE O ARQUIVO PLT OU PDF.

Direitos Autorais Reservados Lei N 5194/66

130/89

PROCALK ESTRUTURAS PL 4-01-00.PLT 17/07/2026 14:52:29