

V21

30X50 | 30X50 | 30X50 | 30X50 | 30X50 | 30X50

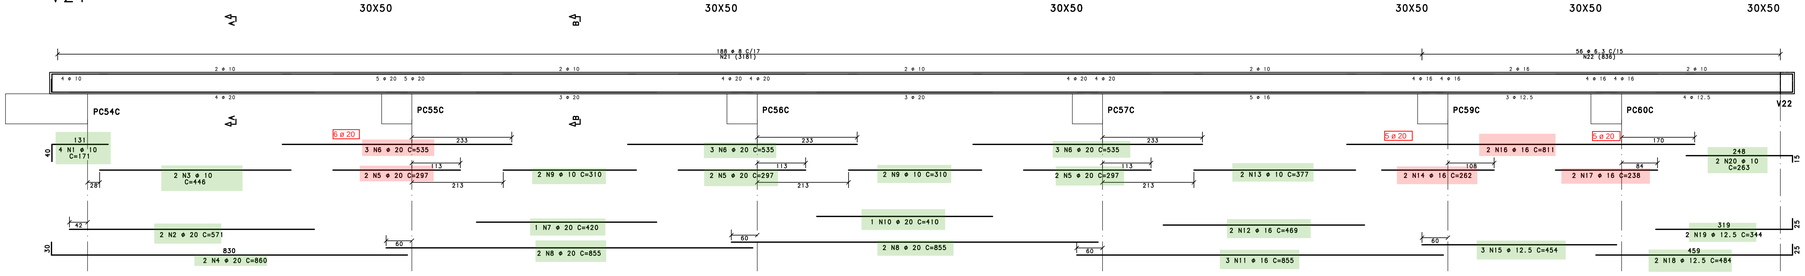


Corte A

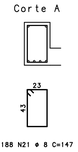

188 N21 ø 8 C=147


Corte B

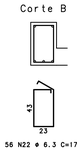

56 N22 ø 6.3 C=171


V23

30X80 | 30X50

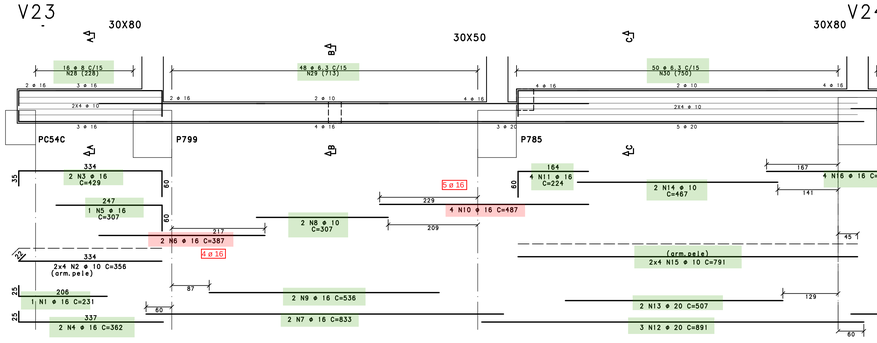


V24

30X80 | 30X50 | 30X50 | 30X50

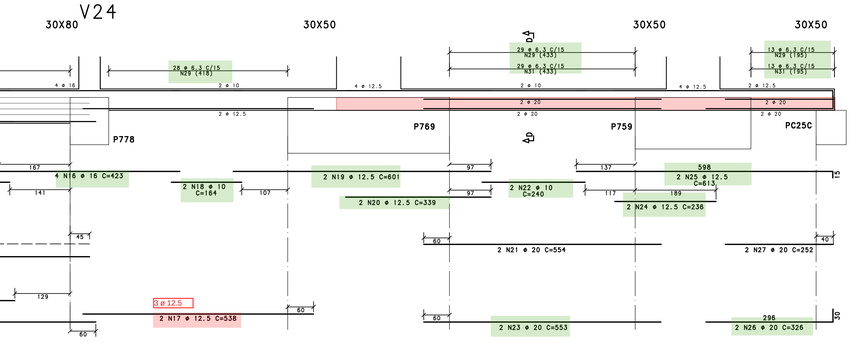

Corte A

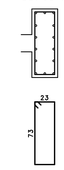


16 N28 ø 8 C=207

Corte B




48 N29 ø 6.3 C=146

Corte C

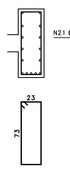

50 N30 ø 6.3 C=206

Corte D

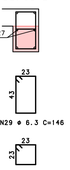

70 N29 ø 6.3 C=146

42 N31 ø 6.3 C=106

	ACO	POS	QUANT	BIT (mm)	COMPRIMENTO UNIT (cm)	COMPRIMENTO TOTAL (cm)
V21						
	50A	1	4	10	171	684
	50A	2	2	20	571	1142
	50A	3	2	10	446	892
	50A	4	2	20	860	1720
	50A	5	6	20	297	1782
	50A	6	9	20	535	4815
	50A	7	1	20	420	420
	50A	8	4	20	855	3420
	50A	9	4	10	310	1240
	50A	10	1	20	410	410
	50A	11	3	16	855	2565
	50A	12	2	16	469	938
	50A	13	2	10	377	754
	50A	14	2	16	262	524
	50A	15	3	12.5	454	1362
	50A	16	2	16	811	1622
	50A	17	2	16	238	476
	50A	18	2	12.5	484	968
	50A	19	2	12.5	344	688
	50A	20	2	10	263	526
	50A	21	188	8	147	27636
	50A	22	56	6.3	171	9576
V22						
	50A	1	2	12.5	353	706
	50A	2	2	12.5	403	806
	50A	3	2	12.5	536	1072
	50A	4	2	20	392	784
	50A	5	1	20	272	272
	50A	6	2	20	484	968
	50A	7	2	16	424	848
	50A	8	2	16	334	668
	50A	9	63	6.3	146	9198
V23=V24						
	50A	1	1	16	231	231
	50A	2	8	10	356	2848
	50A	3	2	16	429	858
	50A	4	2	16	362	724
	50A	5	1	16	307	307
	50A	6	2	16	387	774
	50A	7	2	16	833	1666
	50A	8	2	10	307	614
	50A	9	2	16	536	1072
	50A	10	4	16	487	1948
	50A	11	4	16	224	896
	50A	12	2	20	891	2673
	50A	13	2	20	507	1014
	50A	14	2	20	467	934
	50A	15	8	10	791	6328
	50A	16	4	16	423	1692
	50A	17	2	12.5	538	1076
	50A	18	2	10	184	368
	50A	19	2	12.5	601	1202
	50A	20	2	12.5	339	678
	50A	21	2	20	554	1108
	50A	22	2	20	240	480
	50A	23	2	20	553	1106
	50A	24	2	12.5	236	472
	50A	25	2	12.5	613	1226
	50A	26	2	20	326	652
	50A	27	2	20	252	504
	50A	28	16	8	207	3312
	50A	29	118	6.3	146	17228
	50A	30	50	6.3	206	10300
	50A	31	42	6.3	106	4452


	ACO	POS	QUANT	BIT (mm)	COMPRIMENTO UNIT (cm)	COMPRIMENTO TOTAL (cm)
V25						
	50A	1	2	16	197	394
	50A	2	2	16	288	576
	50A	3	2	20	822	1644
	50A	4	2	20	822	2466
	50A	5	2	10	357	714
	50A	6	2	10	278	556
	50A	7	2	16	642	1284
	50A	8	2	20	465	930
	50A	9	2	20	462	924
	50A	10	2	16	778	1556
	50A	11	1	12.5	492	492
	50A	12	1	12.5	706	1412
	50A	13	2	10	233	466
	50A	14	1	12.5	373	373
	50A	15	2	12.5	736	1472
	50A	16	2	12.5	469	938
	50A	17	136	6.3	146	19856
	50A	18	72	6.3	106	7632
V26						
	50A	1	2	12.5	705	1410
	50A	2	2	16	754	1508
	50A	3	2	16	734	1468
	50A	4	44	6.3	138	6072
	50A	5	44	6.3	84	3696
V27						
	50A	1	2	16	219	438
	50A	2	2	16	401	802
	50A	3	2	20	301	602
	50A	4	2	20	271	542
	50A	5	16	8	135	2160
	50A	6	8	6.3	94	752
V28						
	50A	1	4	16	222	888
	50A	2	4	10	289	1156
	50A	3	2	20	751	3004
	50A	4	4	16	751	3004
	50A	5	4	20	461	1844
	50A	6	4	16	442	1768
	50A	7	4	16	412	1648
	50A	8	4	10	202	808
	50A	9	130	6.3	144	18720
	50A	10	130	6.3	104	13520
V29=V39 (X2)						
	50A	1	4	10	633	2532
	50A	2	4	20	665	2660
	50A	3	2	20	597	1194
	50A	4	2	16	673	1346
	50A	5	68	6.3	314	21352
	50A	6	24	8	603	14472
	50A	7	116	6.3	146	16936
	50A	8	68	6.3	112	7616
V30						
	50A	1	2	10	226	452
	50A	2	3	12.5	204	612
	50A	3	3	16	260	780
	50A	4	2	16	624	1248
	50A	5	1	16	389	389
	50A	6	42	6.3	154	6468
	50A	7	4	10	553	2212
V31						
	50A	1	3	10	200	600
	50A	2	2	10	301	602
	50A	3	2	8	571	8552
	50A	4	4	20	625	2500
	50A	5	4	10	633	2532
	50A	6	3	16	330	990
	50A	7	21	8.0	112	3472
	50A	8	31	6.3	314	9734
V32						
	50A	1	4	16	222	888
	50A	2	4	10	289	1156
	50A	3	4	20	751	3004
	50A	4	4	16	751	3004
	50A	5	4	20	461	1844
	50A	6	4	16	442	1768
	50A	7	4	16	412	1648
	50A	8	4	10	202	808
	50A	9	130	6.3	144	18720
	50A	10	130	6.3	104	13520

RESUMO TOTAL AÇO CA 50-60

AÇO	BIT (mm)	COMPR (m)	PESO (kg)
50A	6.3	2019	495
50A	8	544	215
50A	10	291	179
50A	12.5	170	163
50A	16	488	770
50A	20	450	1109
Peso Total		50A =	2932 kg

V22

30X50 | 30X50 | 30X50

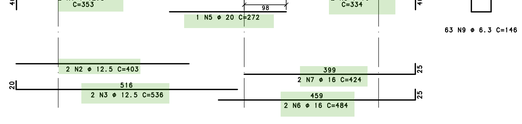


Corte A


63 N9 ø 6.3 C=146

V25

30X50 | 30X50 | 30X50 | 30X50 | 30X50 | 30X50

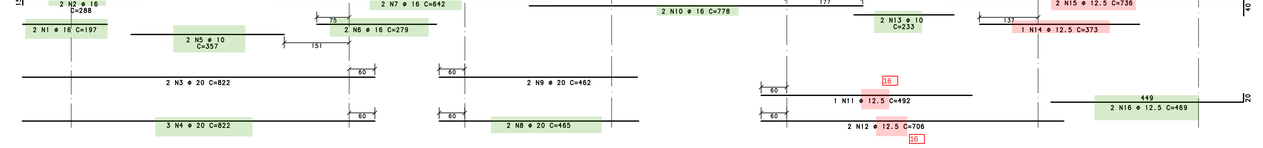

Corte A

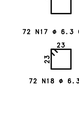

72 N17 ø 6.3 C=146

Corte B




64 N17 ø 6.3 C=146

72 N18 ø 6.3 C=106

V26

19X50 | 19X50 | 19X50

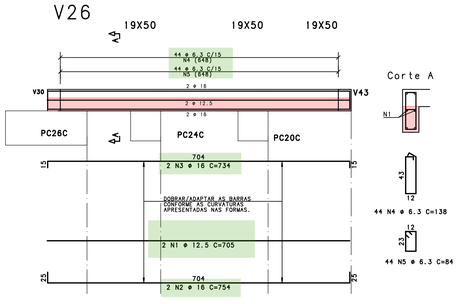


Corte A

44 N4 ø 6.3 C=138

44 N5 ø 6.3 C=84

V27

24X50

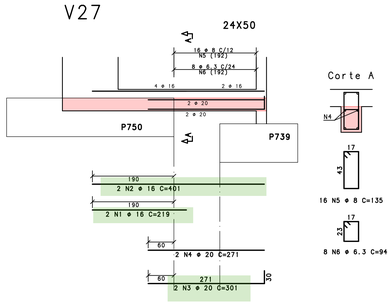


Corte A

16 N5 ø 8 C=135


8 N6 ø 6.3 C=94

V28

40X50 | 40X50

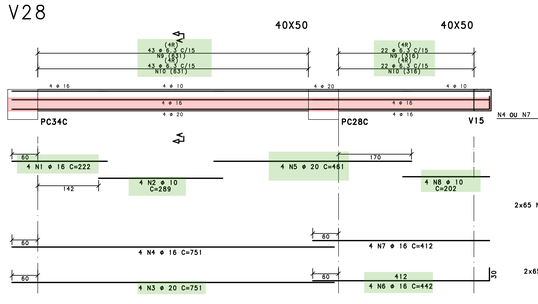

Corte A

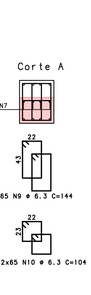


2x65 N9 ø 6.3 C=144

2x65 N10 ø 6.3 C=104

V29=V39

19X165

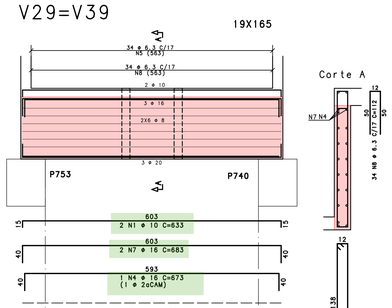

Corte A


34 N5 ø 6.3 C=314

LEGENDA

REGIÃO A SER CONCRETADA EM 1ª ETAPA

V30

24X60

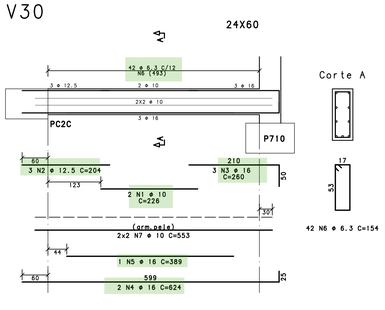


Corte A

42 N6 ø 6.3 C=154

V31

19X165

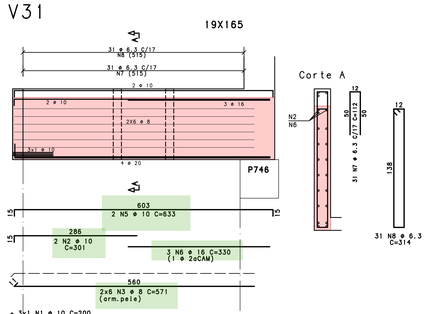


Corte A


31 N8 ø 6.3 C=314

V32

40X50 | 40X50

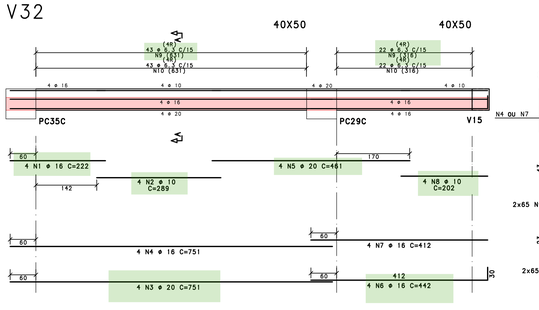

Corte A

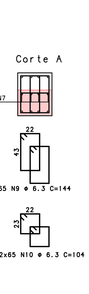

2x65 N9 ø 6.3 C=144

2x65 N10 ø 6.3 C=104

REV.	DATA	ALTERAÇÃO	VISTO
00	17/07/26	EMISSÃO INICIAL	FLP

PROCALK
ESTRUTURAS

RESP. TÉCNICOS
Eng. Eduardo C. Simmonetto
CREA-RS 63038
Eng. Carlos E.M. Morais
CREA-RS 76695

Rua João Abbott,473/401
Porto Alegre - CEP 90460-150
T (51)3013.3300
procalk@procalk.com.br
www.procalk.com.br

Obra: WERT PORTO BELO RESIDENCES
PORTO BELO - SC

Assunto: VIGAS - MULTI 02 - SETOR 7 TÉRREO

Conteúdo: V21 / V22 / V23+V24 / V25 / V26 / V27 / V28 V29=V39 / V30 / V31 / V32

Cliente: WERT

Número: 24-1454

Desenho: 7-402/0

Identificação: WTW-EST-01-1402-PLA-MUL-007-TE-R02

Desenho: FILIPE

Escala: 1:50

fck: 40/35 MPa

Data: 17/07/2026

Direitos Autorais Reservados Lei N. 9174/66

PROCALK ESTRUTURAS PL 4-00 00 PLT 17/07/2026 14:52:31

PARA PLOTAGEM UTILIZAR EXCLUSIVAMENTE O ARQUIVO PLT OU PDF.