V33

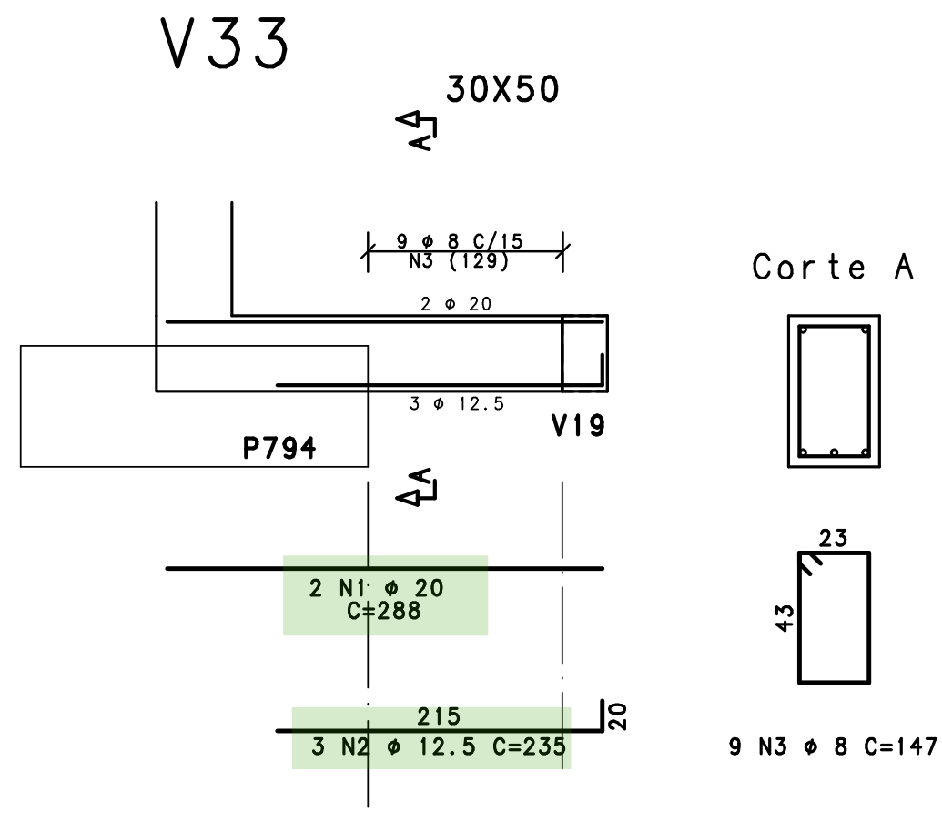
30X50
Corte A
P794
V19

V34

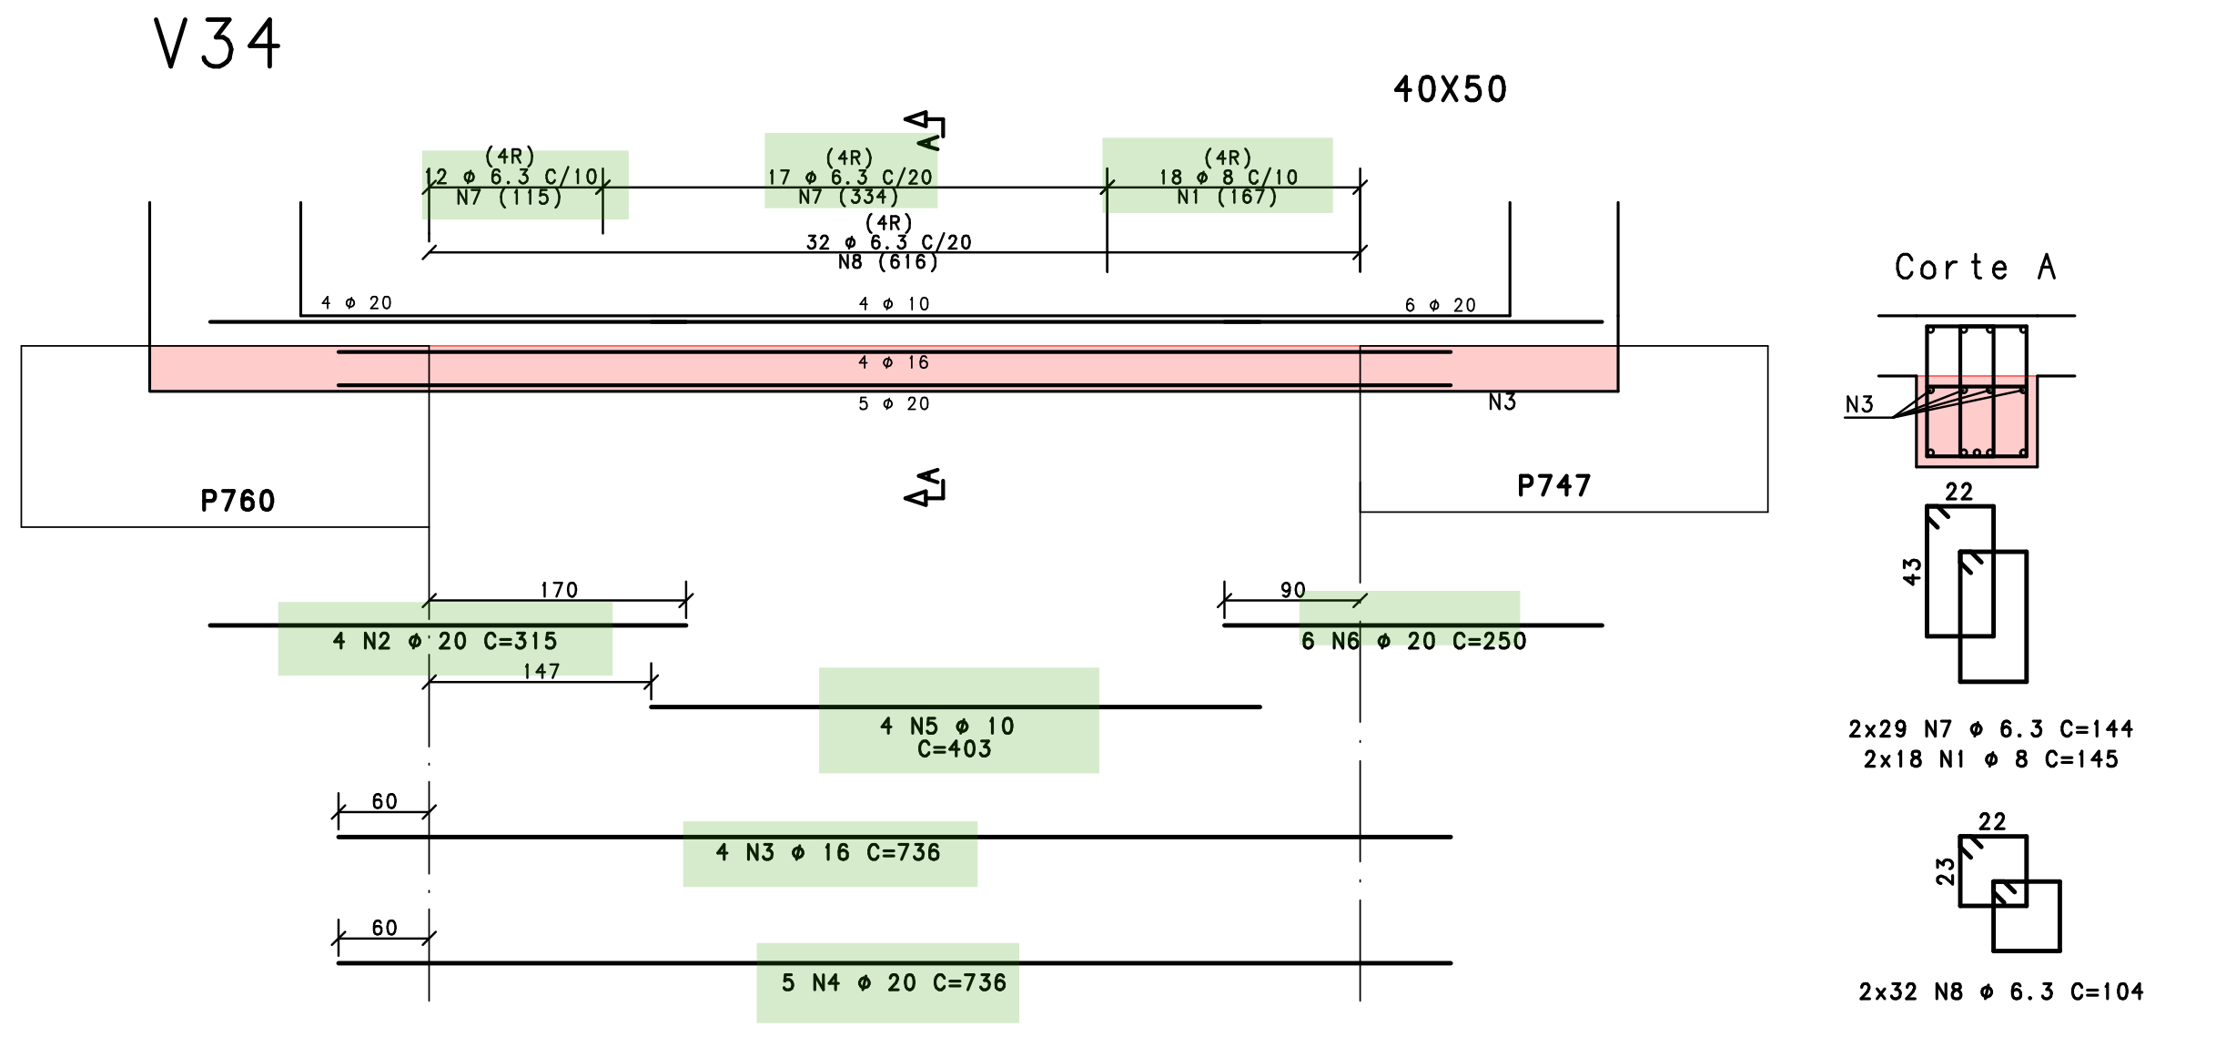
40X50
Corte A
P760
P747

V35

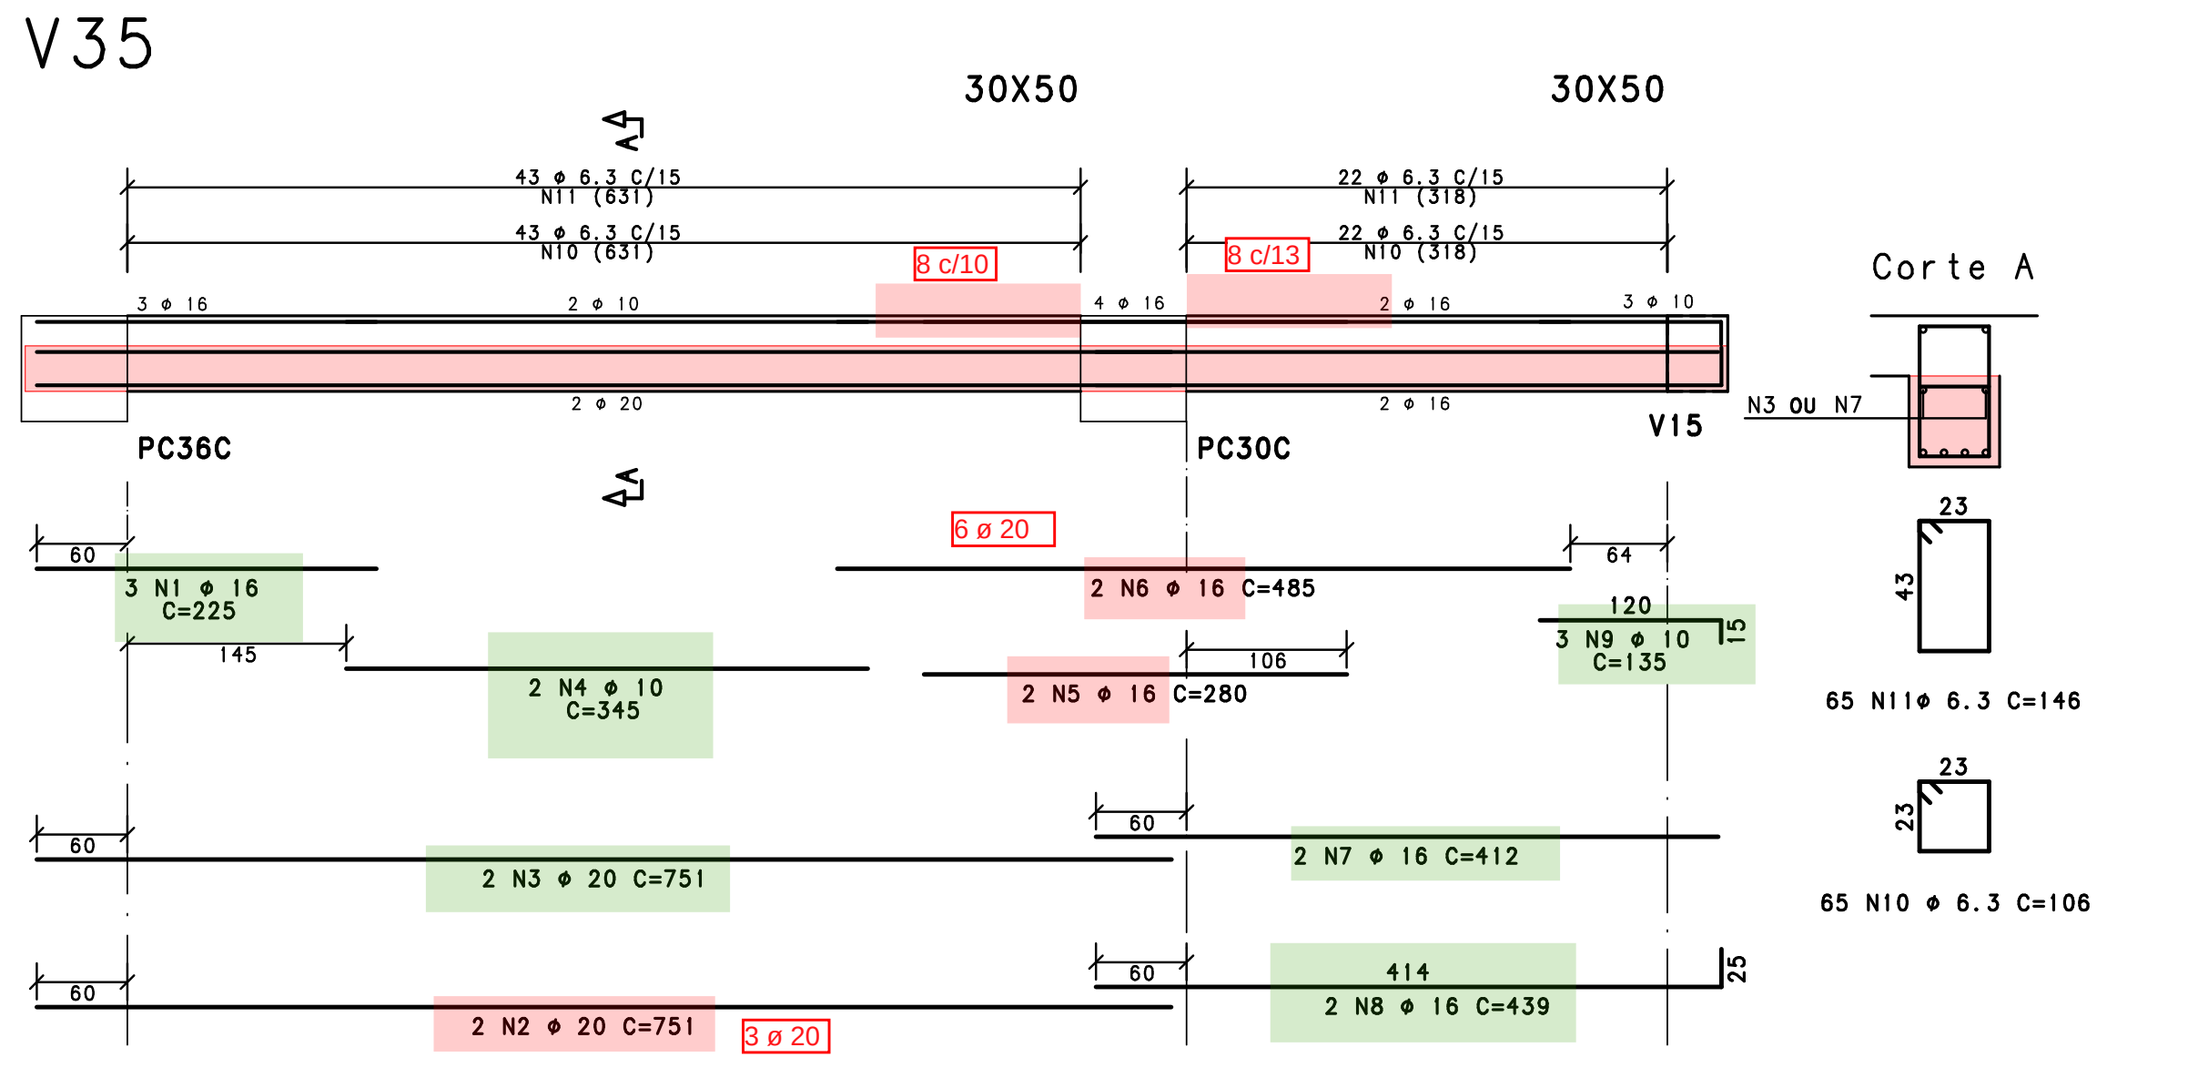
30X50
30X50
Corte A
PC36C
PC30C
V15

V36

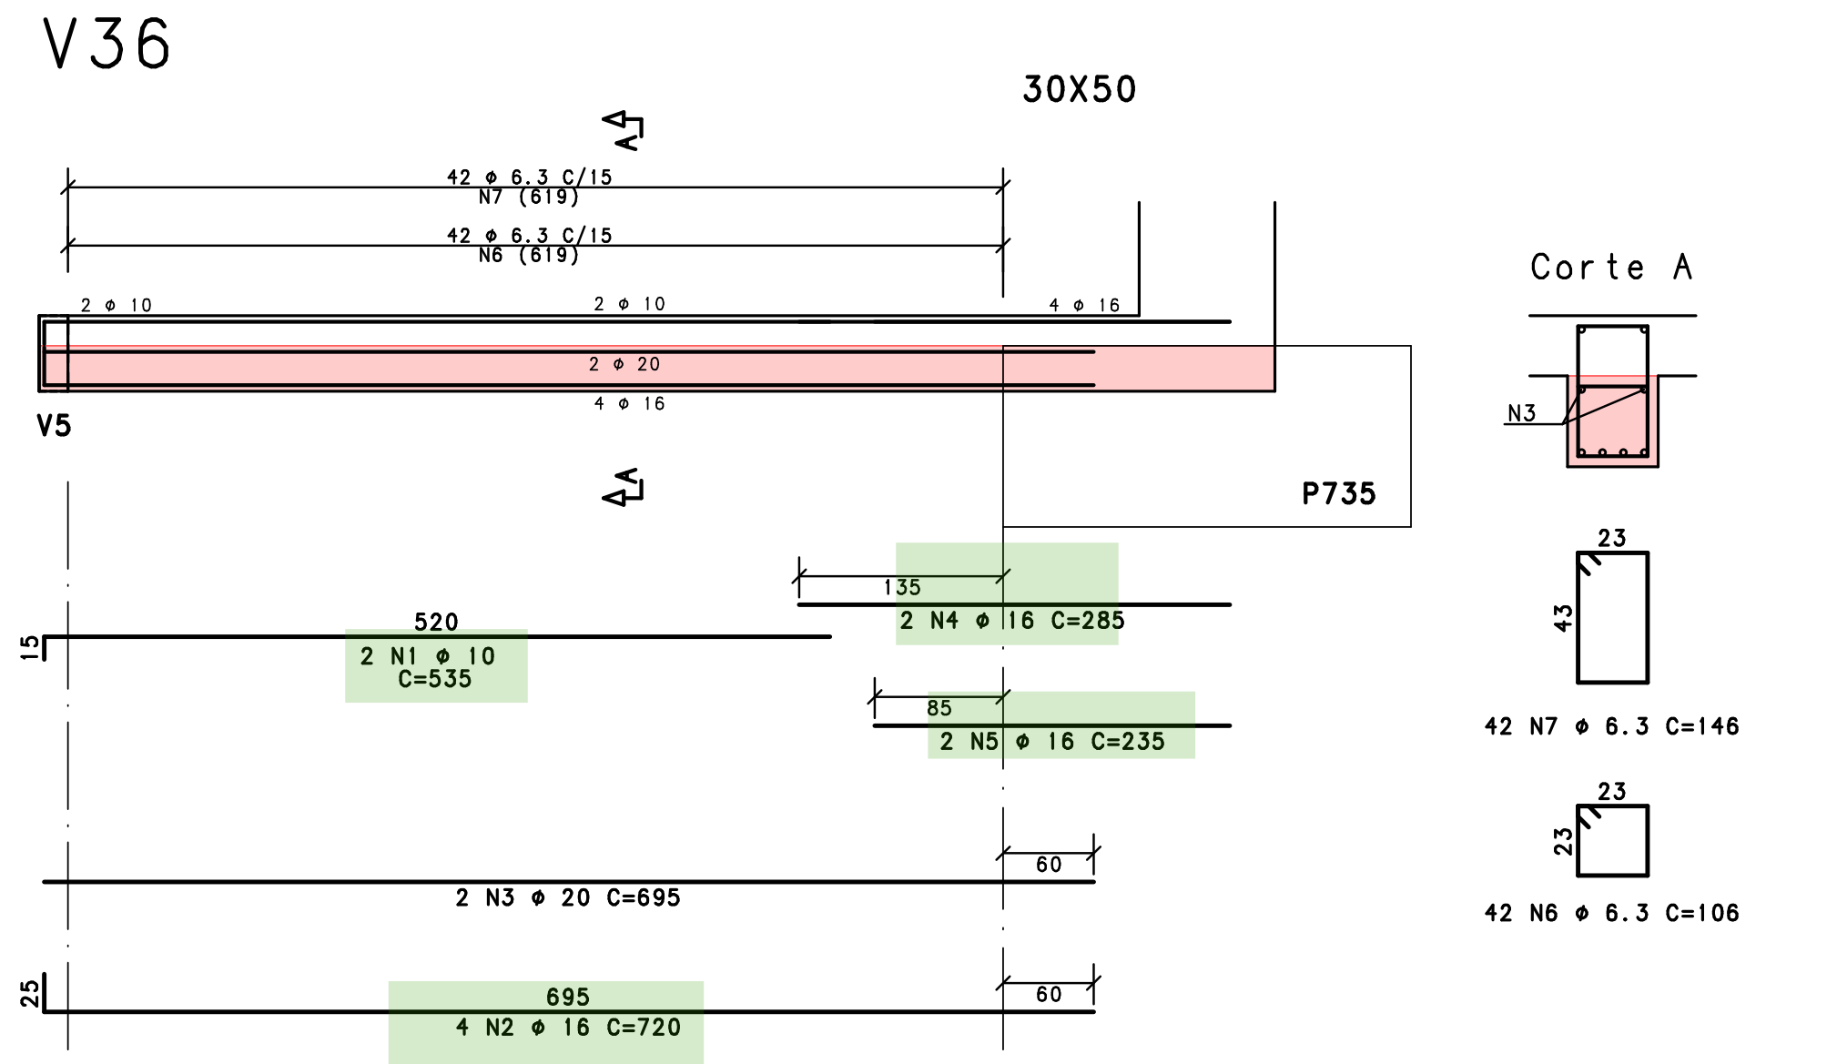
30X50
Corte A
V5
P735

V37

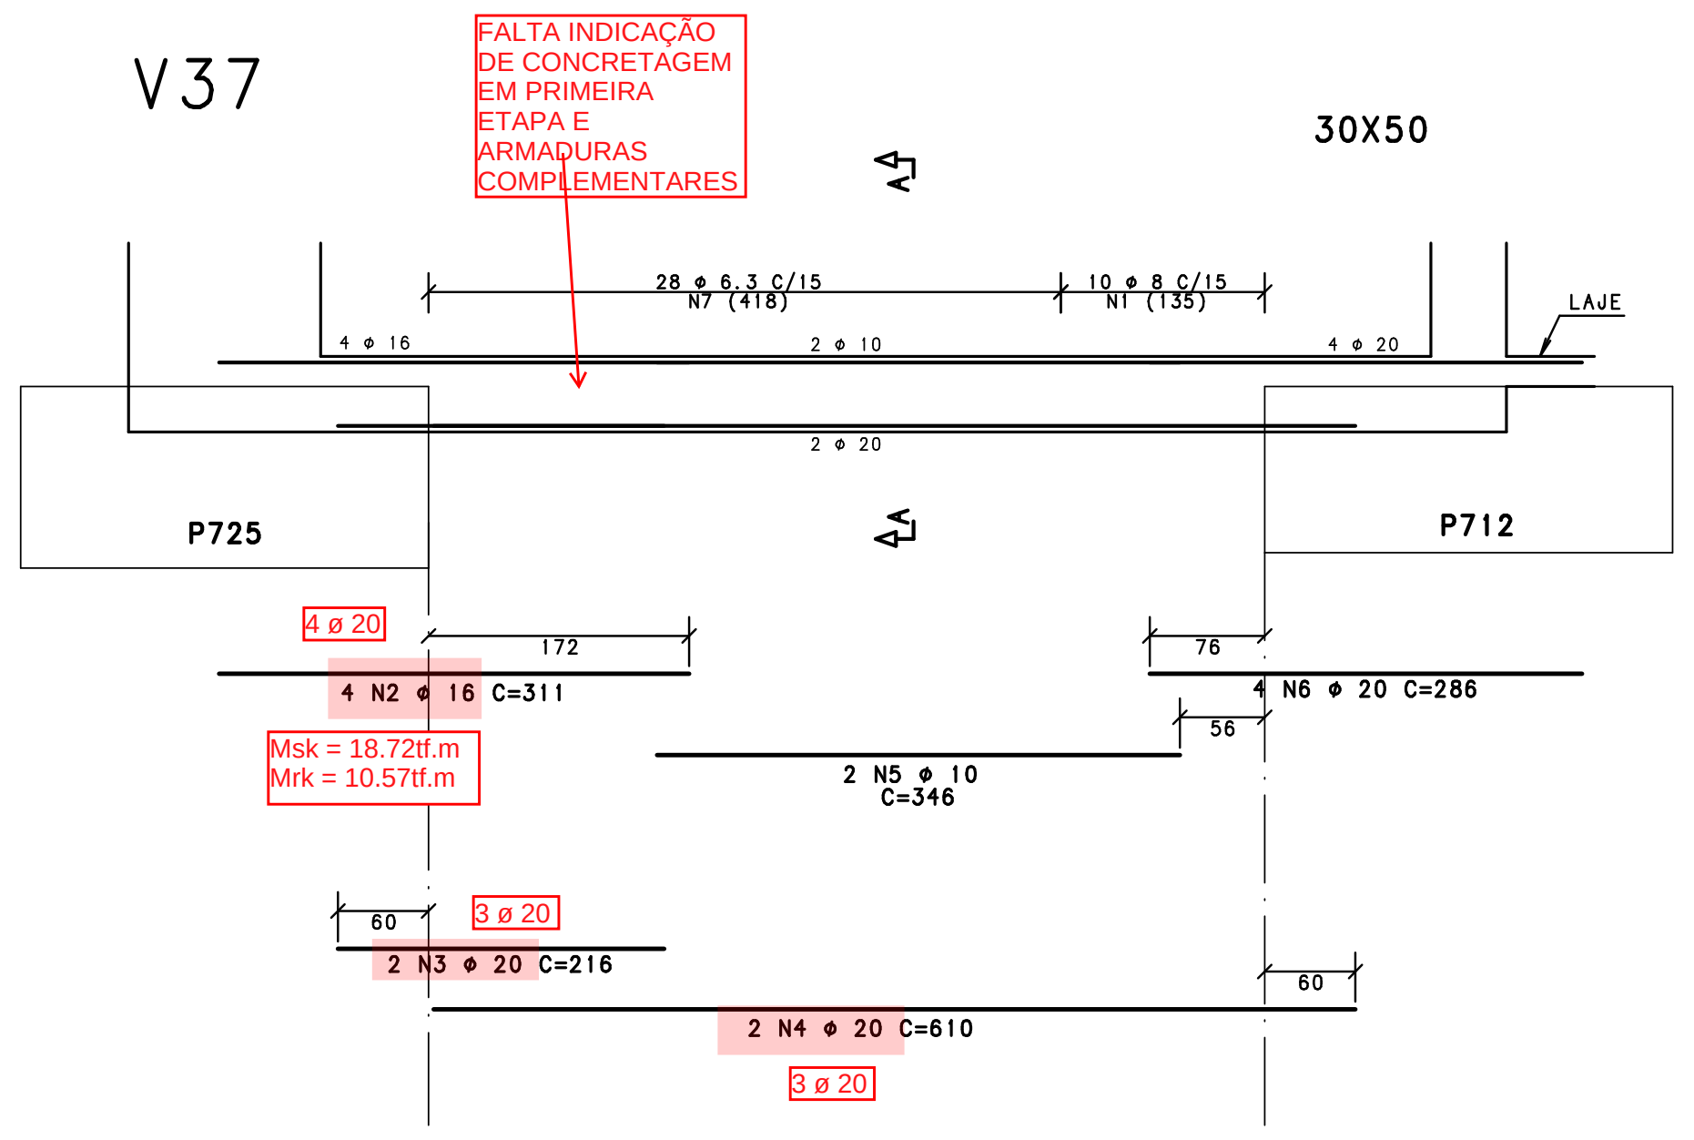
FALTA INDICAÇÃO DE CONCRETAGEM EM PRIMEIRA ETAPA E ARMADURAS COMPLEMENTARES
30X50
Corte A
28 ϕ 6.3 C/15
N7 (418)
4 ϕ 16
2 ϕ 10
2 ϕ 20
P725
P712
4 ø 20
172
4 N2 ϕ 16 C=311
Msk = 18.72tf.m
Mrk = 10.57tf.m
2 N5 ϕ 10
C=346
60
3 ø 20
2 N3 ϕ 20 C=216
2 N4 ϕ 20 C=610
3 ø 20

V38

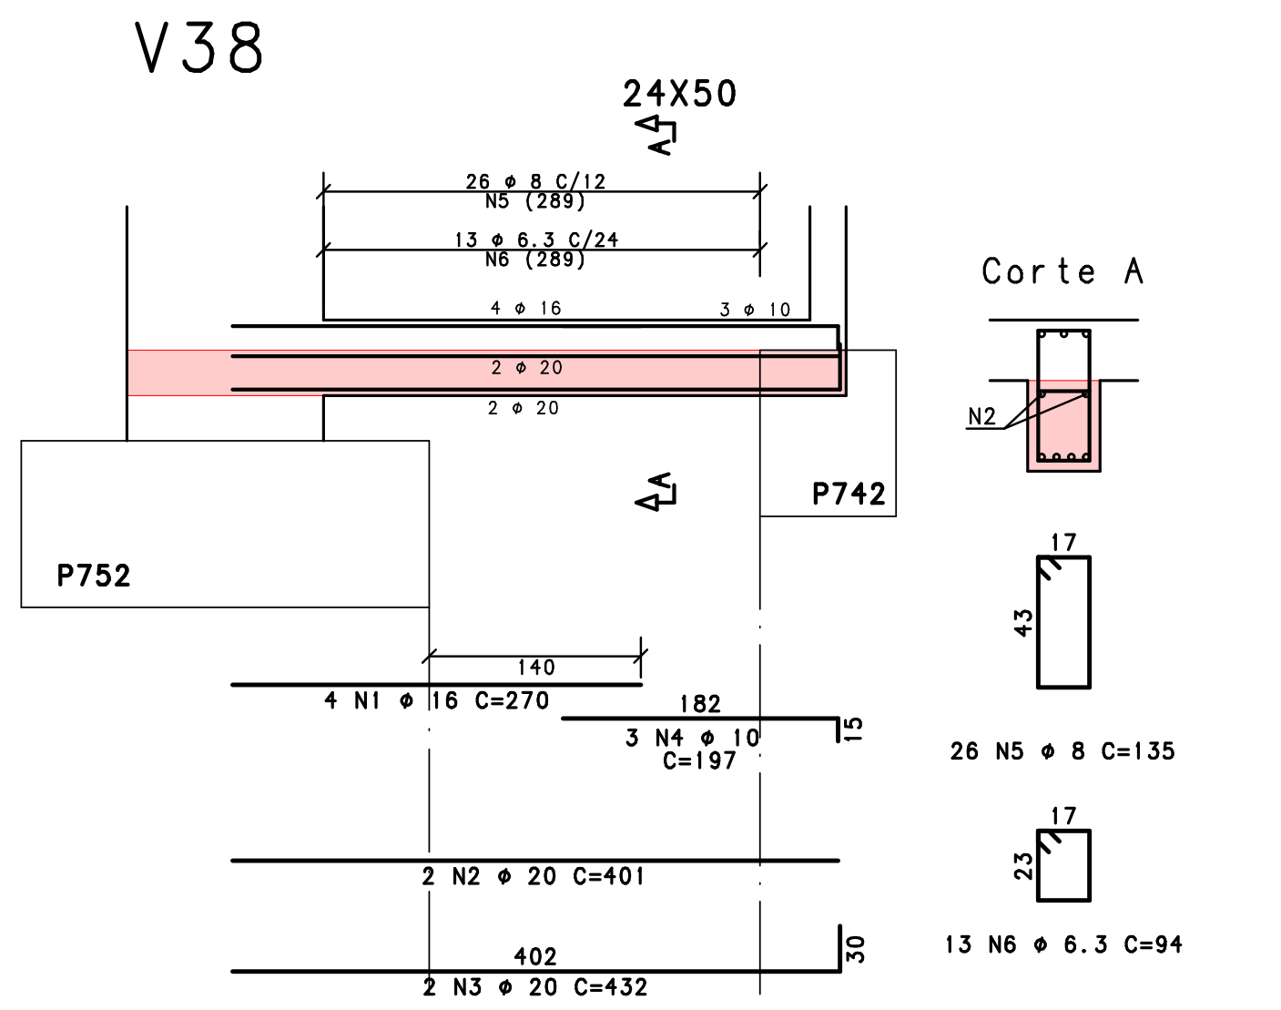
24X50
Corte A
P752
P742

V40

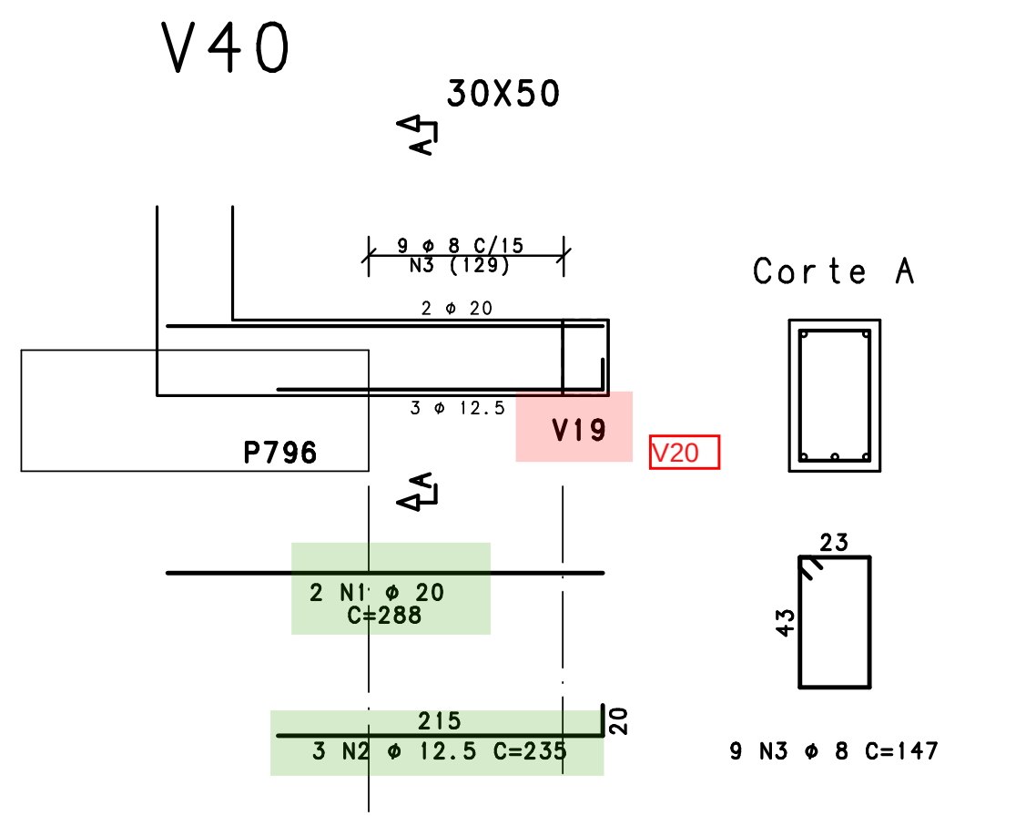
30X50
Corte A
P796
V19

V41

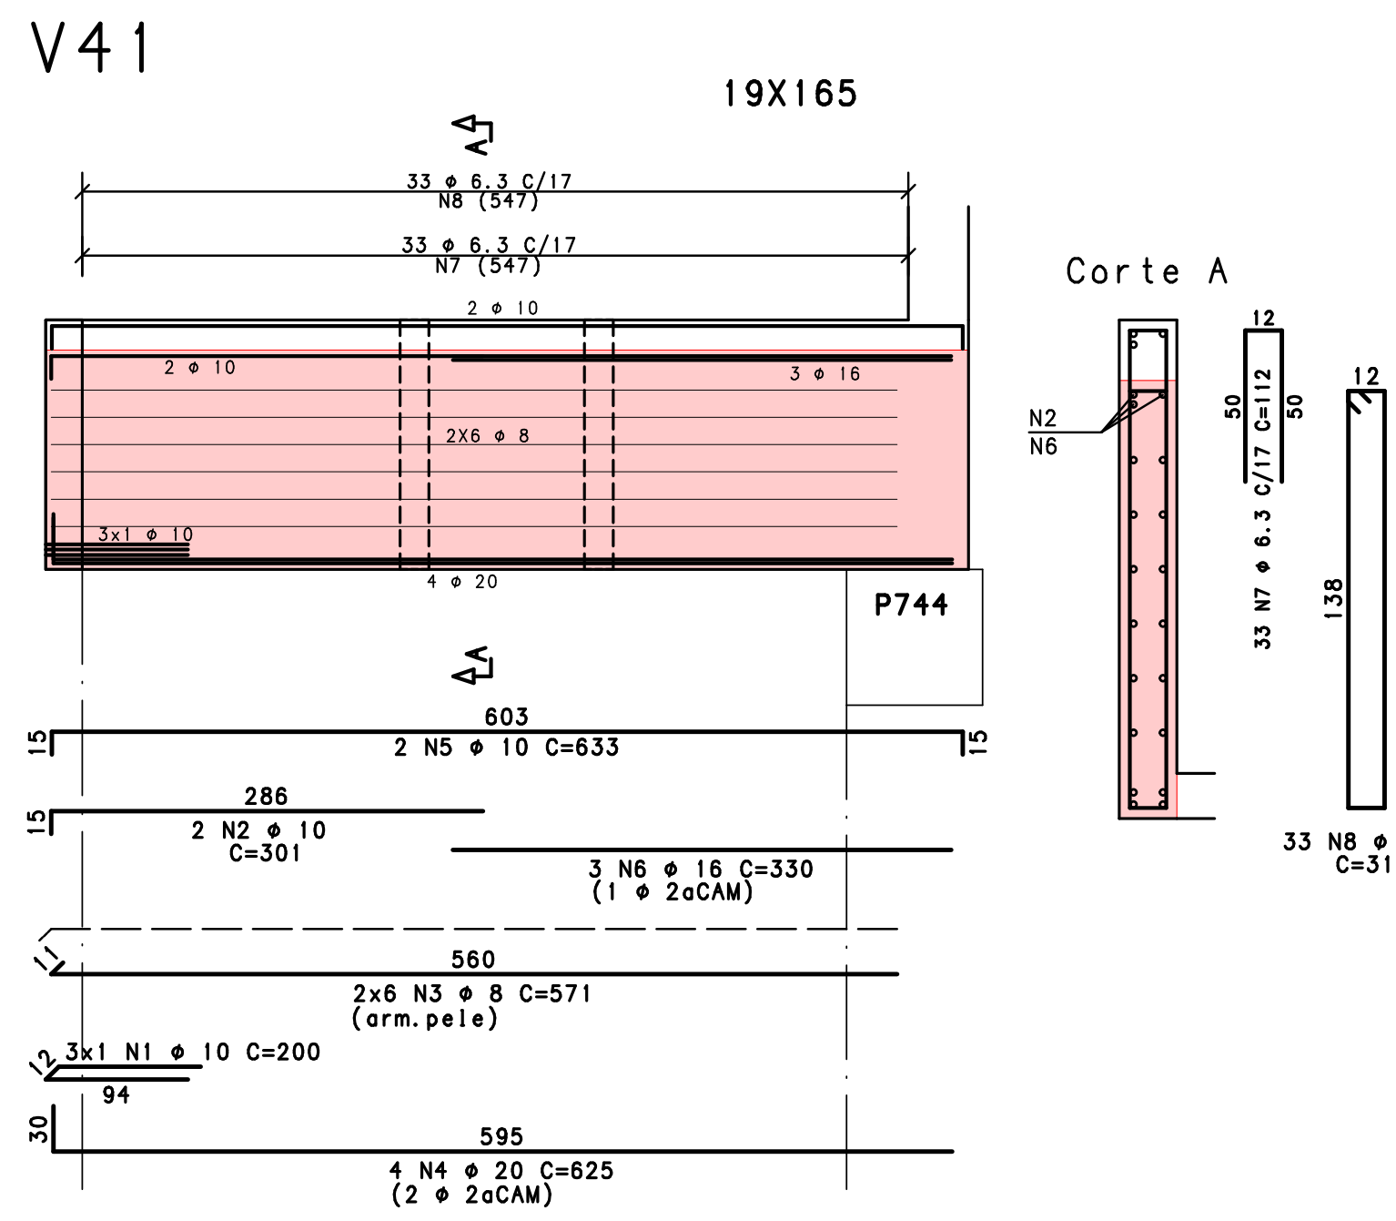
19X165
Corte A
P744

V46

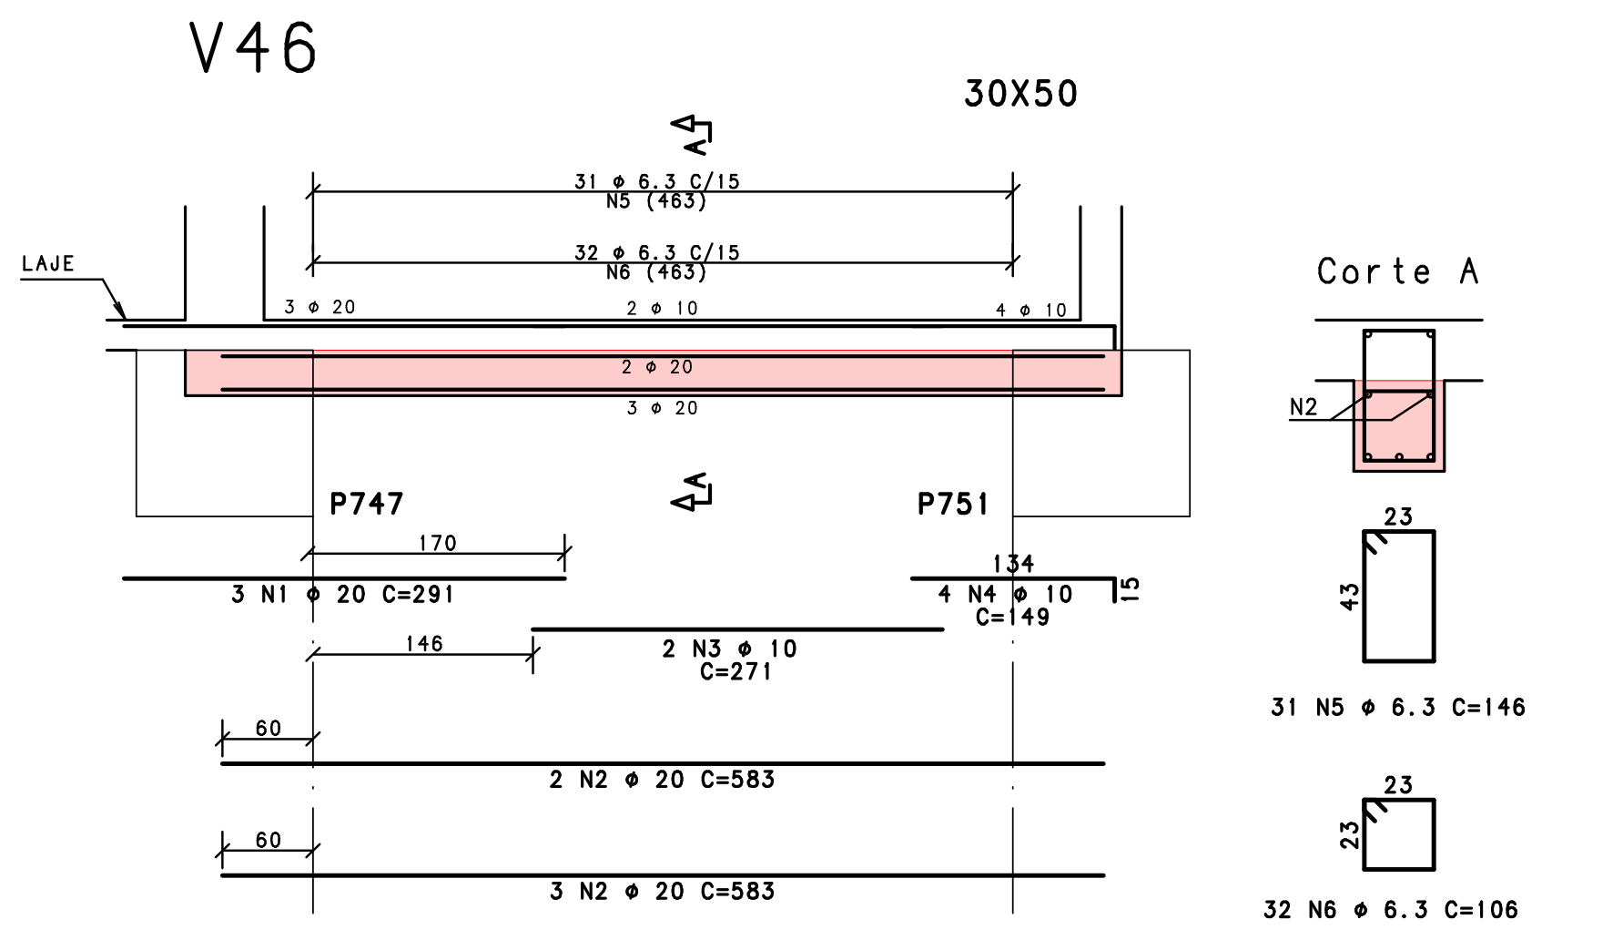
30X50
Corte A
P747
P751

V42

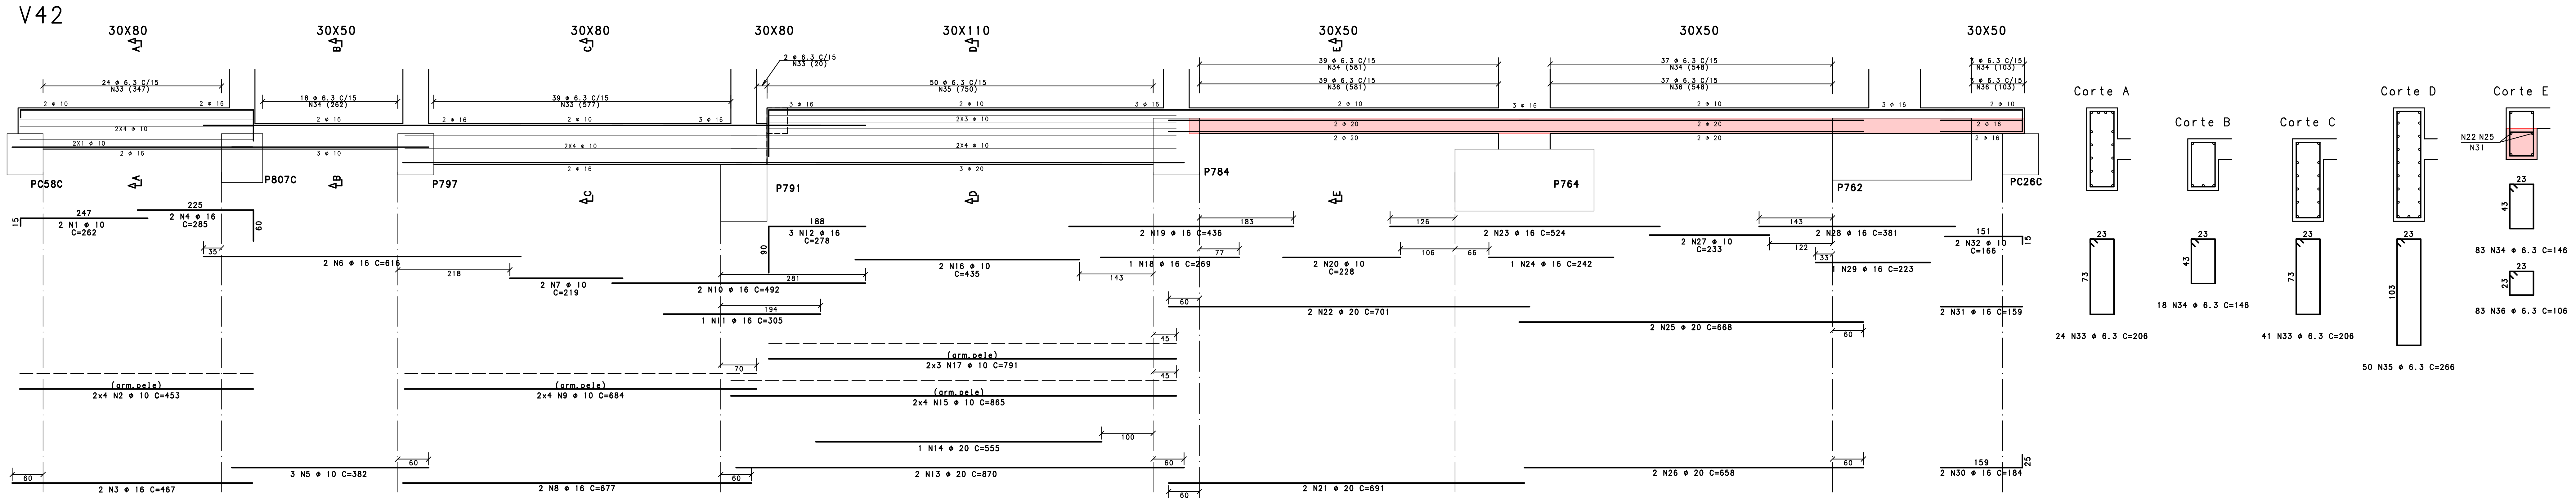
30X80
30X50
30X80
30X80
30X110
30X50
30X50
30X50
PC58C
P807C
P797
P791
P784
P764
P762
PC26C
Corte A
Corte B
Corte C
Corte D
Corte E

V43

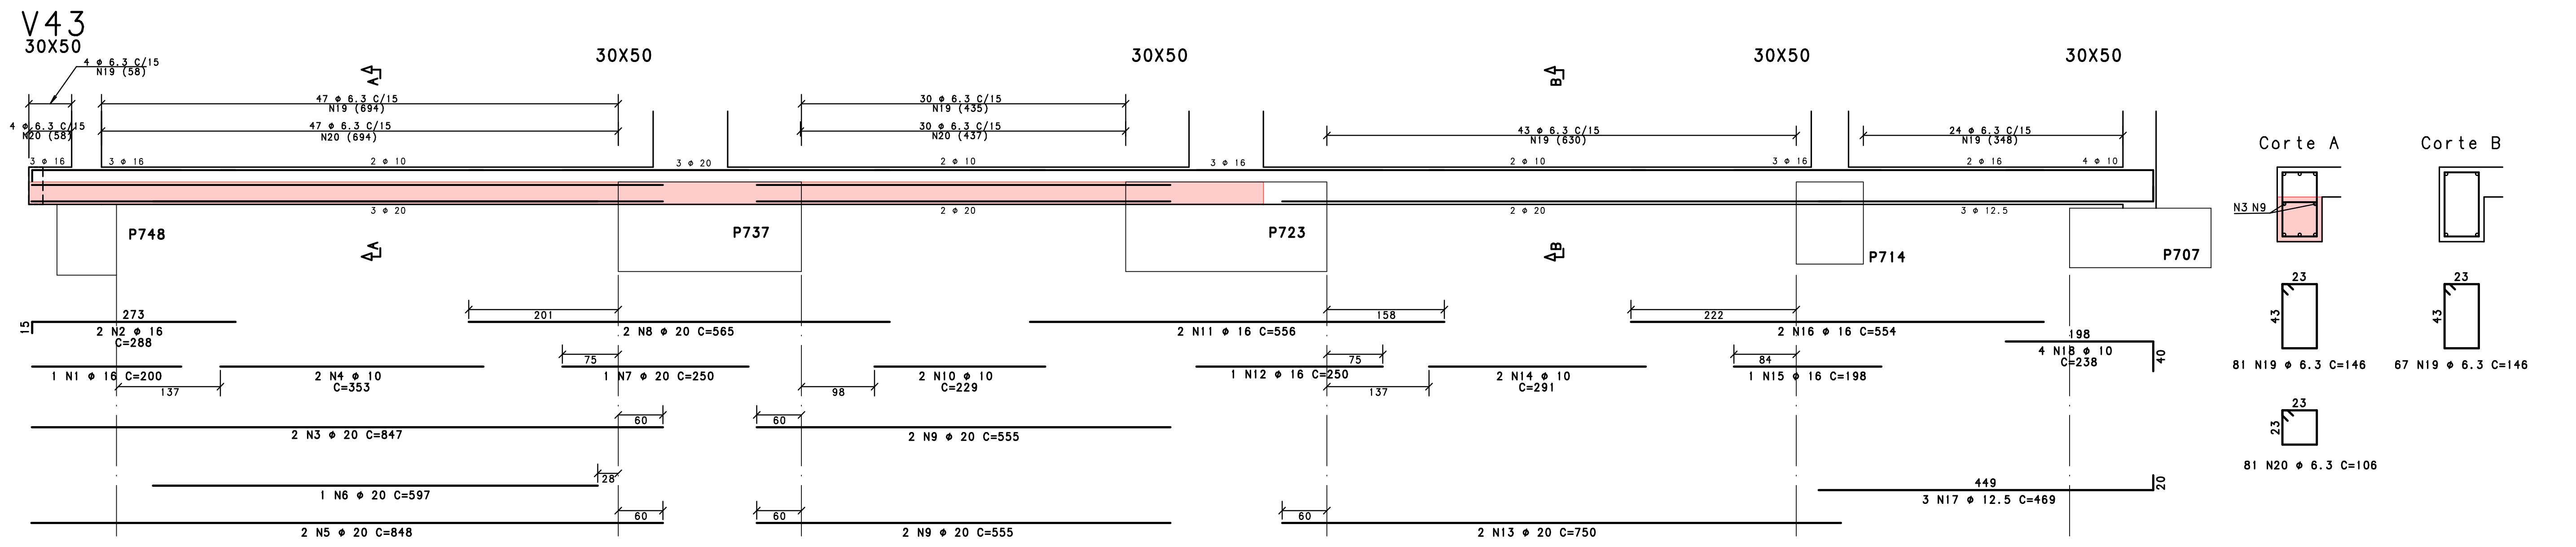
30X50
30X50
30X50
30X50
30X50
P748
P737
P723
P714
P707
Corte A
Corte B

V44

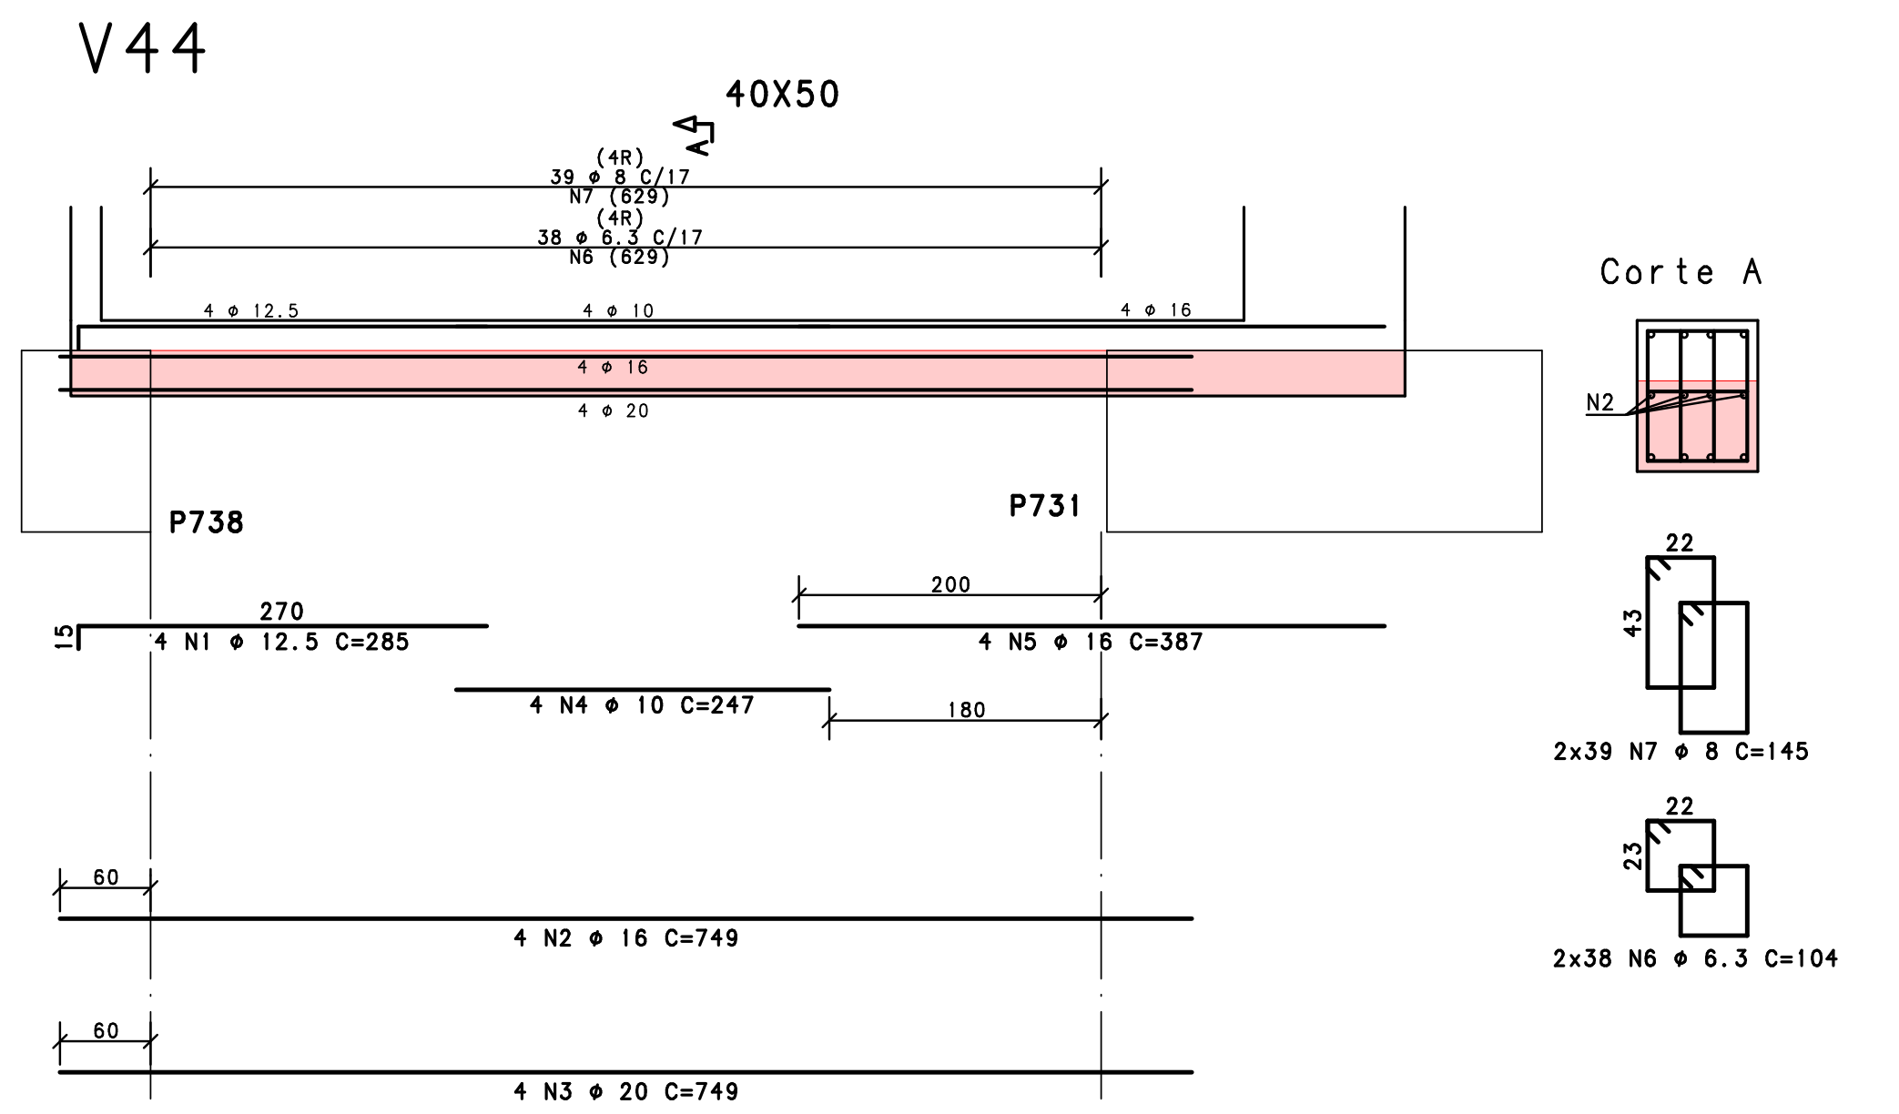
40X50
P738
P731
Corte A

V45

* AS DOBRAS DAS ARMADURAS, EM PLANTA, ACOMPANHAM A INCLINAÇÃO DA FORMA JUNTO AO P753

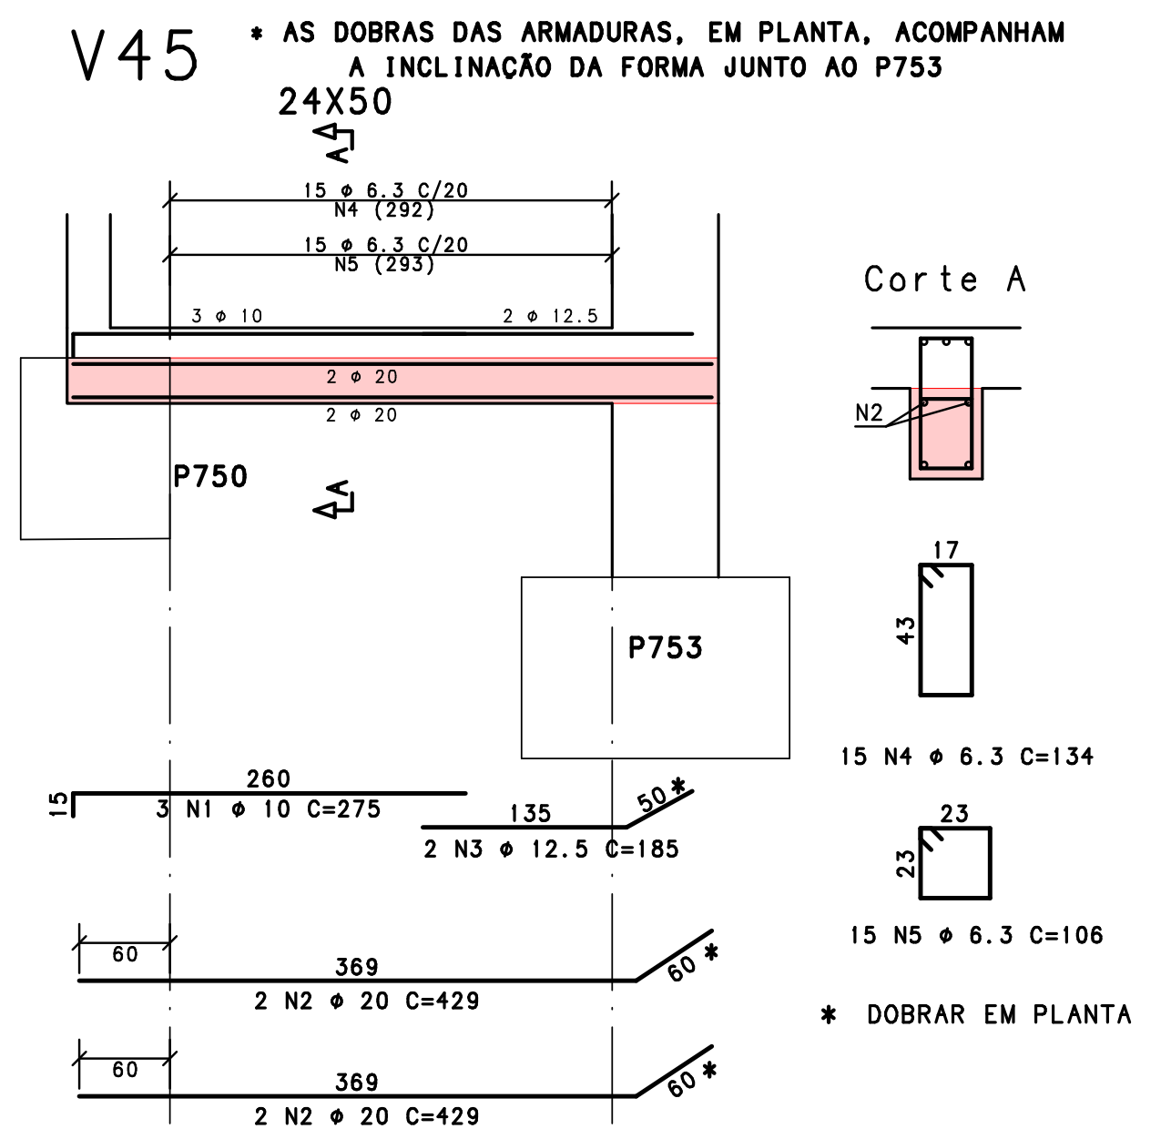
24X50
15 ϕ 6.3 C/20
N4 (292)
15 ϕ 6.3 C/20
N5 (293)
3 ϕ 10
2 ϕ 12.5
2 ϕ 20
2 ϕ 20
P750
P753
Corte A
N2
* DOBRAR EM PLANTA

V47

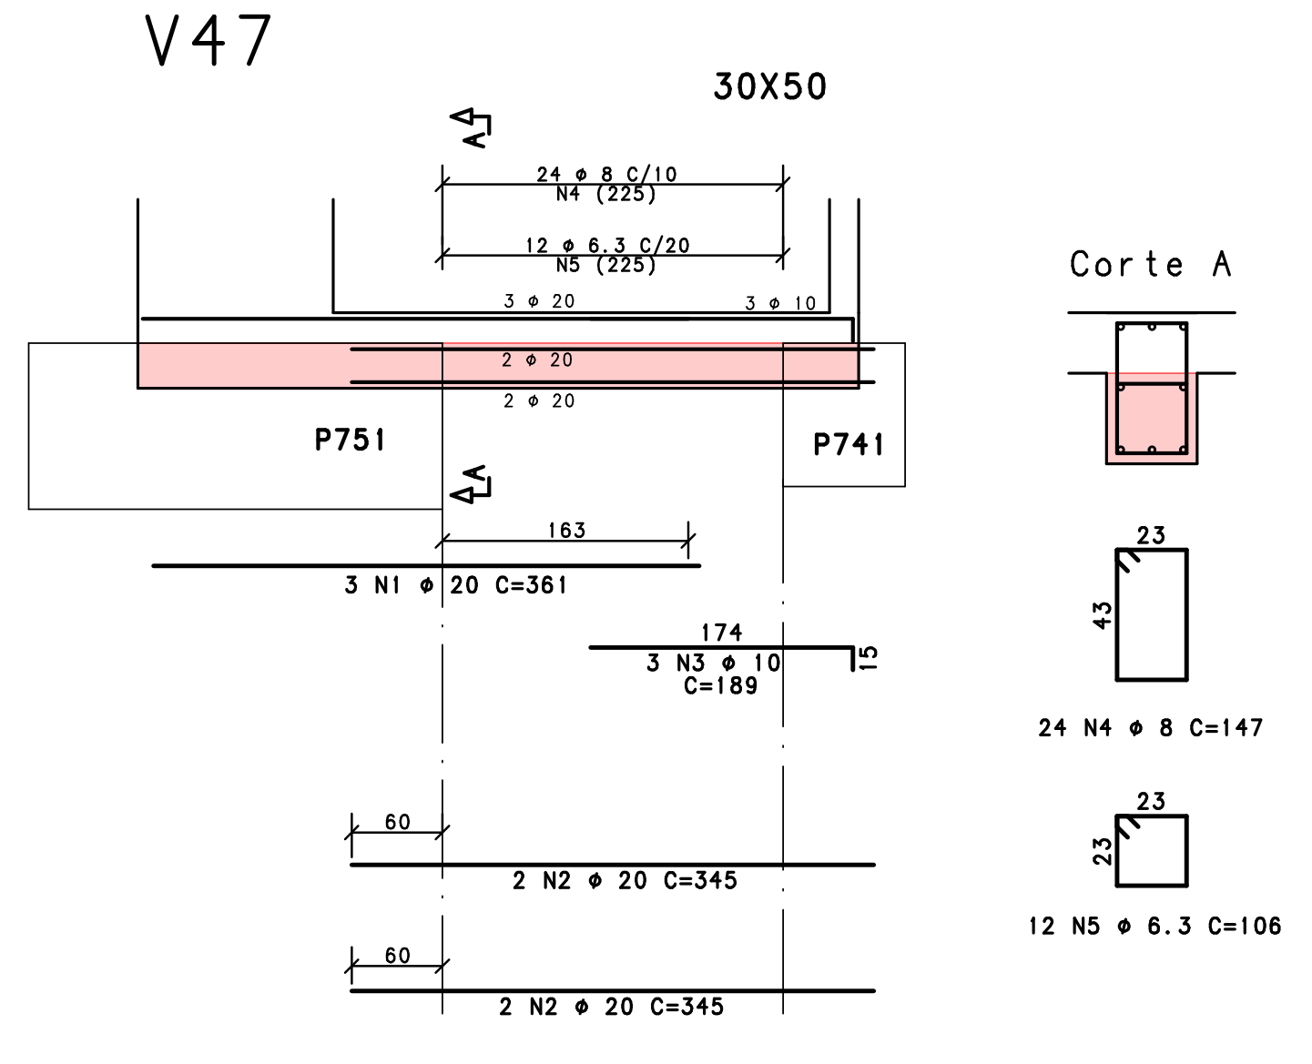
30X50
Corte A
P751
P741

V48

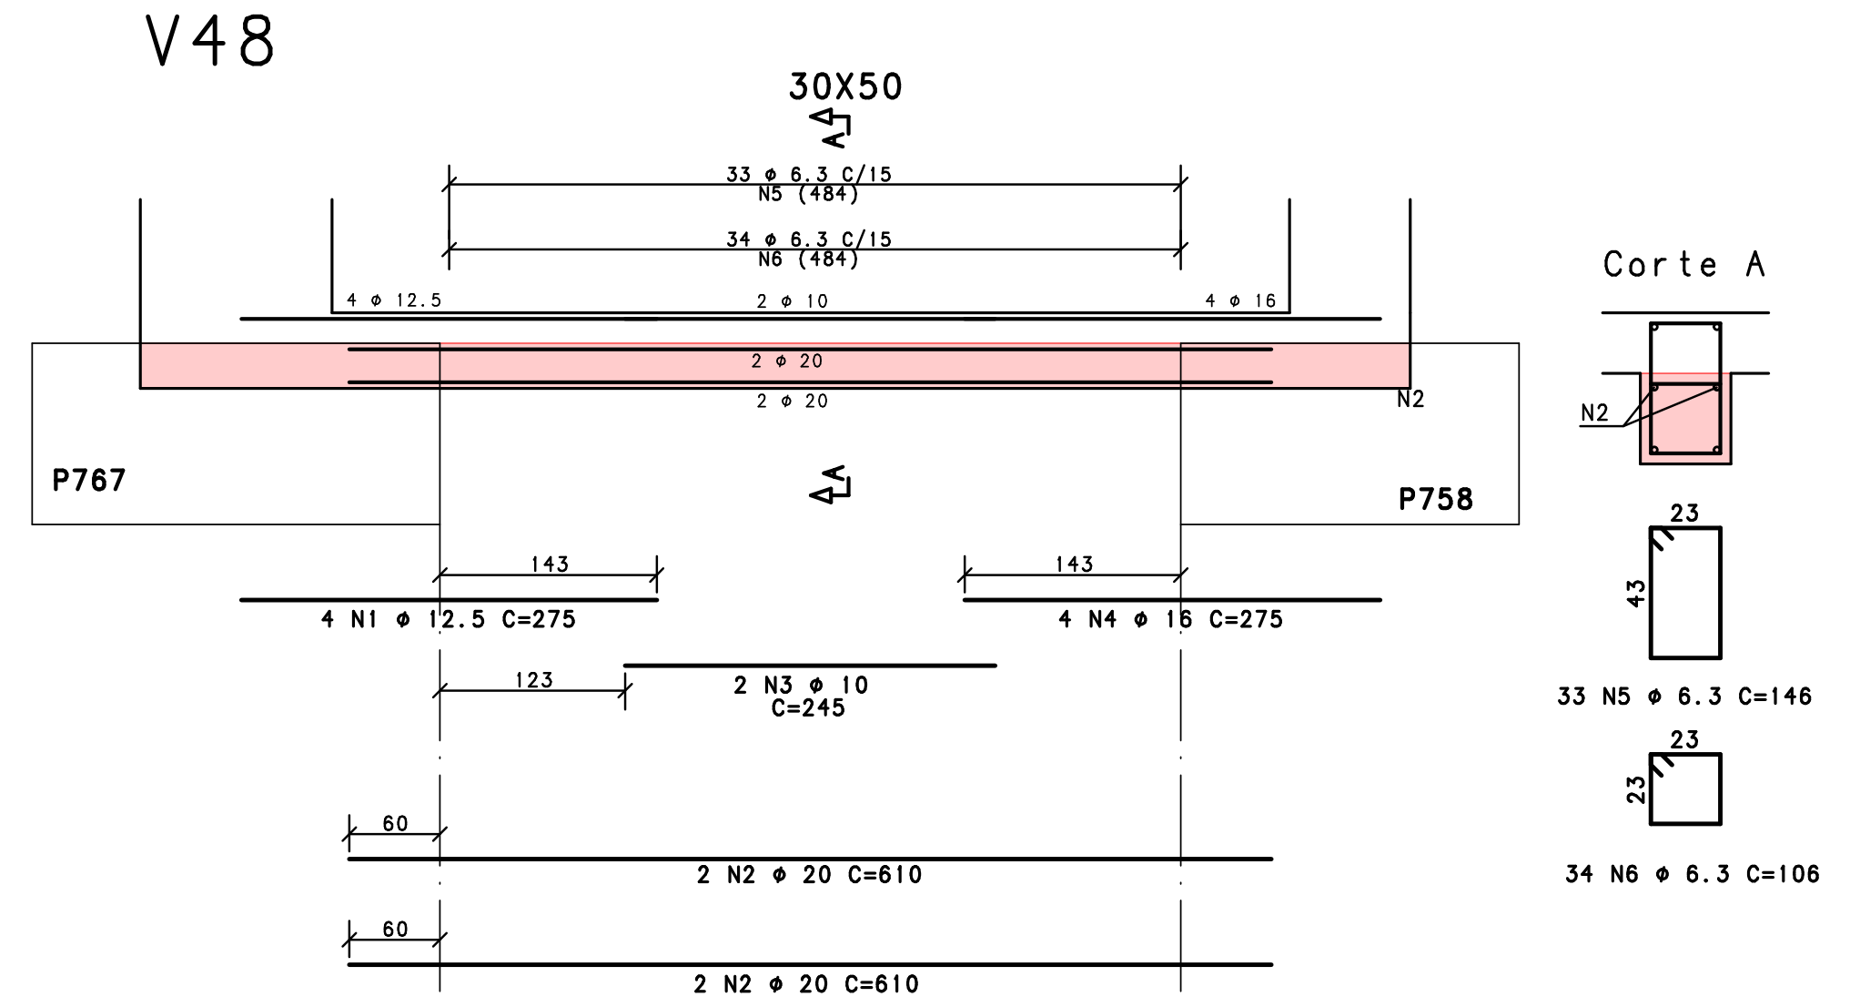
30X50
Corte A
P767
P758

V49

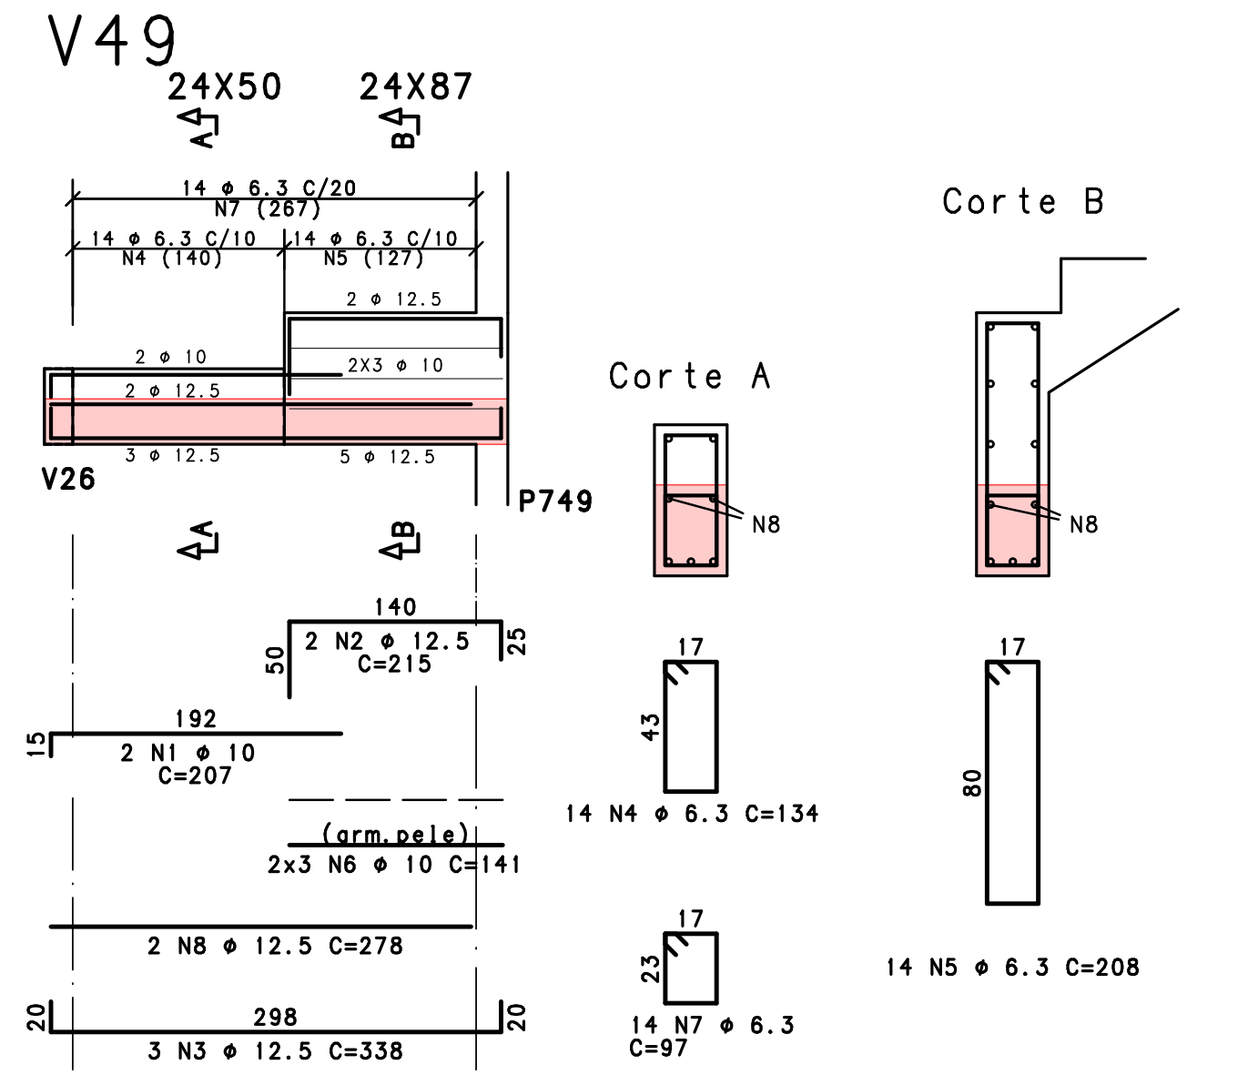
24X50
24X87
Corte A
Corte B
V26
P749

V50

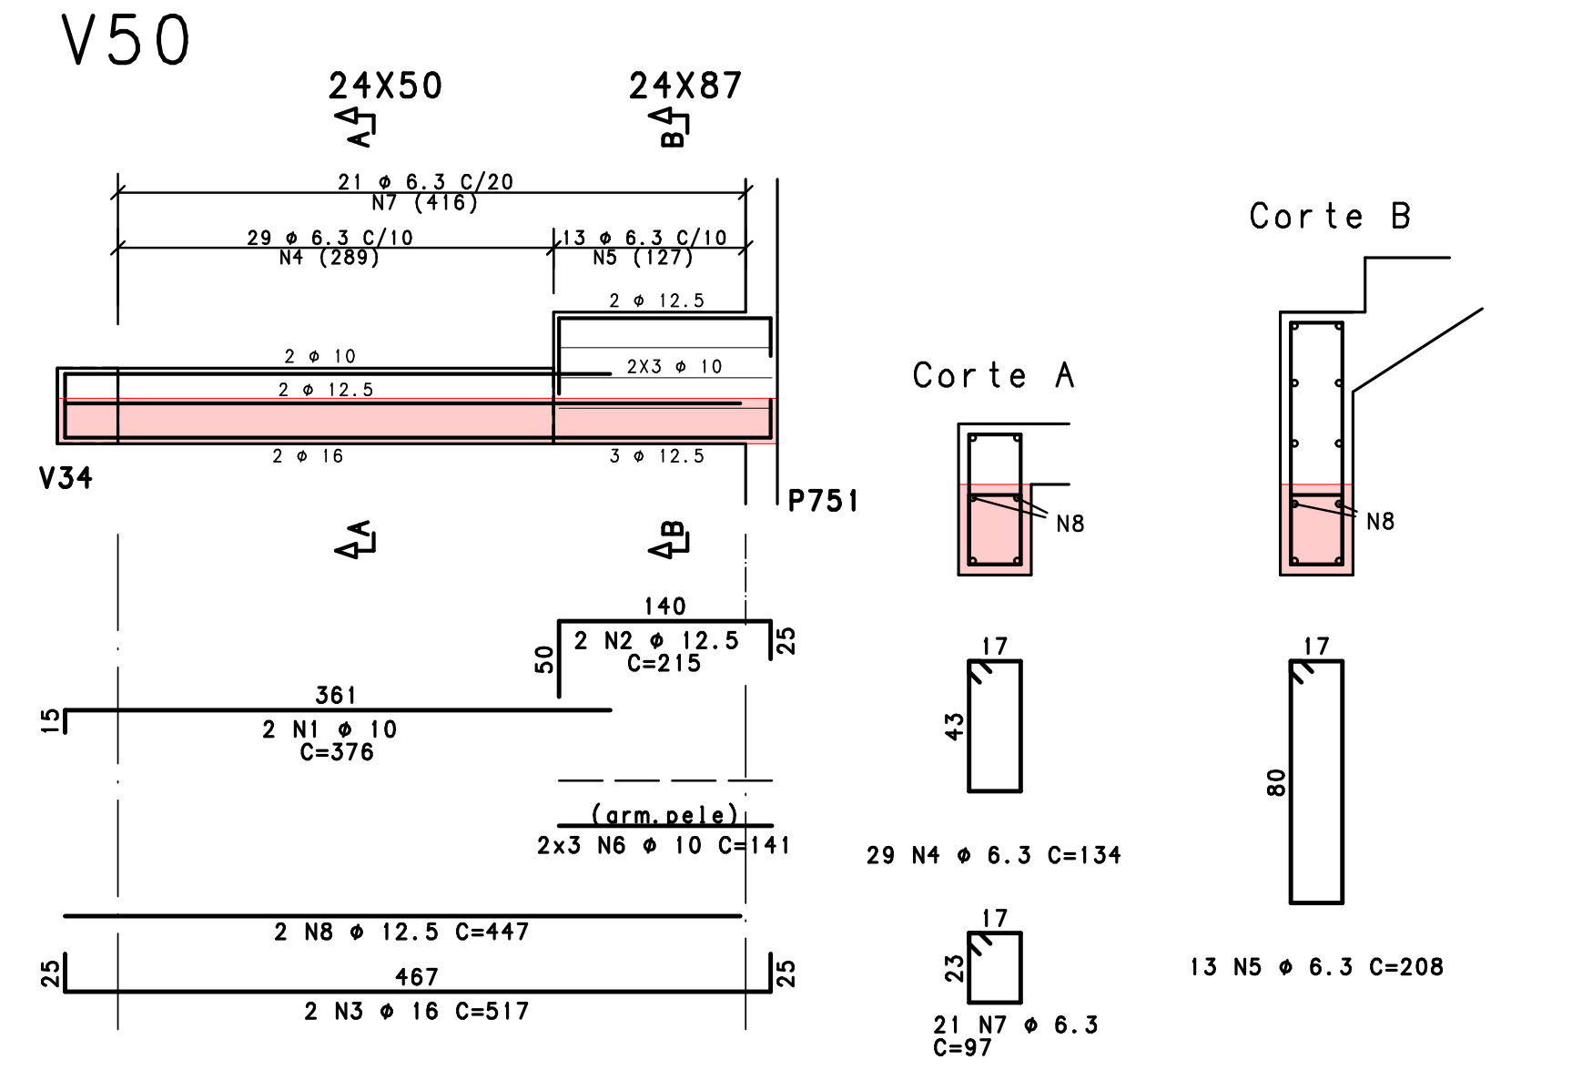
24X50
24X87
Corte A
Corte B
V34
P751

	AÇO	POS	QUANT	BIT (mm)	COMPRIMENTO	
					UNIT (cm)	TOTAL (cm)
V33						
	50A	1	2	20	288	576
	50A	2	3	12.5	235	705
	50A	3	9	8	147	1323
V34						
	50A	1	36	8	145	5220
	50A	2	4	20	315	1260
	50A	3	4	16	736	2944
	50A	4	5	20	736	3680
	50A	5	4	10	403	1612
	50A	6	6	20	250	1500
	50A	7	58	6.3	144	8352
	50A	8	64	6.3	104	6656
V35						
	50A	1	3	16	225	675
	50A	2	2	20	751	1502
	50A	3	2	20	751	1502
	50A	4	2	10	345	690
	50A	5	2	16	280	560
	50A	6	2	16	485	970
	50A	7	2	16	412	824
	50A	8	2	16	439	878
	50A	9	3	10	135	405
	50A	10	65	6.3	106	6890
	50A	11	65	6.3	146	9490
V36						
	50A	1	2	10	535	1070
	50A	2	4	16	720	2880
	50A	3	2	20	695	1390
	50A	4	2	16	285	570
	50A	5	2	16	235	470
	50A	6	42	6.3	106	4452
	50A	7	42	6.3	146	6132
V37						
	50A	1	10	8	147	1470
	50A	2	4	16	311	1244
	50A	3	2	20	216	432
	50A	4	2	20	610	1220
	50A	5	2	10	346	692
	50A	6	4	20	286	1144
	50A	7	28	6.3	146	4088
V38						
	50A	1	4	16	270	1080
	50A	2	2	20	401	802
	50A	3	2	20	432	864
	50A	4	3	10	197	591
	50A	5	26	8	135	3510
	50A	6	13	6.3	94	1222
V40						
	50A	1	2	20	288	576
	50A	2	3	12.5	235	705
	50A	3	9	8	147	1323
V41						
	50A	1	3	10	200	600
	50A	2	2	10	301	602
	50A	3	12	8	571	6852
	50A	4	4	20	625	2500
	50A	5	2	10	633	1266
	50A	6	3	16	330	990
	50A	7	33	6.3	112	3696
	50A	8	33	6.3	314	10362
V42						
	50A	1	2	10	262	524
	50A	2	8	10	453	3624
	50A	3	2	16	467	934
	50A	4	2	16	285	570
	50A	5	3	10	382	1146
	50A	6	2	16	616	1232
	50A	7	2	10	219	438
	50A	8	2	16	677	1354
	50A	9	8	10	684	5472
	50A	10	2	16	492	984
	50A	11	1	16	305	305
	50A	12	3	16	278	834
	50A	13	2	20	870	1740
	50A	14	1	20	555	555
	50A	15	8	10	865	6920
	50A	16	2	10	435	870
	50A	17	6	10	791	4746
	50A	18	1	16	269	269
	50A	19	2	16	436	872
	50A	20	2	10	228	456
	50A	21	2	20	691	1382
	50A	22	2	20	701	1402
	50A	23	2	16	524	1048
	50A	24	1	16	242	242
	50A	25	2	20	668	1336
	50A	26	2	20	658	1316
	50A	27	2	10	233	466
	50A	28	2	16	381	762
	50A	29	1	16	223	223
	50A	30	2	16	184	368
	50A	31	2	16	159	318
	50A	32	2	10	166	332
	50A	33	65	6.3	206	13390
	50A	34	101	6.3	146	14746
	50A	35	50	6.3	266	13300
	50A	36	83	6.3	106	8798
V43						
	50A	1	1	16	200	200
	50A	2	2	16	288	576
	50A	3	2	20	847	1694
	50A	4	2	10	353	706
	50A	5	2	20	848	1696
	50A	6	1	20	597	597
	50A	7	1	20	250	250
	50A	8	2	20	565	1130
	50A	9	4	20	555	2220
	50A	10	2	10	229	458
	50A	11	2	16	556	1112
	50A	12	1	16	250	250
	50A	13	2	20	750	1500
	50A	14	2	10	291	582
	50A	15	1	16	198	198
	50A	16	2	16	554	1108
	50A	17	3	12.5	469	1407
	50A	18	4	10	238	952
	50A	19	148	6.3	146	21608
	50A	20	81	6.3	106	8586
V44						
	50A	1	4	12.5	285	1140
	50A	2	4	16	749	2996
	50A	3	4	20	749	2996
	50A	4	4	10	247	988
	50A	5	4	16	387	1548
	50A	6	76	6.3	104	7904
	50A	7	78	8	145	11310
V45						
	50A	1	3	10	275	825
	50A	2	4	20	429	1716
	50A	3	2	12.5	185	370
	50A	4	15	6.3	134	2010
	50A	5	15	6.3	106	1590
V46						
	50A	1	3	20	291	873
	50A	2	5	20	583	2915
	50A	3	2	10	271	542
	50A	4	4	10	149	596
	50A	5	31	6.3	146	4526
	50A	6	32	6.3	106	3392
V47						
	50A	1	3	20	361	1083
	50A	2	4	20	345	1380
	50A	3	3	10	189	567
	50A	4	24	8	147	3528
	50A	5	12	6.3	106	1272
V48						
	50A	1	4	12.5	275	1100
	50A	2	4	20	610	2440
	50A	3	2	10	245	490
	50A	4	4	16	275	1100
	50A	5	33	6.3	146	4818
	50A	6	34	6.3	106	3604
V49						
	50A	1	2	10	207	414
	50A	2	2	12.5	215	430
	50A	3	3	12.5	338	1014
	50A	4	14	6.3	134	1876
	50A	5	14	6.3	208	2912
	50A	6	6	10	141	846
	50A	7	14	6.3	97	1358
	50A	8	2	12.5	278	556
V50						
	50A	1	2	10	376	752
	50A	2	2	12.5	215	430
	50A	3	2	16	517	1034
	50A	4	29	6.3	134	3886
	50A	5	13	6.3	208	2704
	50A	6	6	10	141	846
	50A	7	21	6.3	97	2037
	50A	8	2	12.5	447	894

RESUMO TOTAL AÇO CA 50-60

AÇO	BIT (mm)	COMPR (m)	PESO (kg)
50A	6.3	1857	455
50A	8	345	136
50A	10	421	260
50A	12.5	88	84
50A	16	345	545
50A	20	492	1213
Peso Total		50A =	2692 kgf

LEGENDA

🟥 REGIÃO A SER CONCRETADA EM 1° ETAPA

REV.	DATA	ALTERAÇÃO	VISTO
01	13/08/26	ACRESC.V49 E V50;MODIF.V34	DS
00	17/07/26	EMISSÃO INICIAL	FLP

PROCALK
ESTRUTURAS

RESP. TÉCNICOS
Eng. Edemir C. Simonato
CREA-RS 63038
Eng. Carlos R.M. Morais
CREA-RS 74695

Rua João Abbott, 473/401
Porto Alegre - CEP 90460-150
F. (51)3013.3200
procalk@procalk.com.br
www.procalk.com.br

Obra WERT PORTO BELO RESIDENCES
PORTO BELO - SC

Assunto VIGAS - MULTI 02 - SETOR 7
TÉRREO

Conteúdo V33 / V34 / V35 / V36 / V37 / V38 / V40 / V41
V42 / V43 / V44 / V45 / V46 / V47 / V48 / V49
V50

Cliente WERT
Número 24-1454
Desenho 7-403/1
Identificação WPBR-EST-EX-7403-PLN-MU2-S07-TE-R01
Desenho FILIPE
Escala 1:50
fck 40/35 MPa
Data 17/07/2026

PARA PLOTAGEM UTILIZAR EXCLUSIVAMENTE O ARQUIVO PLT OU PDF.

Direitos Autorais Reservados Lei N 5194/66