PAR701

30X442

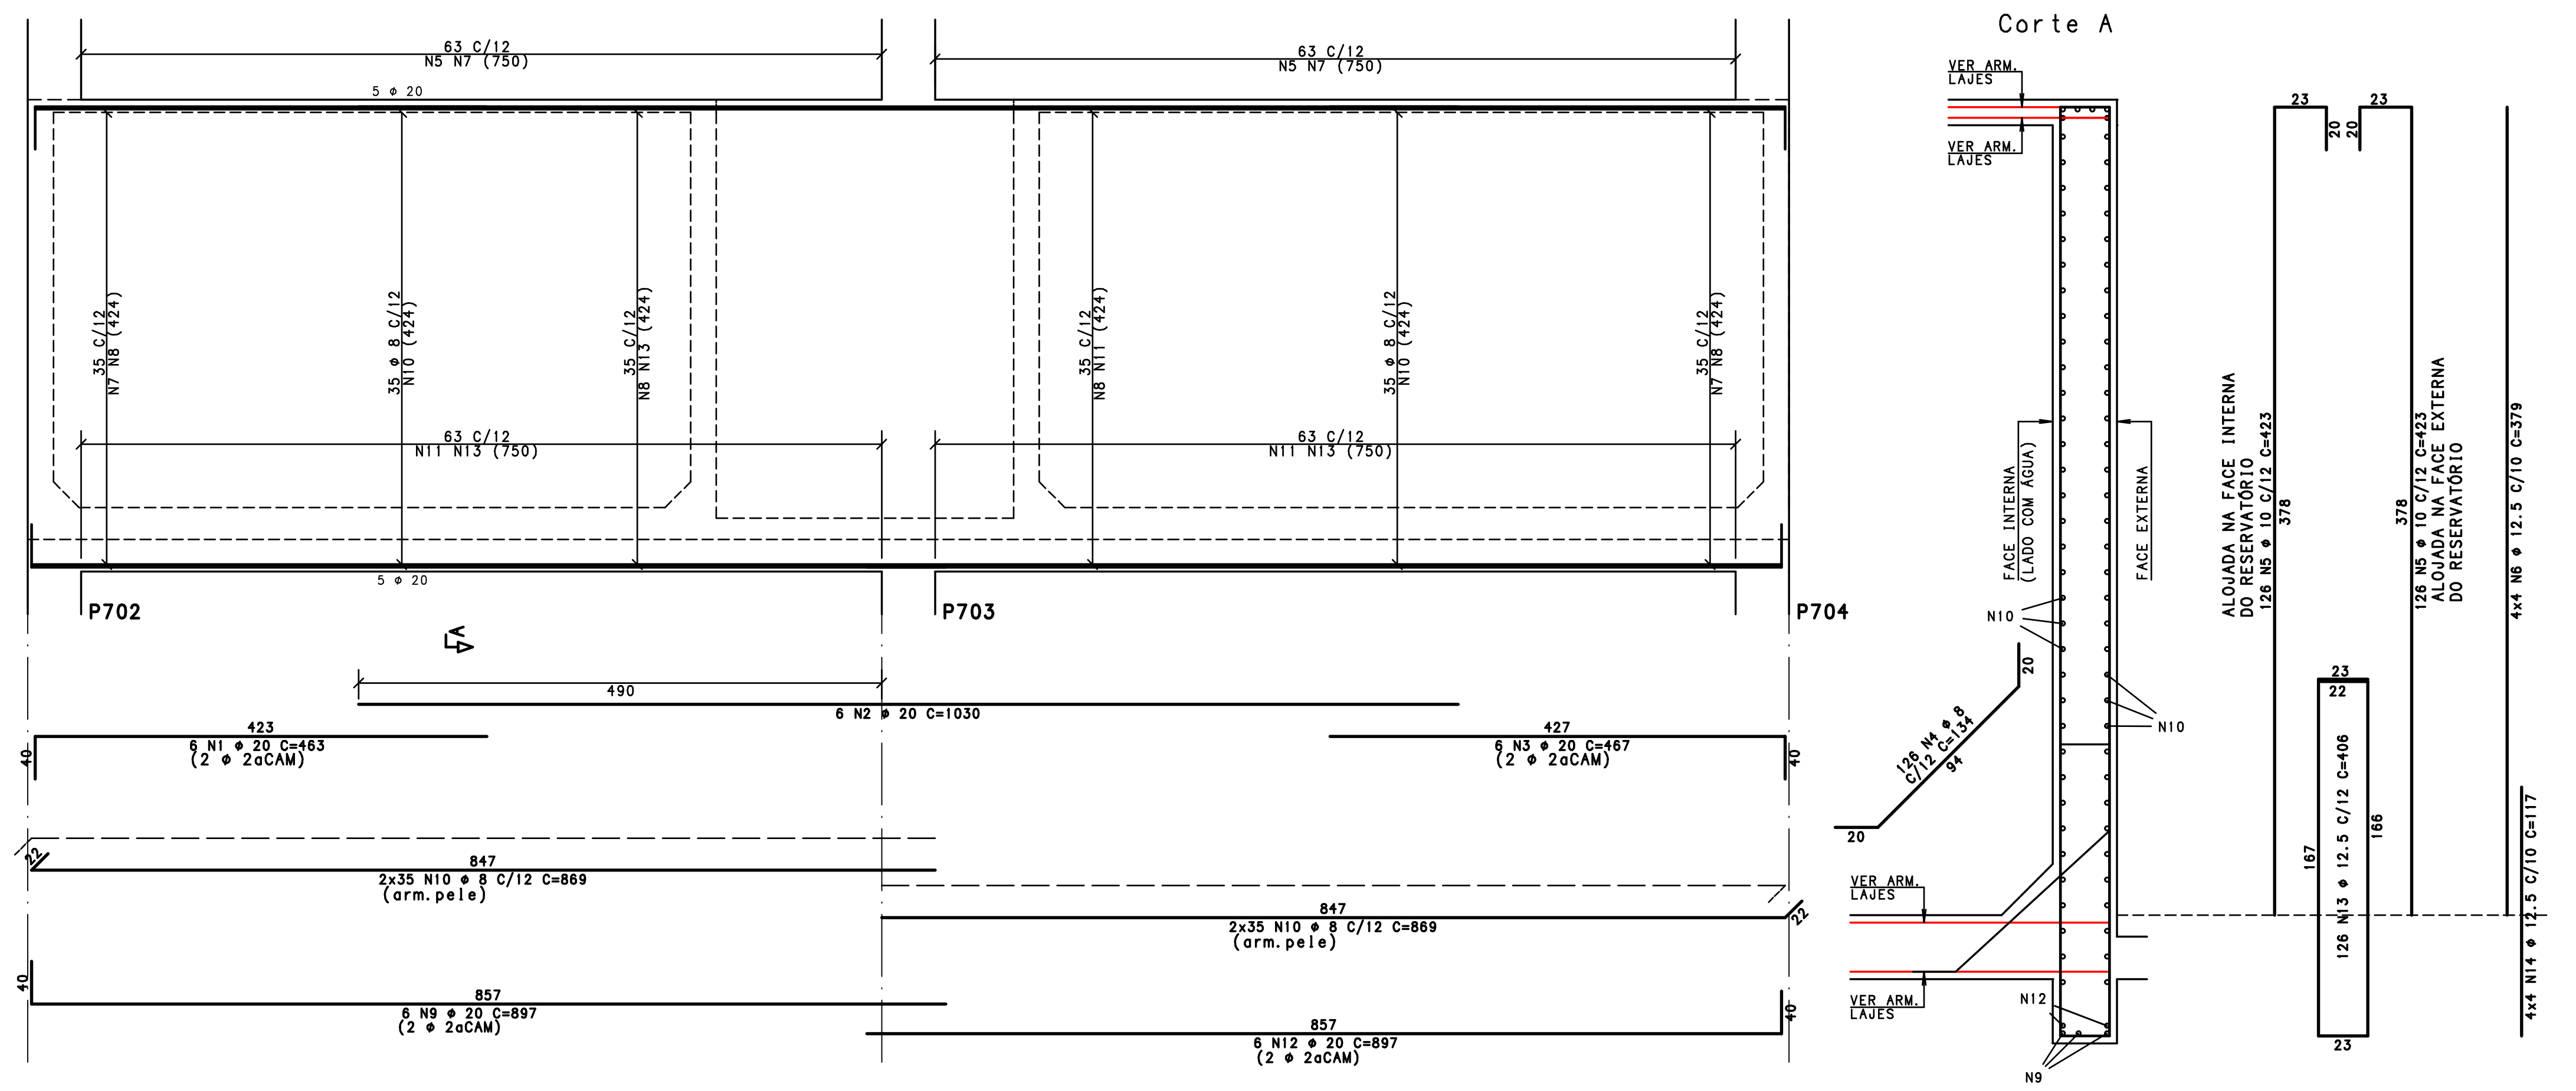
30X442
Corte A
63 C/12
N5 N7 (750)
63 C/12
N5 N7 (750)
5 ⌀ 20
N11 N13 (750)
P702
P703
P704
VER ARM. LAJES
FACE INTERNA (LADO COM ÁGUA)
FACE EXTERNA
ALOJADA NA FACE INTERNA DO RESERVATÓRIO
ALOJADA NA FACE EXTERNA DO RESERVATÓRIO
6 N2 ⌀ 20 C=1030
6 N1 ⌀ 20 C=463 (2 ⌀ 2oCAM)
6 N3 ⌀ 20 C=467 (2 ⌀ 2oCAM)
2x35 N10 ⌀ 8 C/12 C=869 (arm.pele)
6 N9 ⌀ 20 C=897 (2 ⌀ 2oCAM)
6 N12 ⌀ 20 C=897 (2 ⌀ 2oCAM)
N10
N12
N9
4x4 N14 ⌀ 12.5 C/10 C=117
126 N13 ⌀ 12.5 C/12 C=406

ARM.DAS MÍSULAS VERTICAIS
ESCALA 1:25
Planta

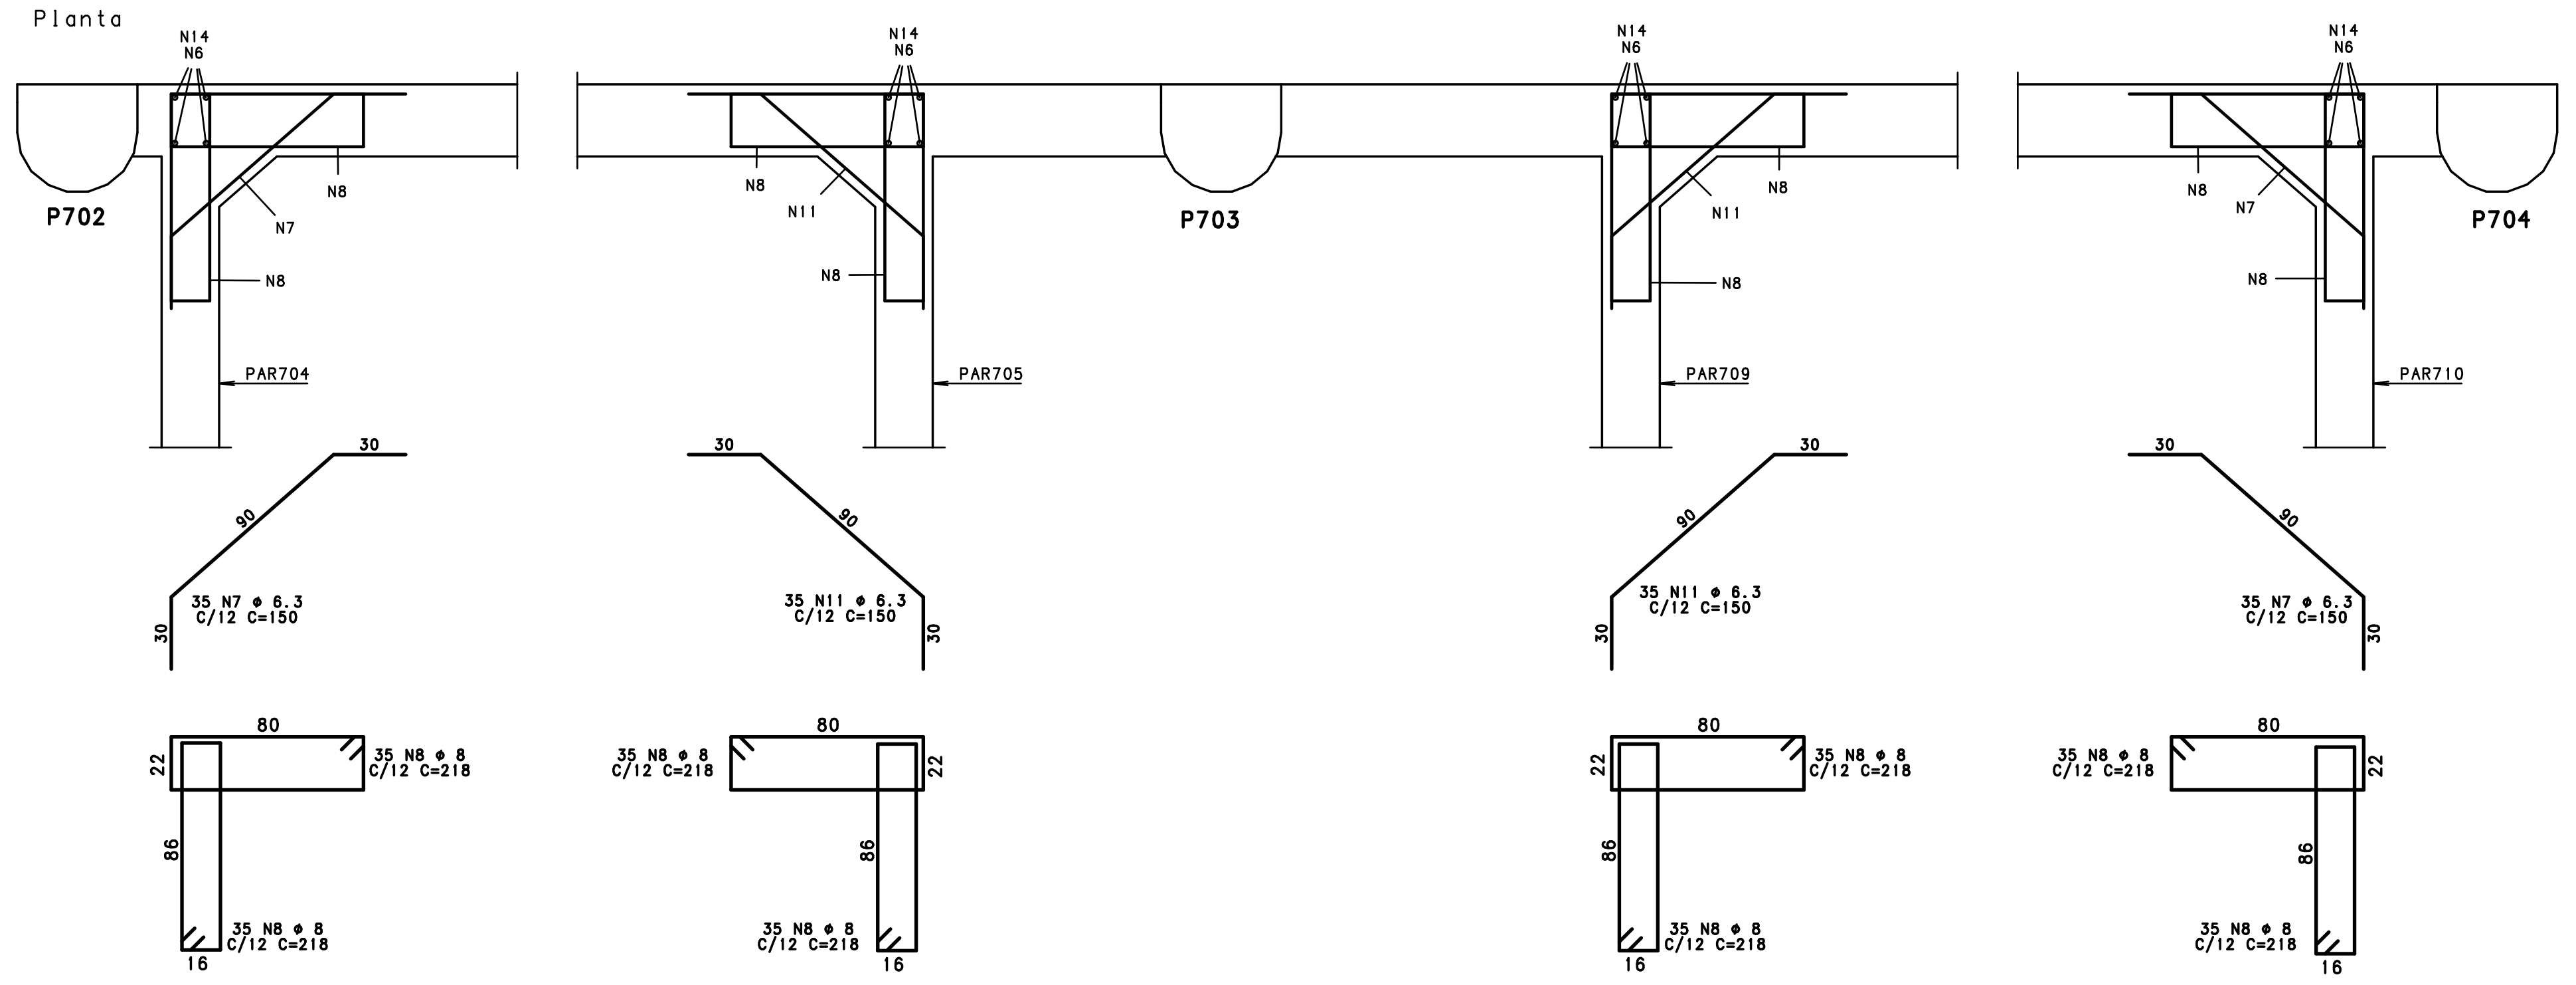

PAR702

24X412

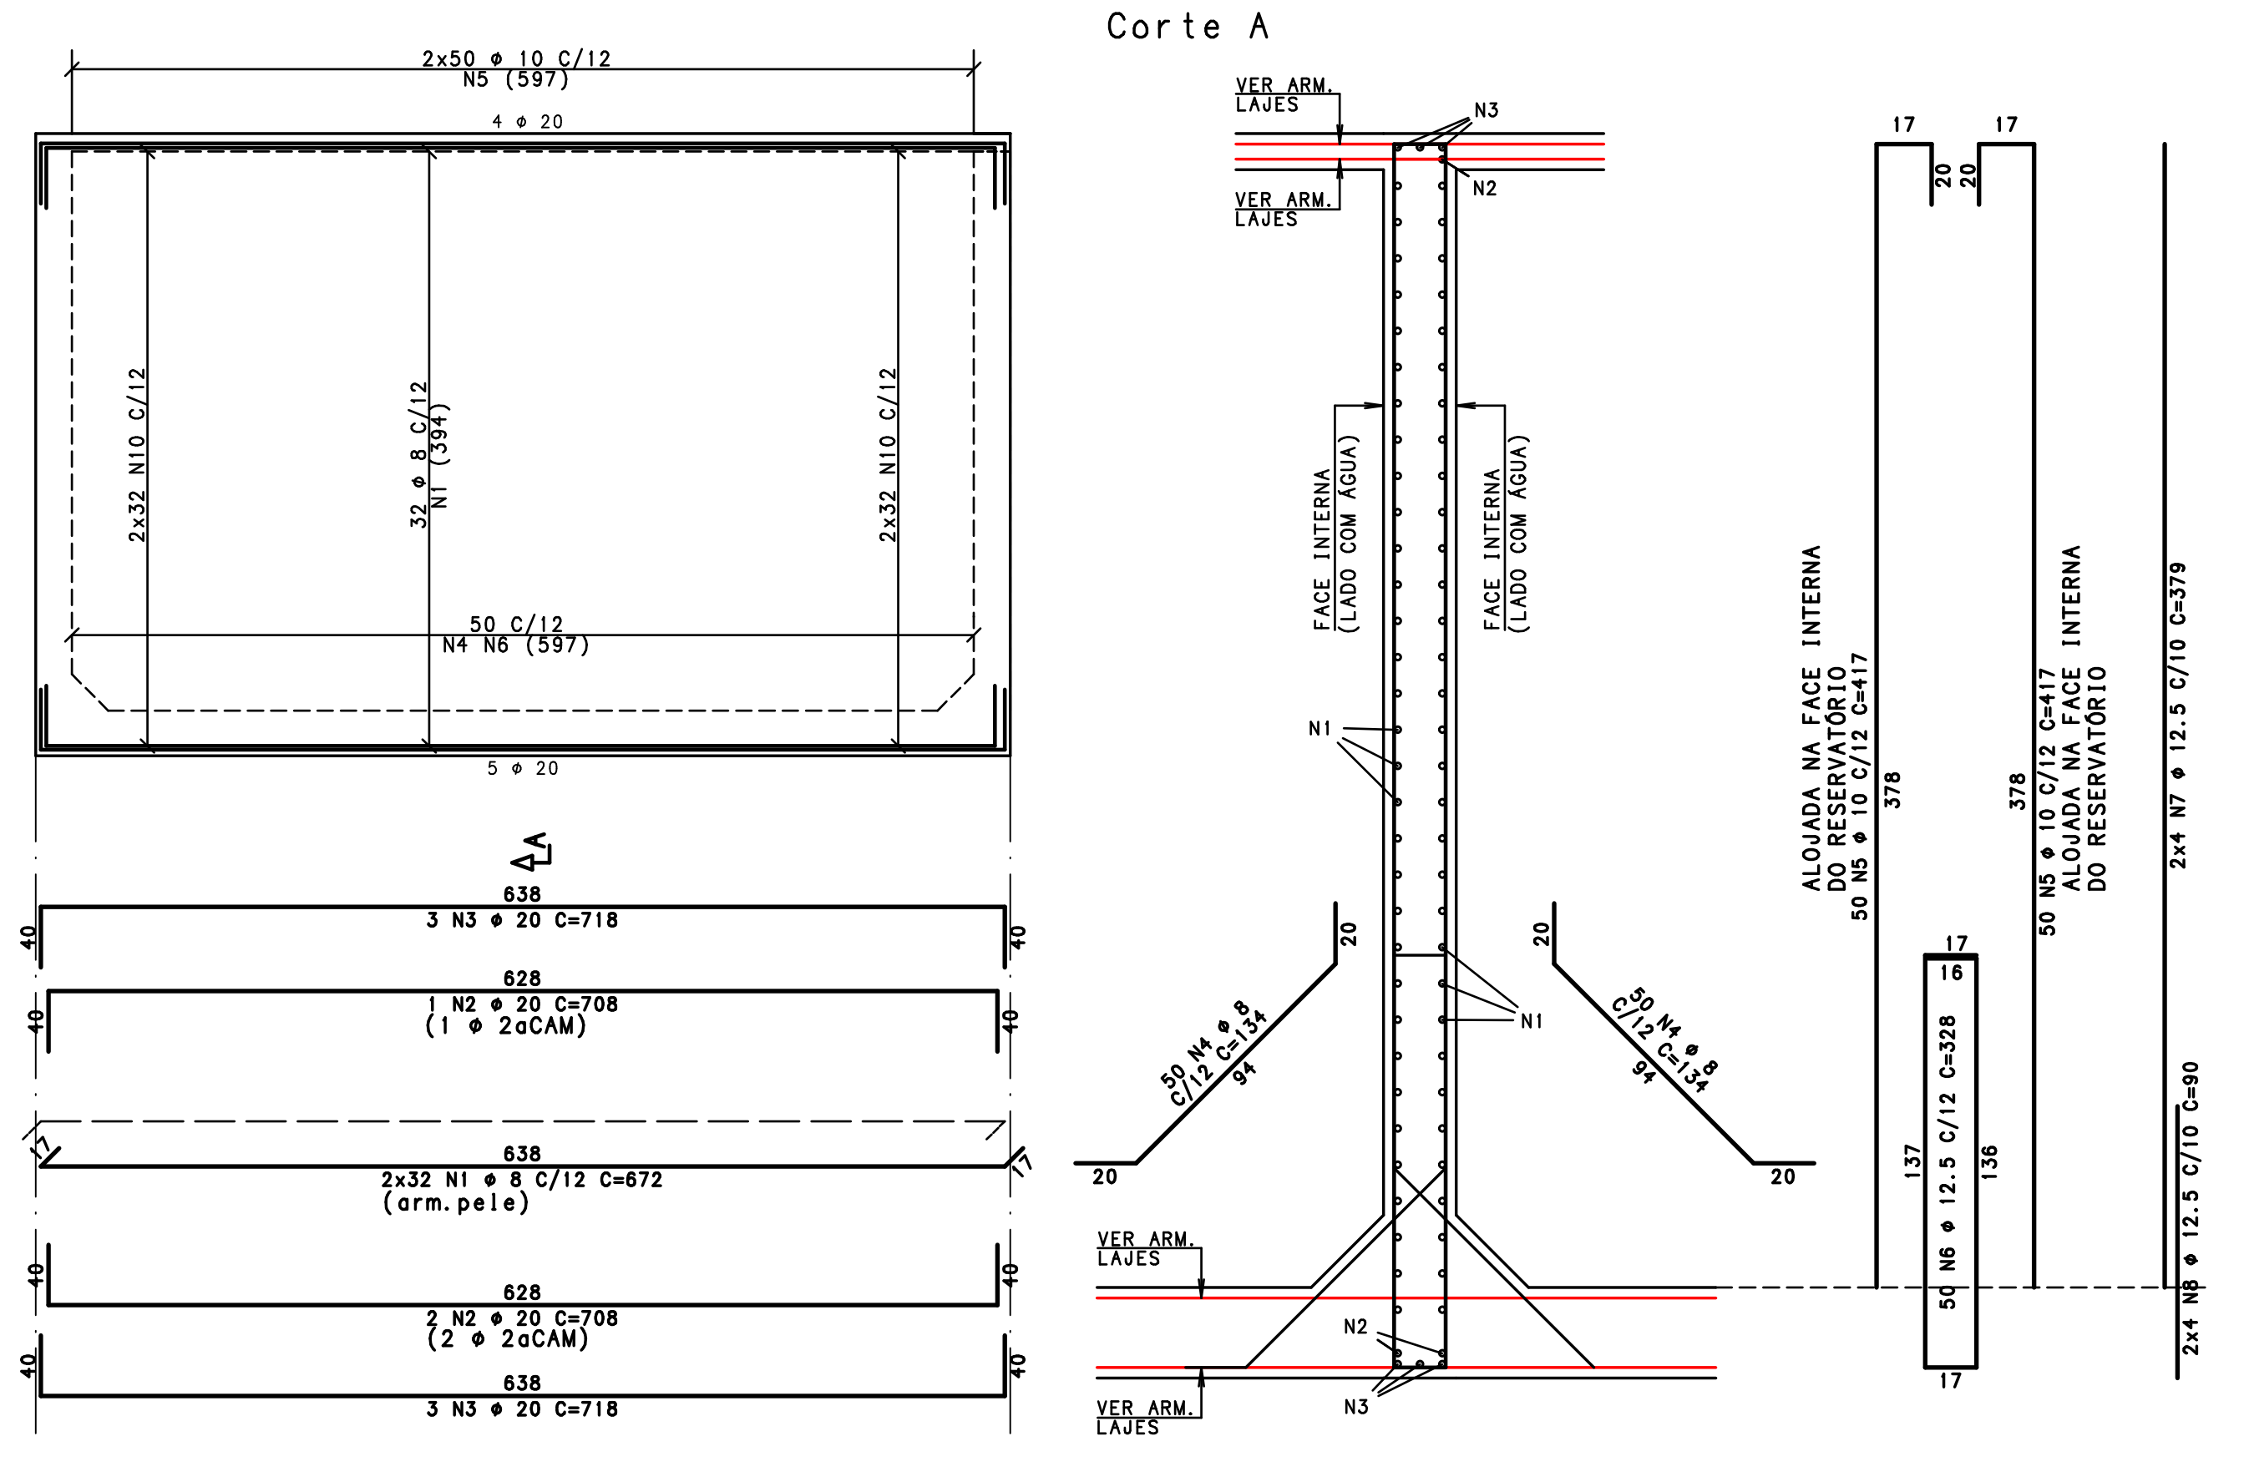

ARM.DAS MÍSULAS VERTICAIS
ESCALA 1:25
Planta

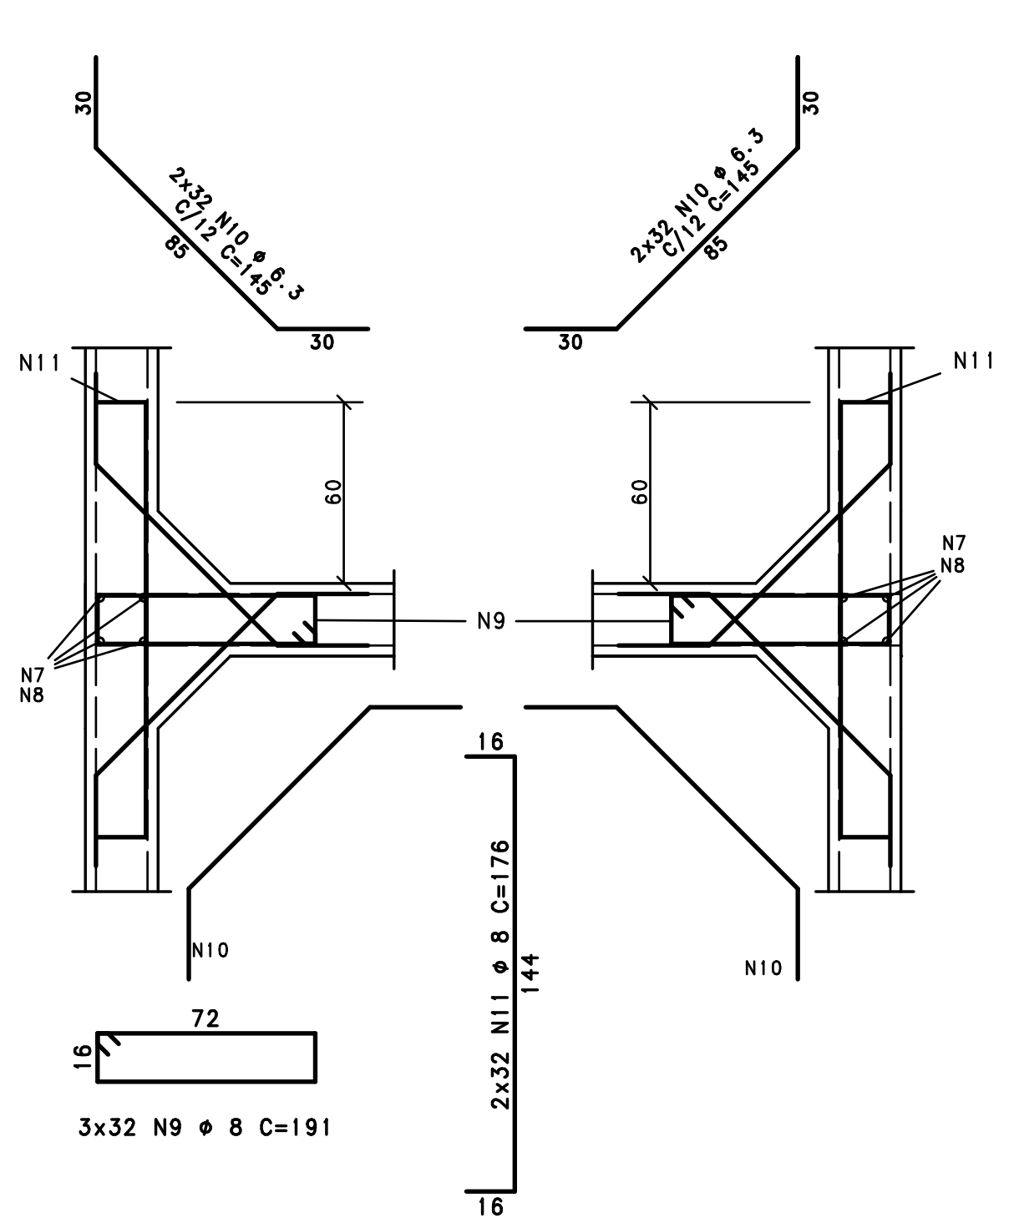

PAR703

24X412

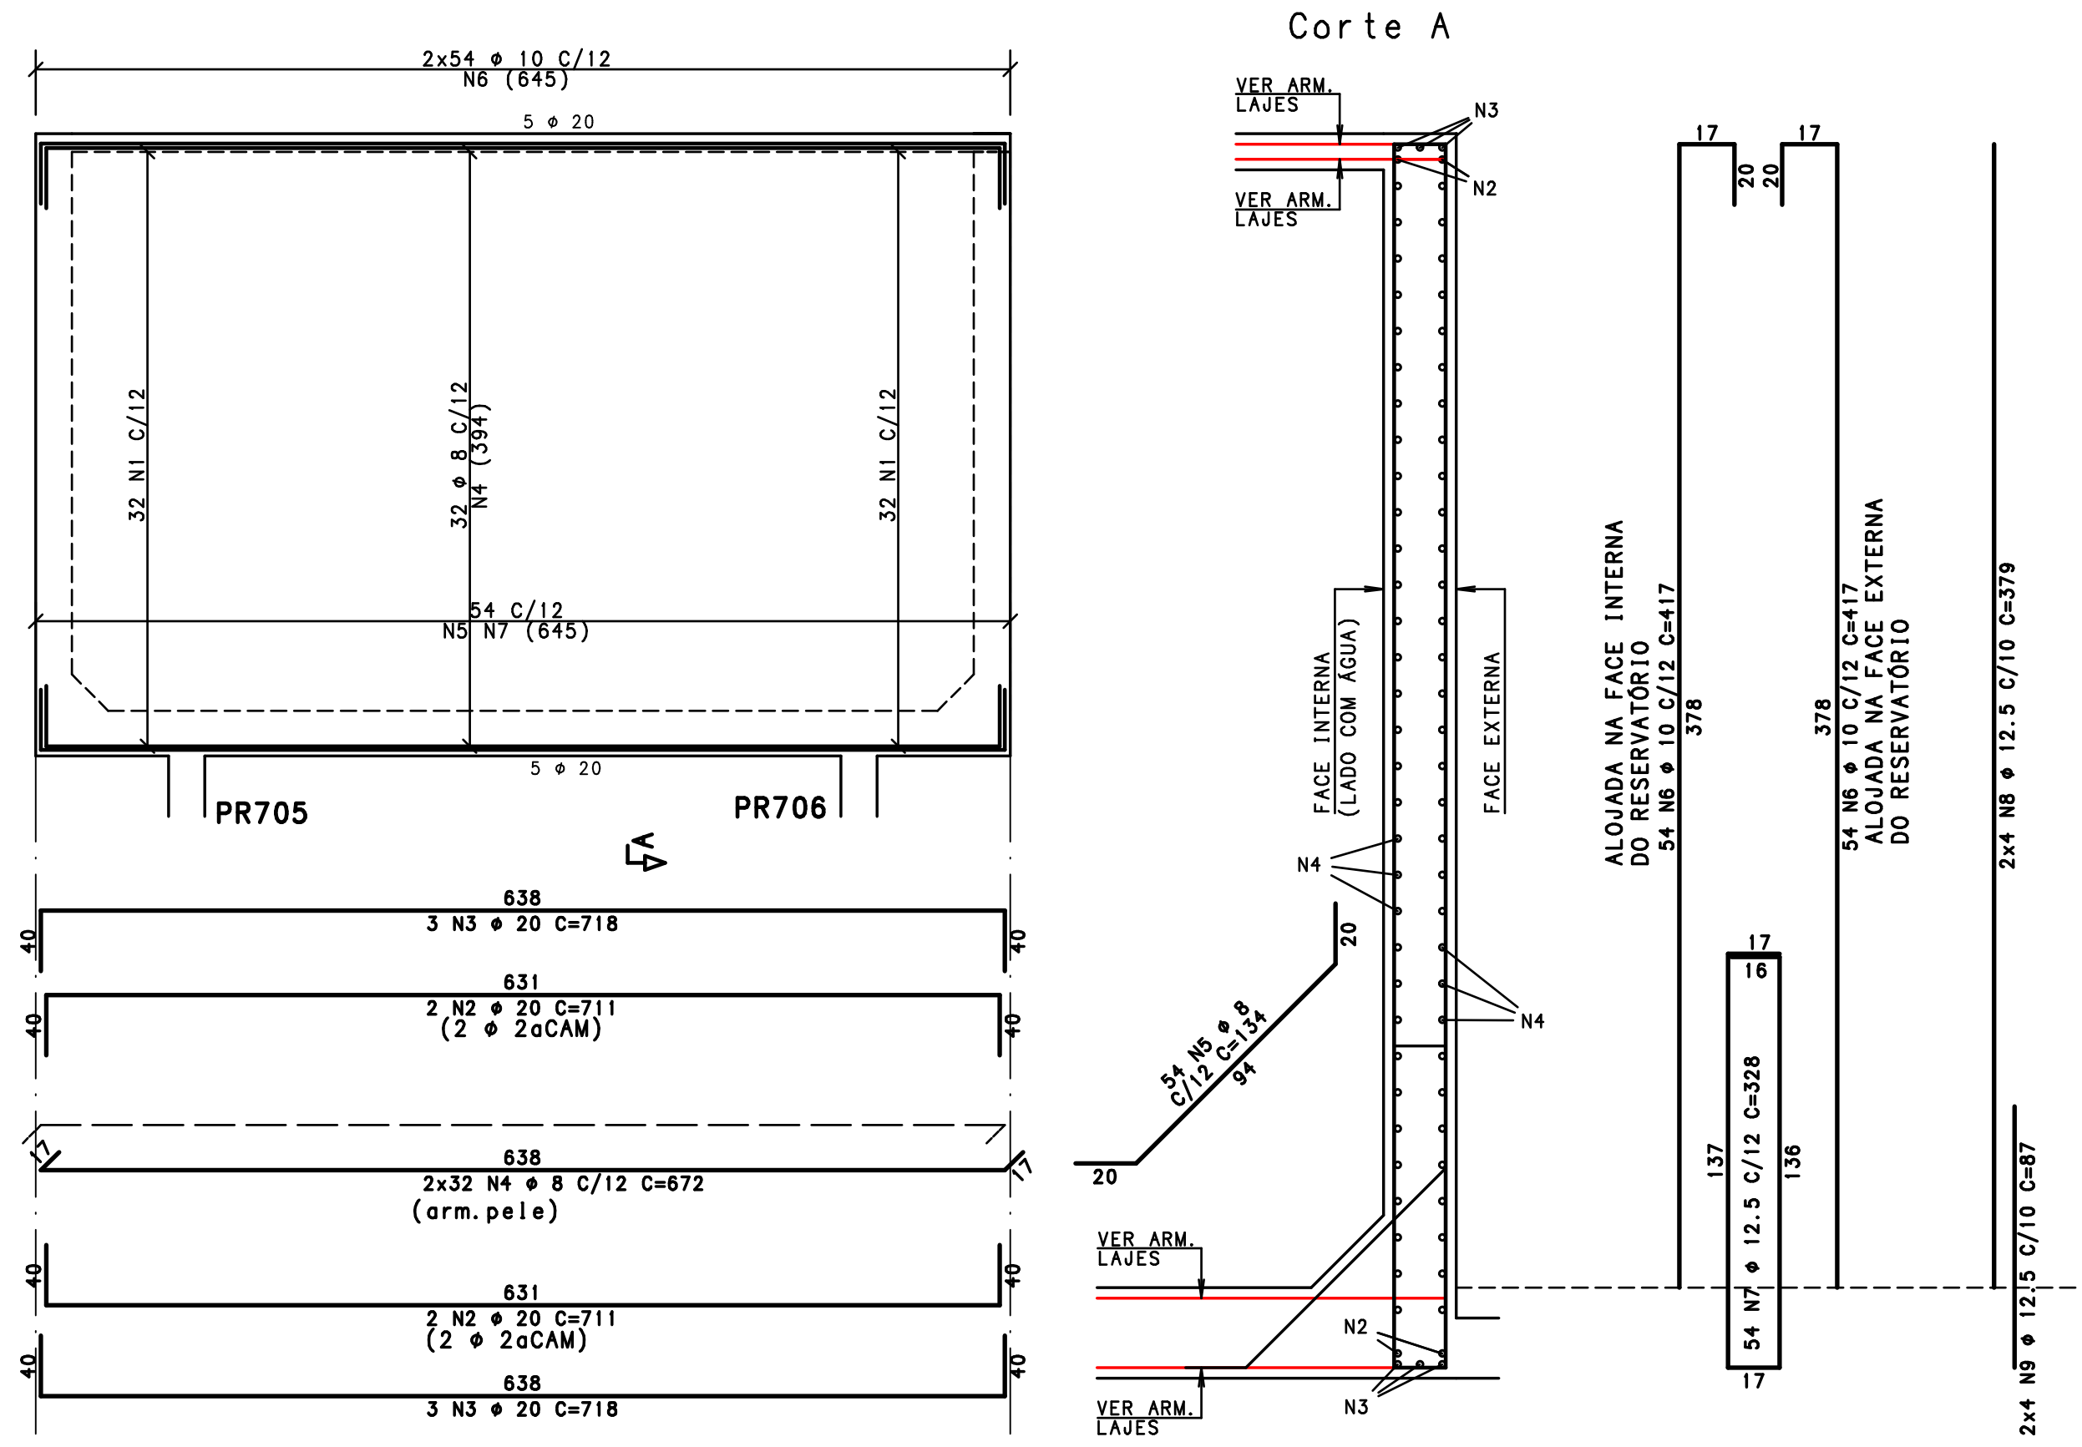

ARM.DAS MÍSULAS VERTICAIS
ESCALA 1:25
Planta

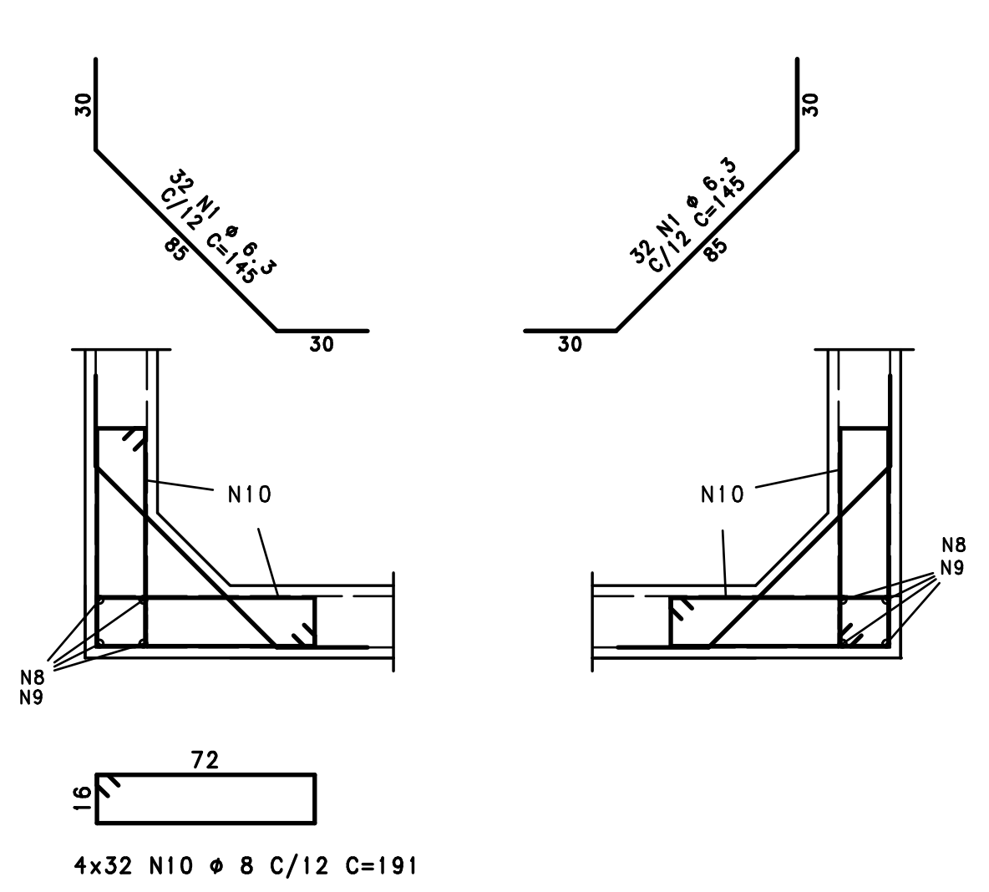

PAR704=PAR705=PAR709=PAR710

24X412

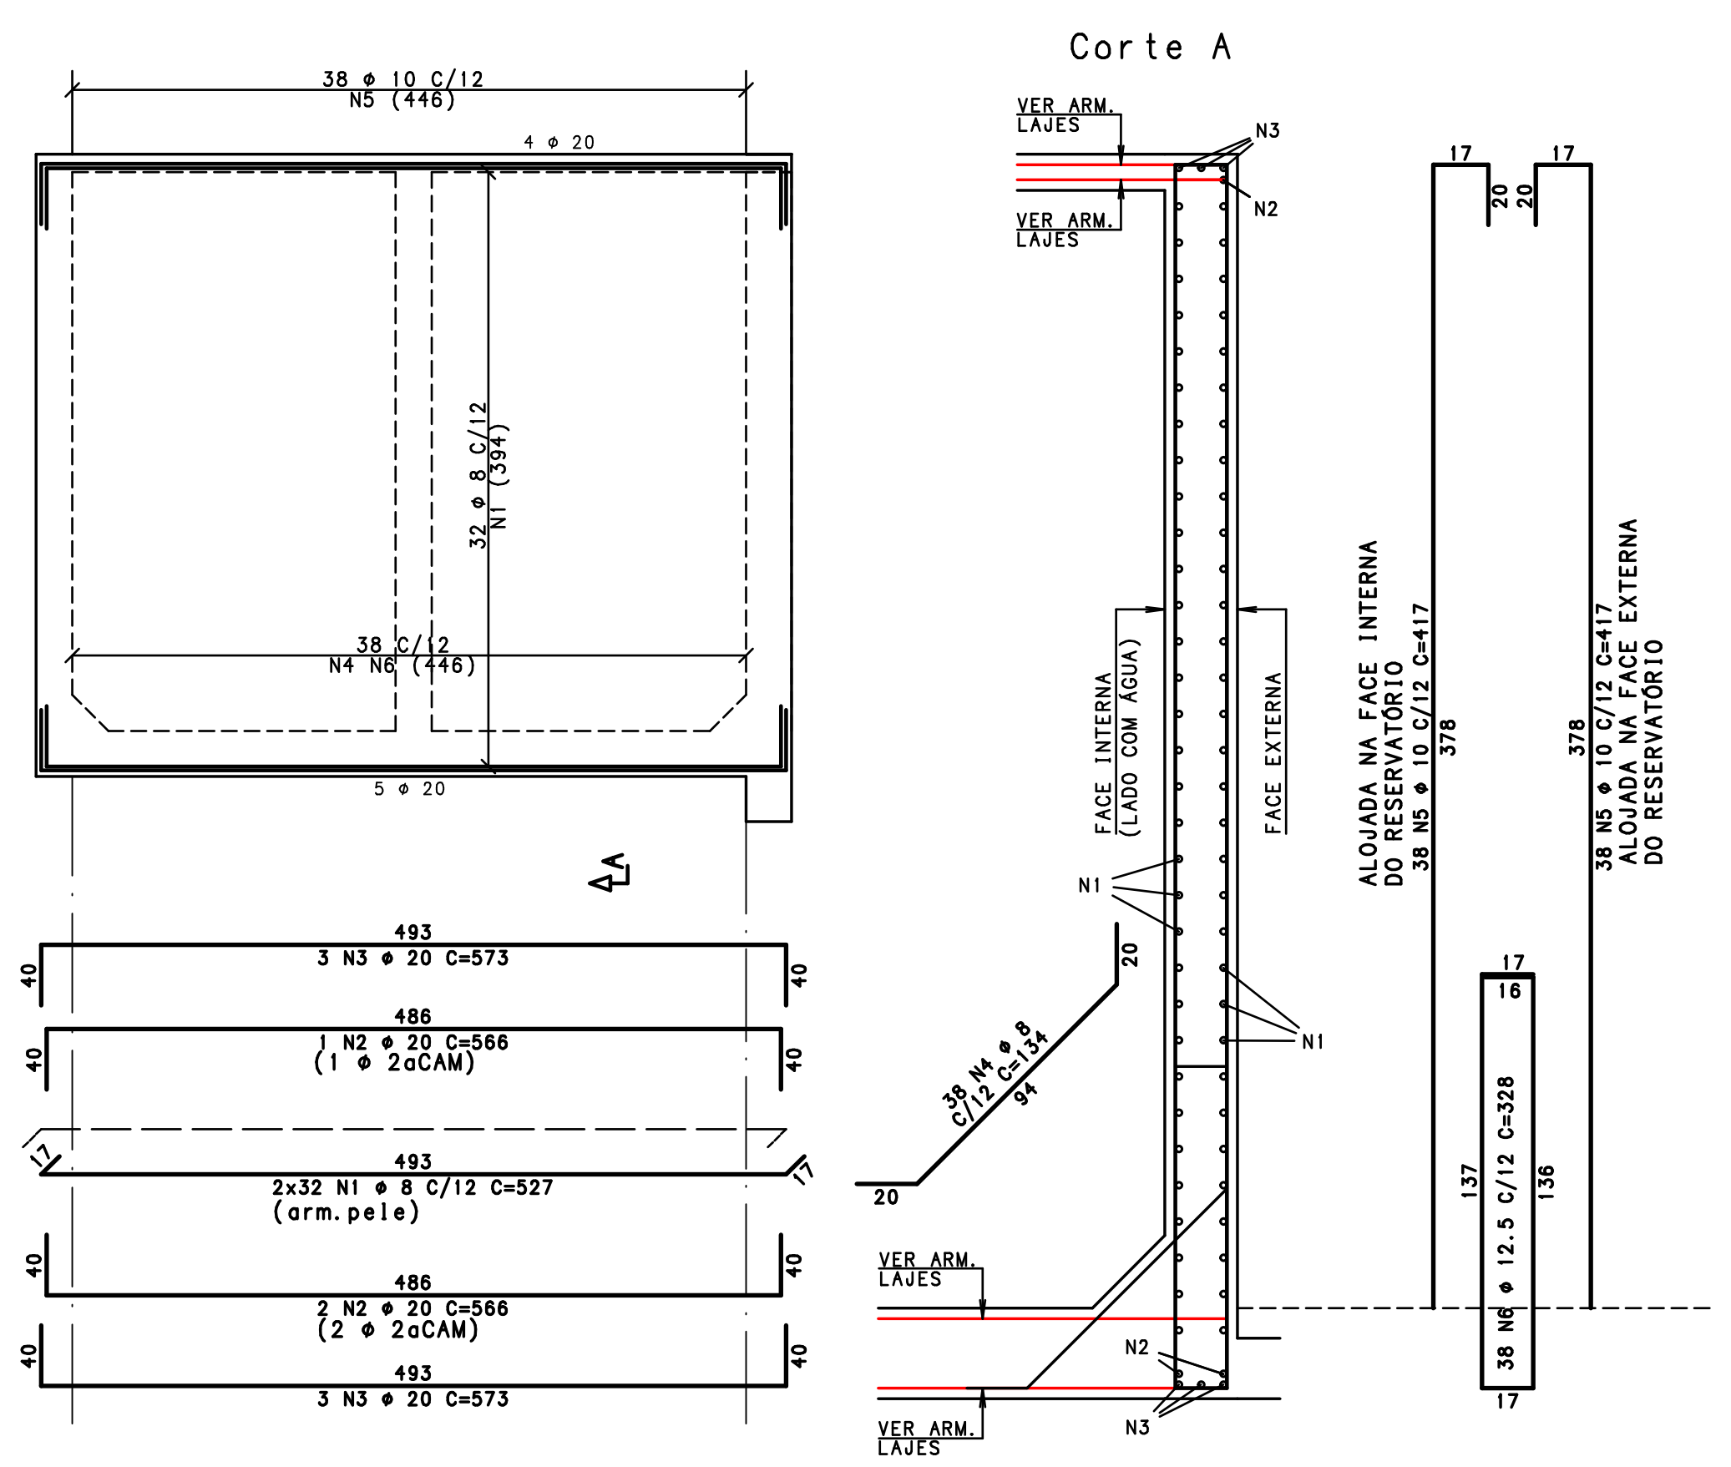
Corte A
38 ⌀ 10 C/12
N5 (446)
4 ⌀ 20
32 ⌀ 8 C/12 N1 (594)
38 C/12
N4 N6 (446)
5 ⌀ 20
3 N3 ⌀ 20 C=573
1 N2 ⌀ 20 C=566 (1 ⌀ 2oCAM)
2x32 N1 ⌀ 8 C/12 C=527 (arm.pele)
2 N2 ⌀ 20 C=566 (2 ⌀ 2oCAM)
3 N3 ⌀ 20 C=573
VER ARM. LAJES
FACE INTERNA (LADO COM ÁGUA)
FACE EXTERNA
ALOJADA NA FACE INTERNA DO RESERVATÓRIO
ALOJADA NA FACE EXTERNA DO RESERVATÓRIO
38 N5 ⌀ 10 C/12 C=417
38 N6 ⌀ 12.5 C/12 C=328
38 N4 ⌀ 8

PAR707

24X412

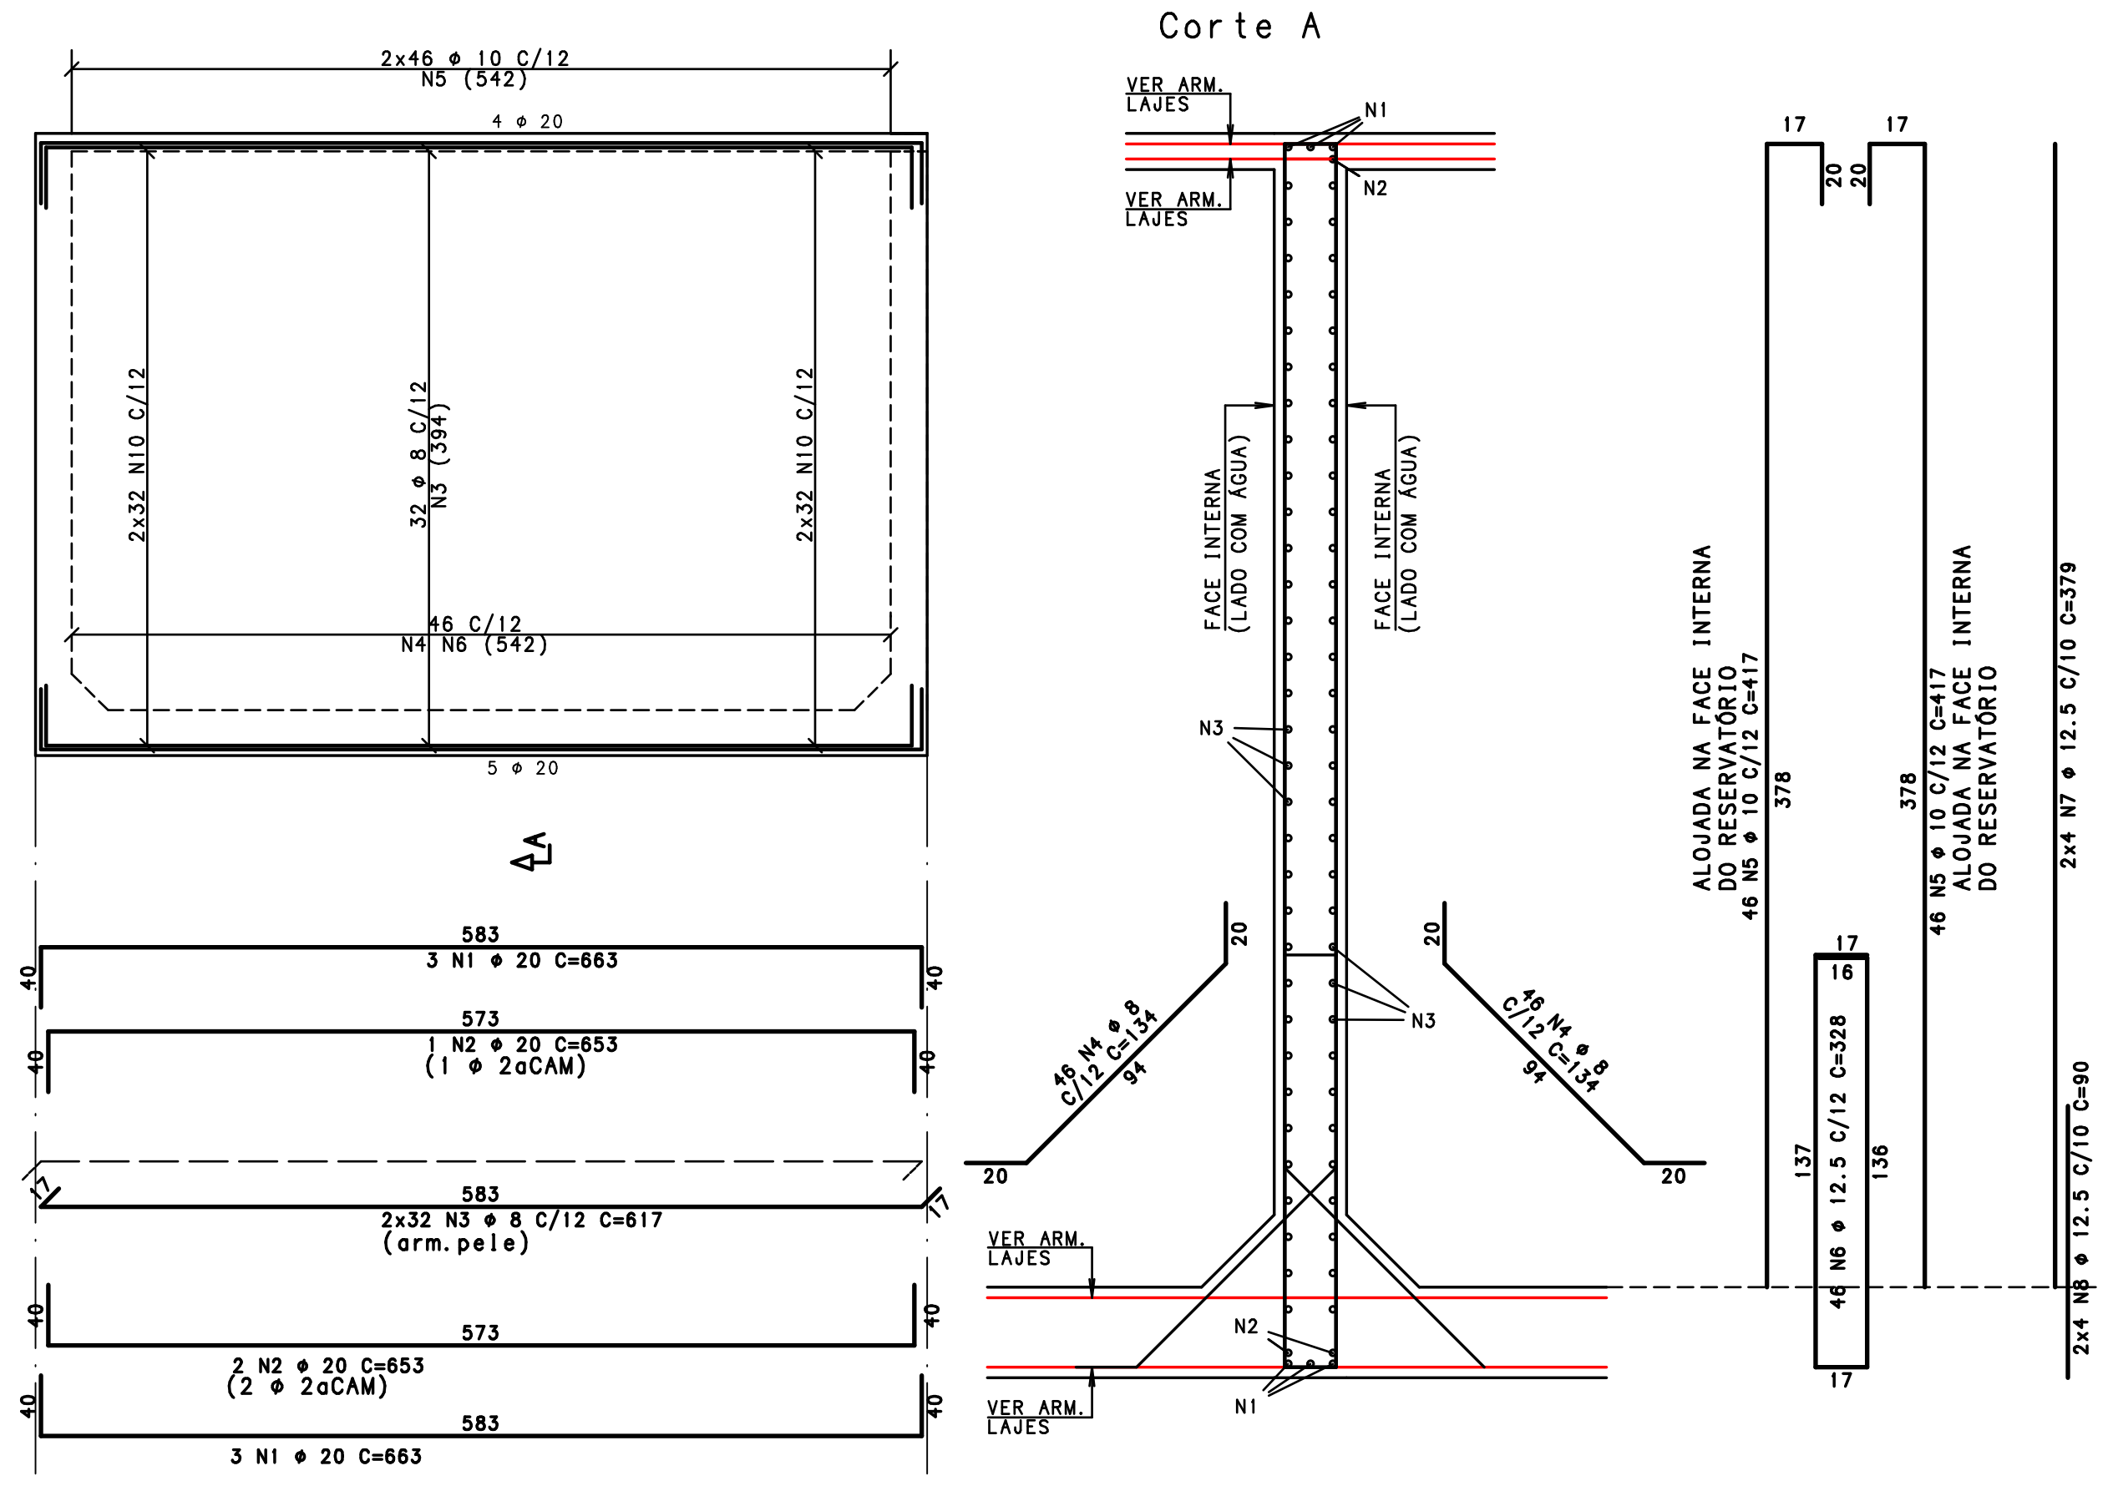

ARM.DAS MÍSULAS VERTICAIS
ESCALA 1:25
Planta

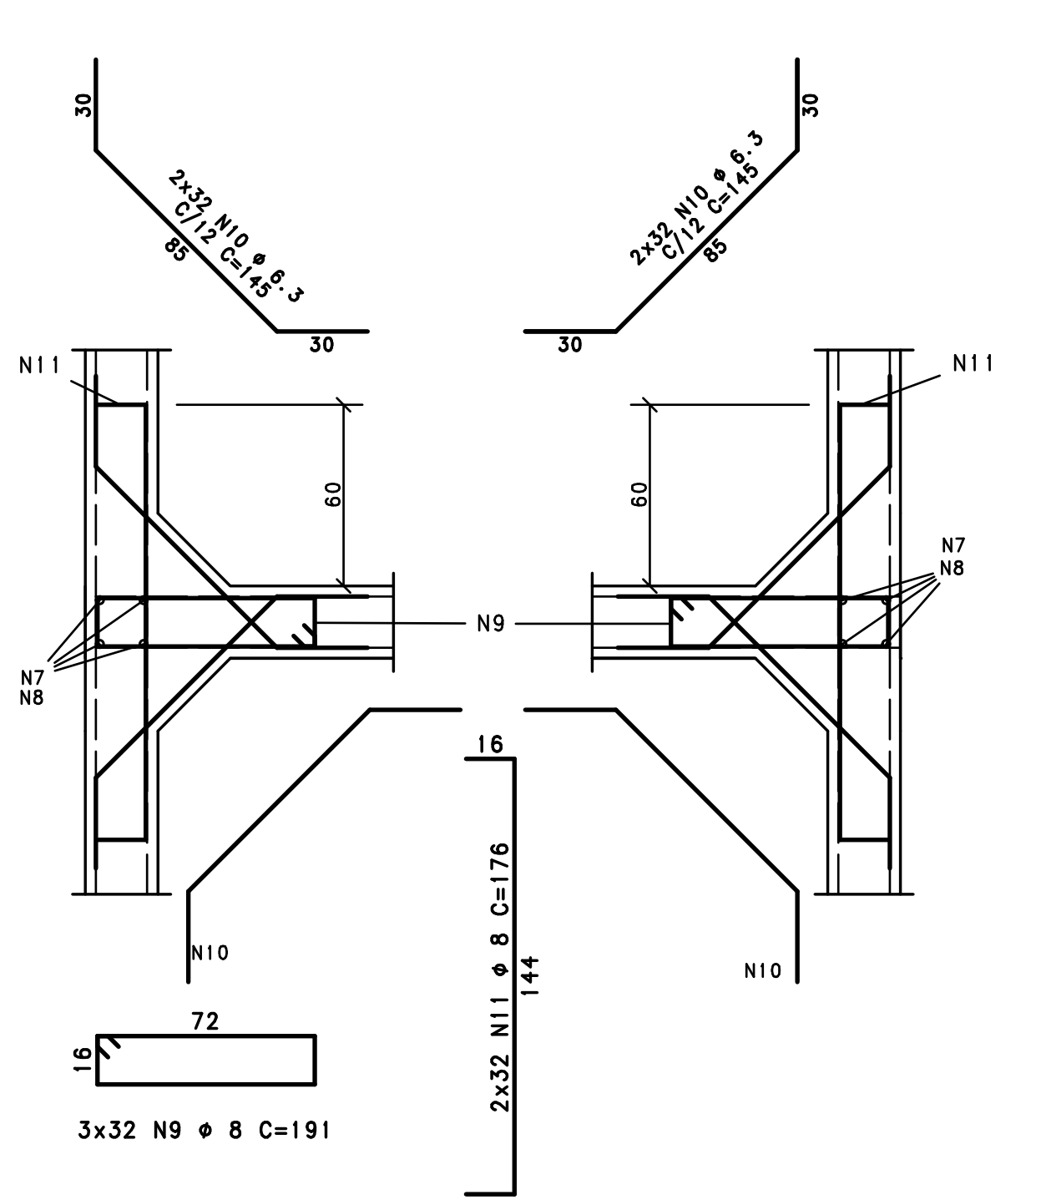

PAR708

24X412

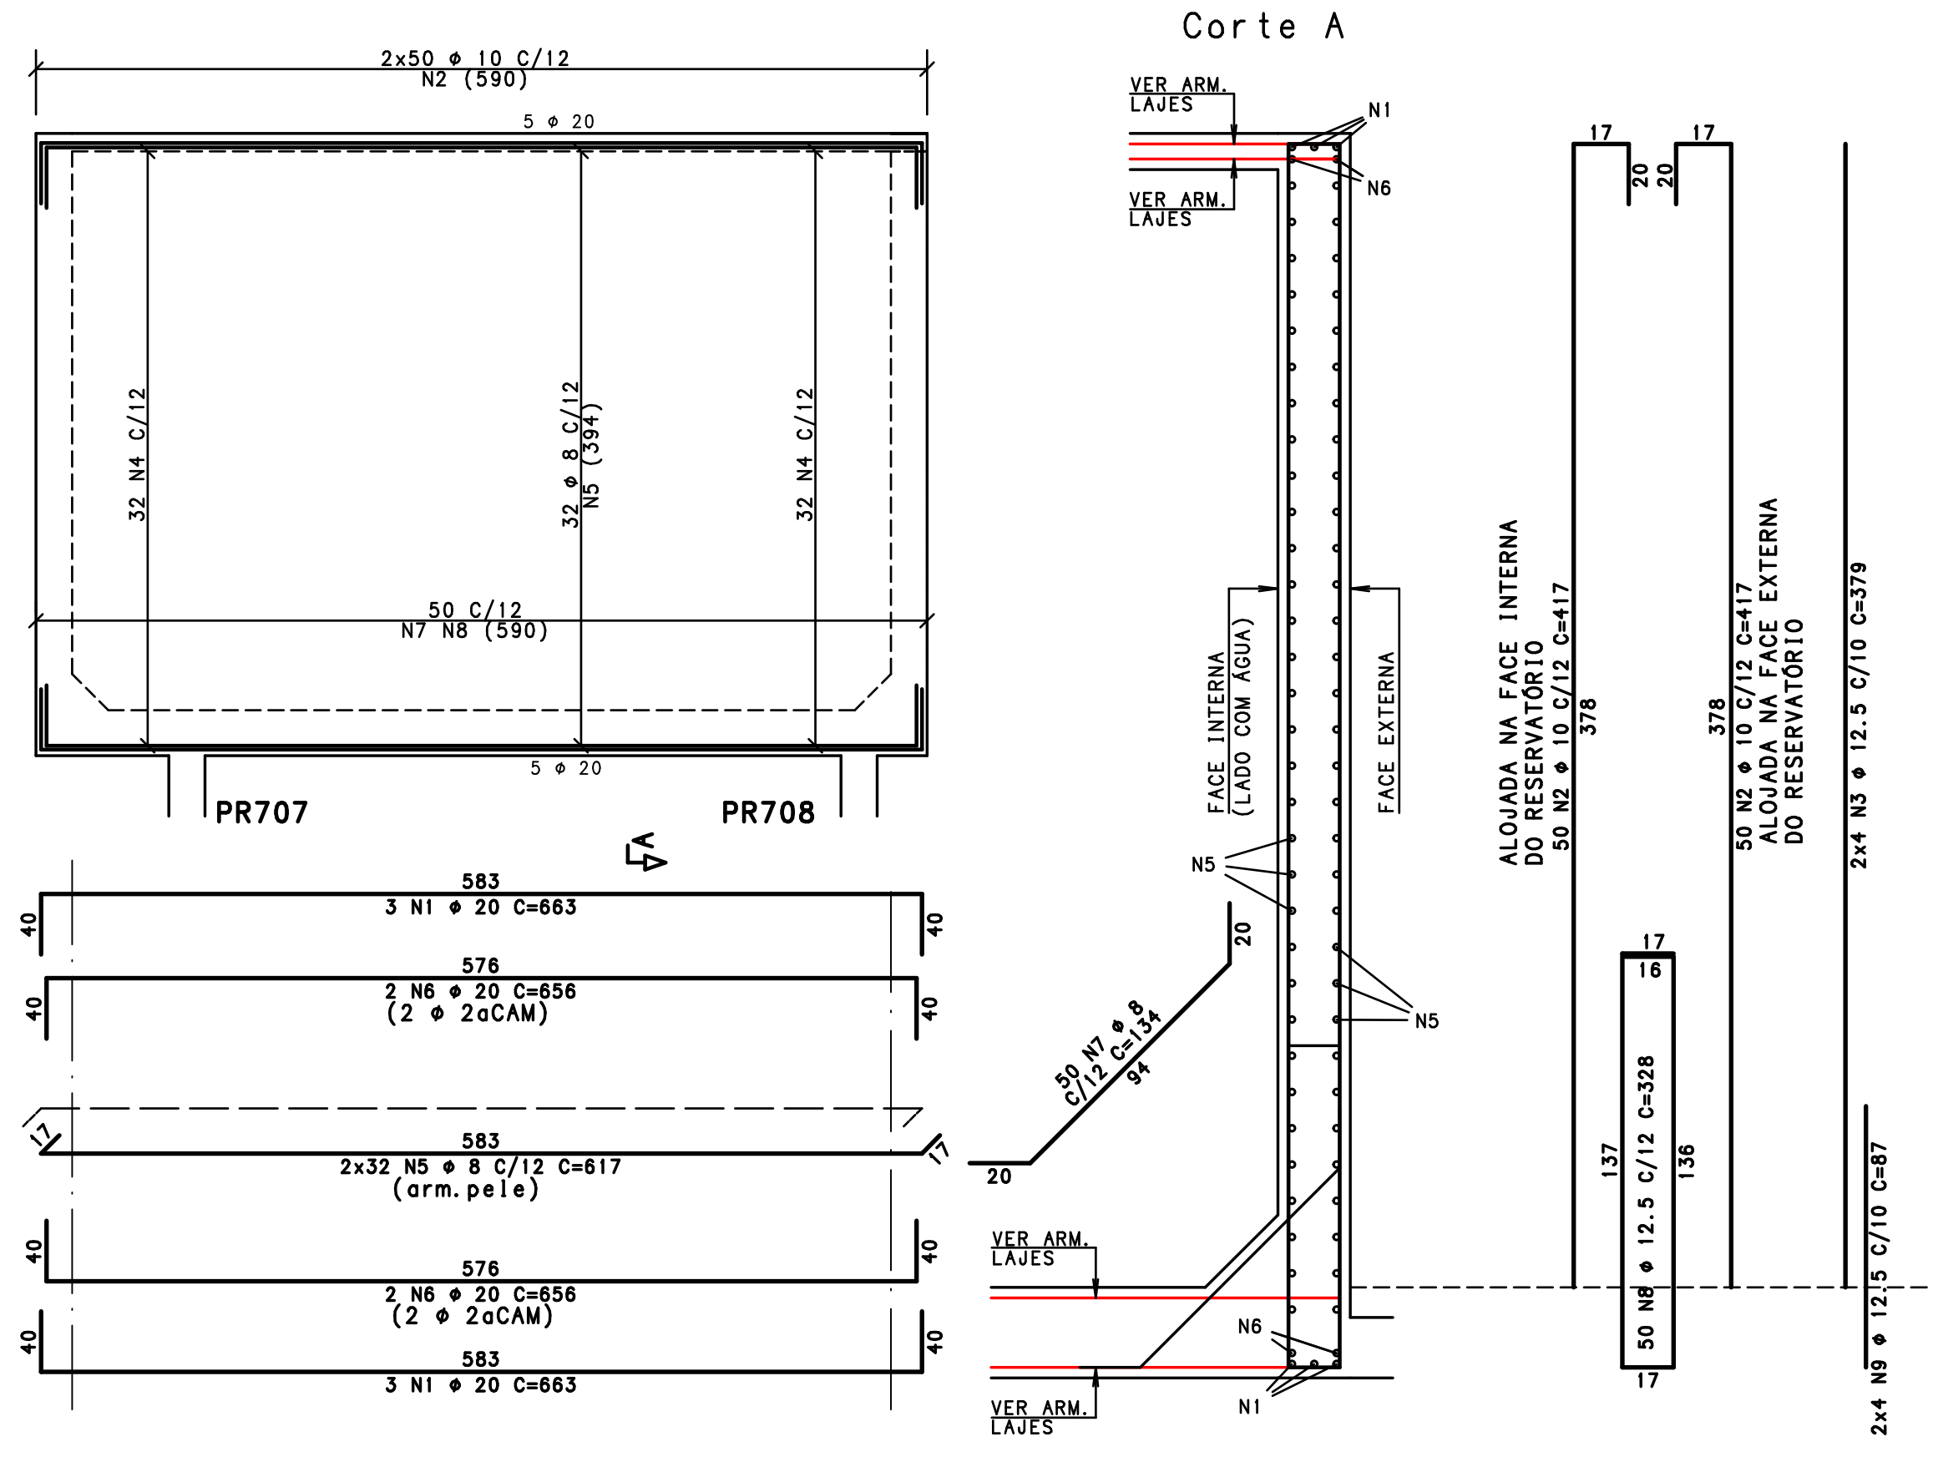

ARM.DAS MÍSULAS VERTICAIS
ESCALA 1:25
Planta

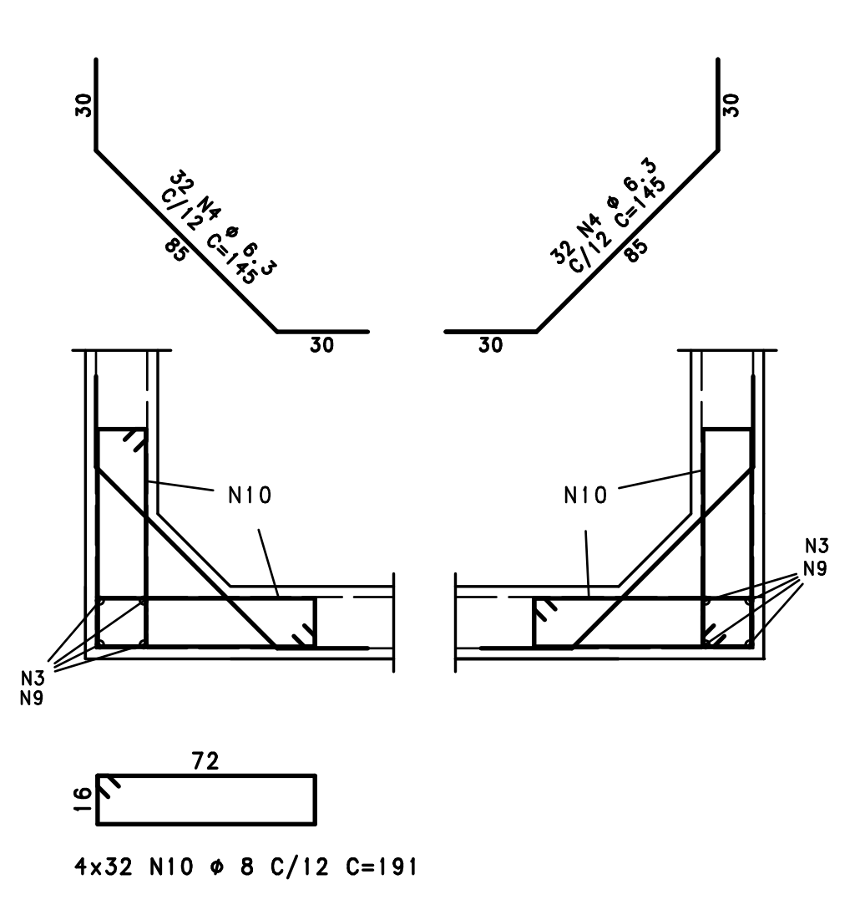

	AÇO	POS	QUANT	BIT (mm)	COMPRIMENTO UNIT (cm)	COMPRIMENTO TOTAL (cm)
PAR701						
	50A	1	6	20	463	2778
	50A	2	6	20	1030	6180
	50A	3	6	20	467	2802
	50A	4	126	8	134	16884
	50A	5	252	10	423	106596
	50A	6	16	12.5	379	6064
	50A	7	70	6.3	150	10500
	50A	8	280	8	218	61040
	50A	9	6	20	897	5382
	50A	10	140	8	869	121660
	50A	11	70	6.3	150	10500
	50A	12	6	20	897	5382
	50A	13	126	12.5	406	51156
	50A	14	16	12.5	117	1872
PAR702						
	50A	1	64	8	672	43008
	50A	2	3	20	708	2124
	50A	3	6	20	718	4308
	50A	4	100	8	134	13400
	50A	5	100	10	417	41700
	50A	6	50	12.5	328	16400
	50A	7	8	12.5	379	3032
	50A	8	8	12.5	90	720
	50A	9	96	8	191	18336
	50A	10	128	6.3	145	18560
	50A	11	64	8	176	11264

	AÇO	POS	QUANT	BIT (mm)	COMPRIMENTO UNIT (cm)	COMPRIMENTO TOTAL (cm)
PAR703						
	50A	1	64	6.3	145	9280
	50A	2	4	20	711	2844
	50A	3	6	20	718	4308
	50A	4	64	8	672	43008
	50A	5	54	8	134	7236
	50A	6	108	10	417	45036
	50A	7	54	12.5	328	17712
	50A	8	8	12.5	379	3032
	50A	9	8	12.5	87	696
	50A	10	128	8	191	24448
PAR704=PAR705=PAR709=PAR710 (X4)						
	50A	1	256	8	527	134912
	50A	2	12	20	566	6792
	50A	3	24	20	573	13752
	50A	4	152	8	134	20368
	50A	5	304	10	417	126768
	50A	6	152	12.5	328	49856
PAR707						
	50A	1	6	20	663	3978
	50A	2	3	20	653	1959
	50A	3	64	8	617	39488
	50A	4	92	8	134	12328
	50A	5	92	10	417	38364
	50A	6	46	12.5	328	15088
	50A	7	8	12.5	379	3032
	50A	8	8	12.5	90	720
	50A	9	96	8	191	18336
	50A	10	128	6.3	145	18560
	50A	11	64	8	176	11264
PAR708						
	50A	1	6	20	663	3978
	50A	2	100	10	417	41700
	50A	3	8	12.5	379	3032
	50A	4	64	6.3	145	9280
	50A	5	64	8	617	39488
	50A	6	4	20	656	2624
	50A	7	50	8	134	6700
	50A	8	50	12.5	328	16400
	50A	9	8	12.5	87	696
	50A	10	128	8	191	24448

RESUMO TOTAL AÇO CA 50-60

AÇO	BIT (mm)	COMPR (m)	PESO (kg)
50A	6.3	767	188
50A	8	6676	2637
50A	10	4002	2469
50A	12.5	1895	1825
50A	20	692	1706
Peso Total		50A =	8825 kgf

REV.	DATA	ALTERAÇÃO	VISTO
00	17/07/26	EMISSÃO INICIAL	FLP

PROCALK
ESTRUTURAS

RESP. TÉCNICOS
Eng. Edemir C. Simonato
CREA-RS 63038
Eng. Carlos R.M. Morais
CREA-RS 74695

Rua João Abbott, 473/401
Porto Alegre - CEP 90460-150
F. (51)3013.3200
procalk@procalk.com.br
www.procalk.com.br

Obra WERT PORTO BELO RESIDENCES
PORTO BELO - SC
Assunto VIGAS - MULTI 02 - SETOR 7
TÉRREO
Conteúdo PAR701 / PAR702 / PAR703
PAR704=PAR705=PAR709=PAR710 / PAR707 / PAR708
Cliente WERT
Número 24-1454
Desenho 7-404/0
Identificação WPBR-EST-EX-7404-PLN-MU2-S07-TE-R00
Desenho FILIPE
Escala 1:50
fck 40/35 MPa
Data 17/07/2026

PARA PLOTAGEM UTILIZAR EXCLUSIVAMENTE O ARQUIVO PLT OU PDF.

Direitos Autorais Reservados Lei N 5194/66

130/75

PROCALK ESTRUTURAS PL 4-04-00.PLT 17/07/2026 14:52:36