TAMPA DOS RESERVATÓRIOS
ESCALA 1:75

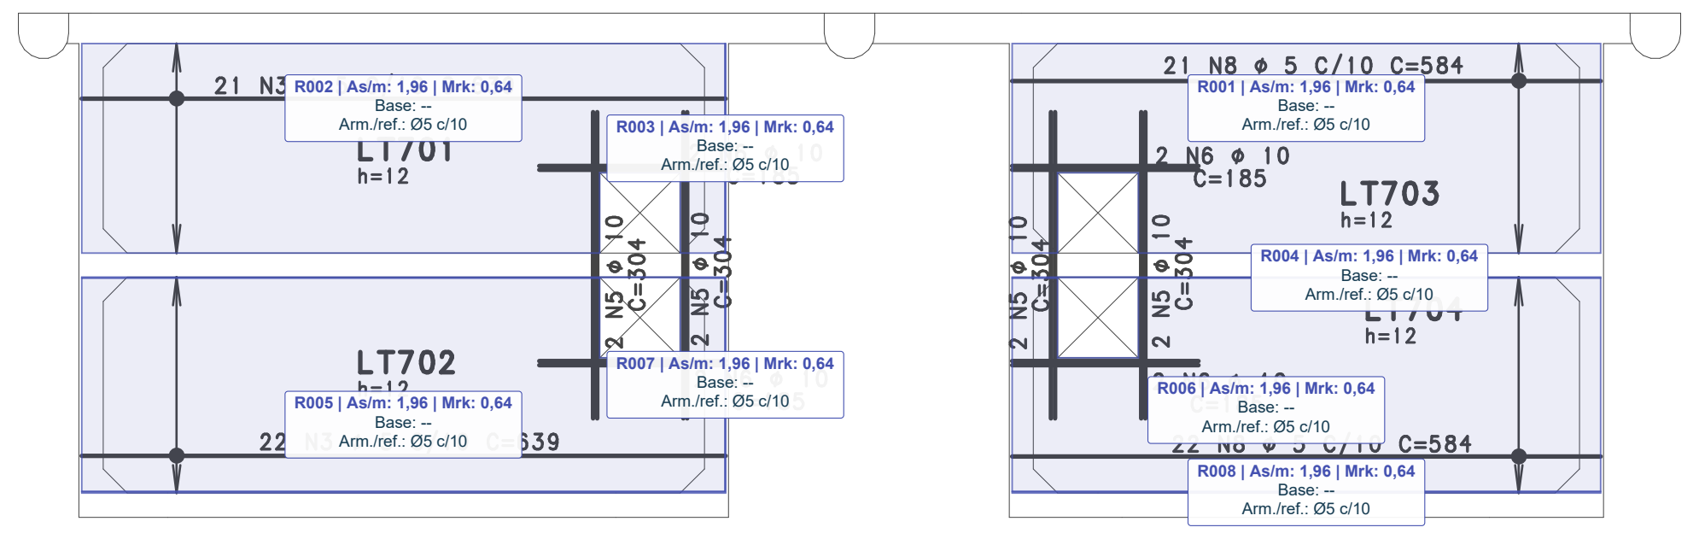

DETALHE CORTE DE BARRAS
SEM ESCALA

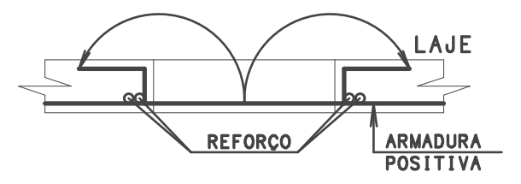

- CORTAR A ARMADURA DA LAJE NO EIXO DO FURO E DOBRAR AS PONTAS CONFORME DETALHE.

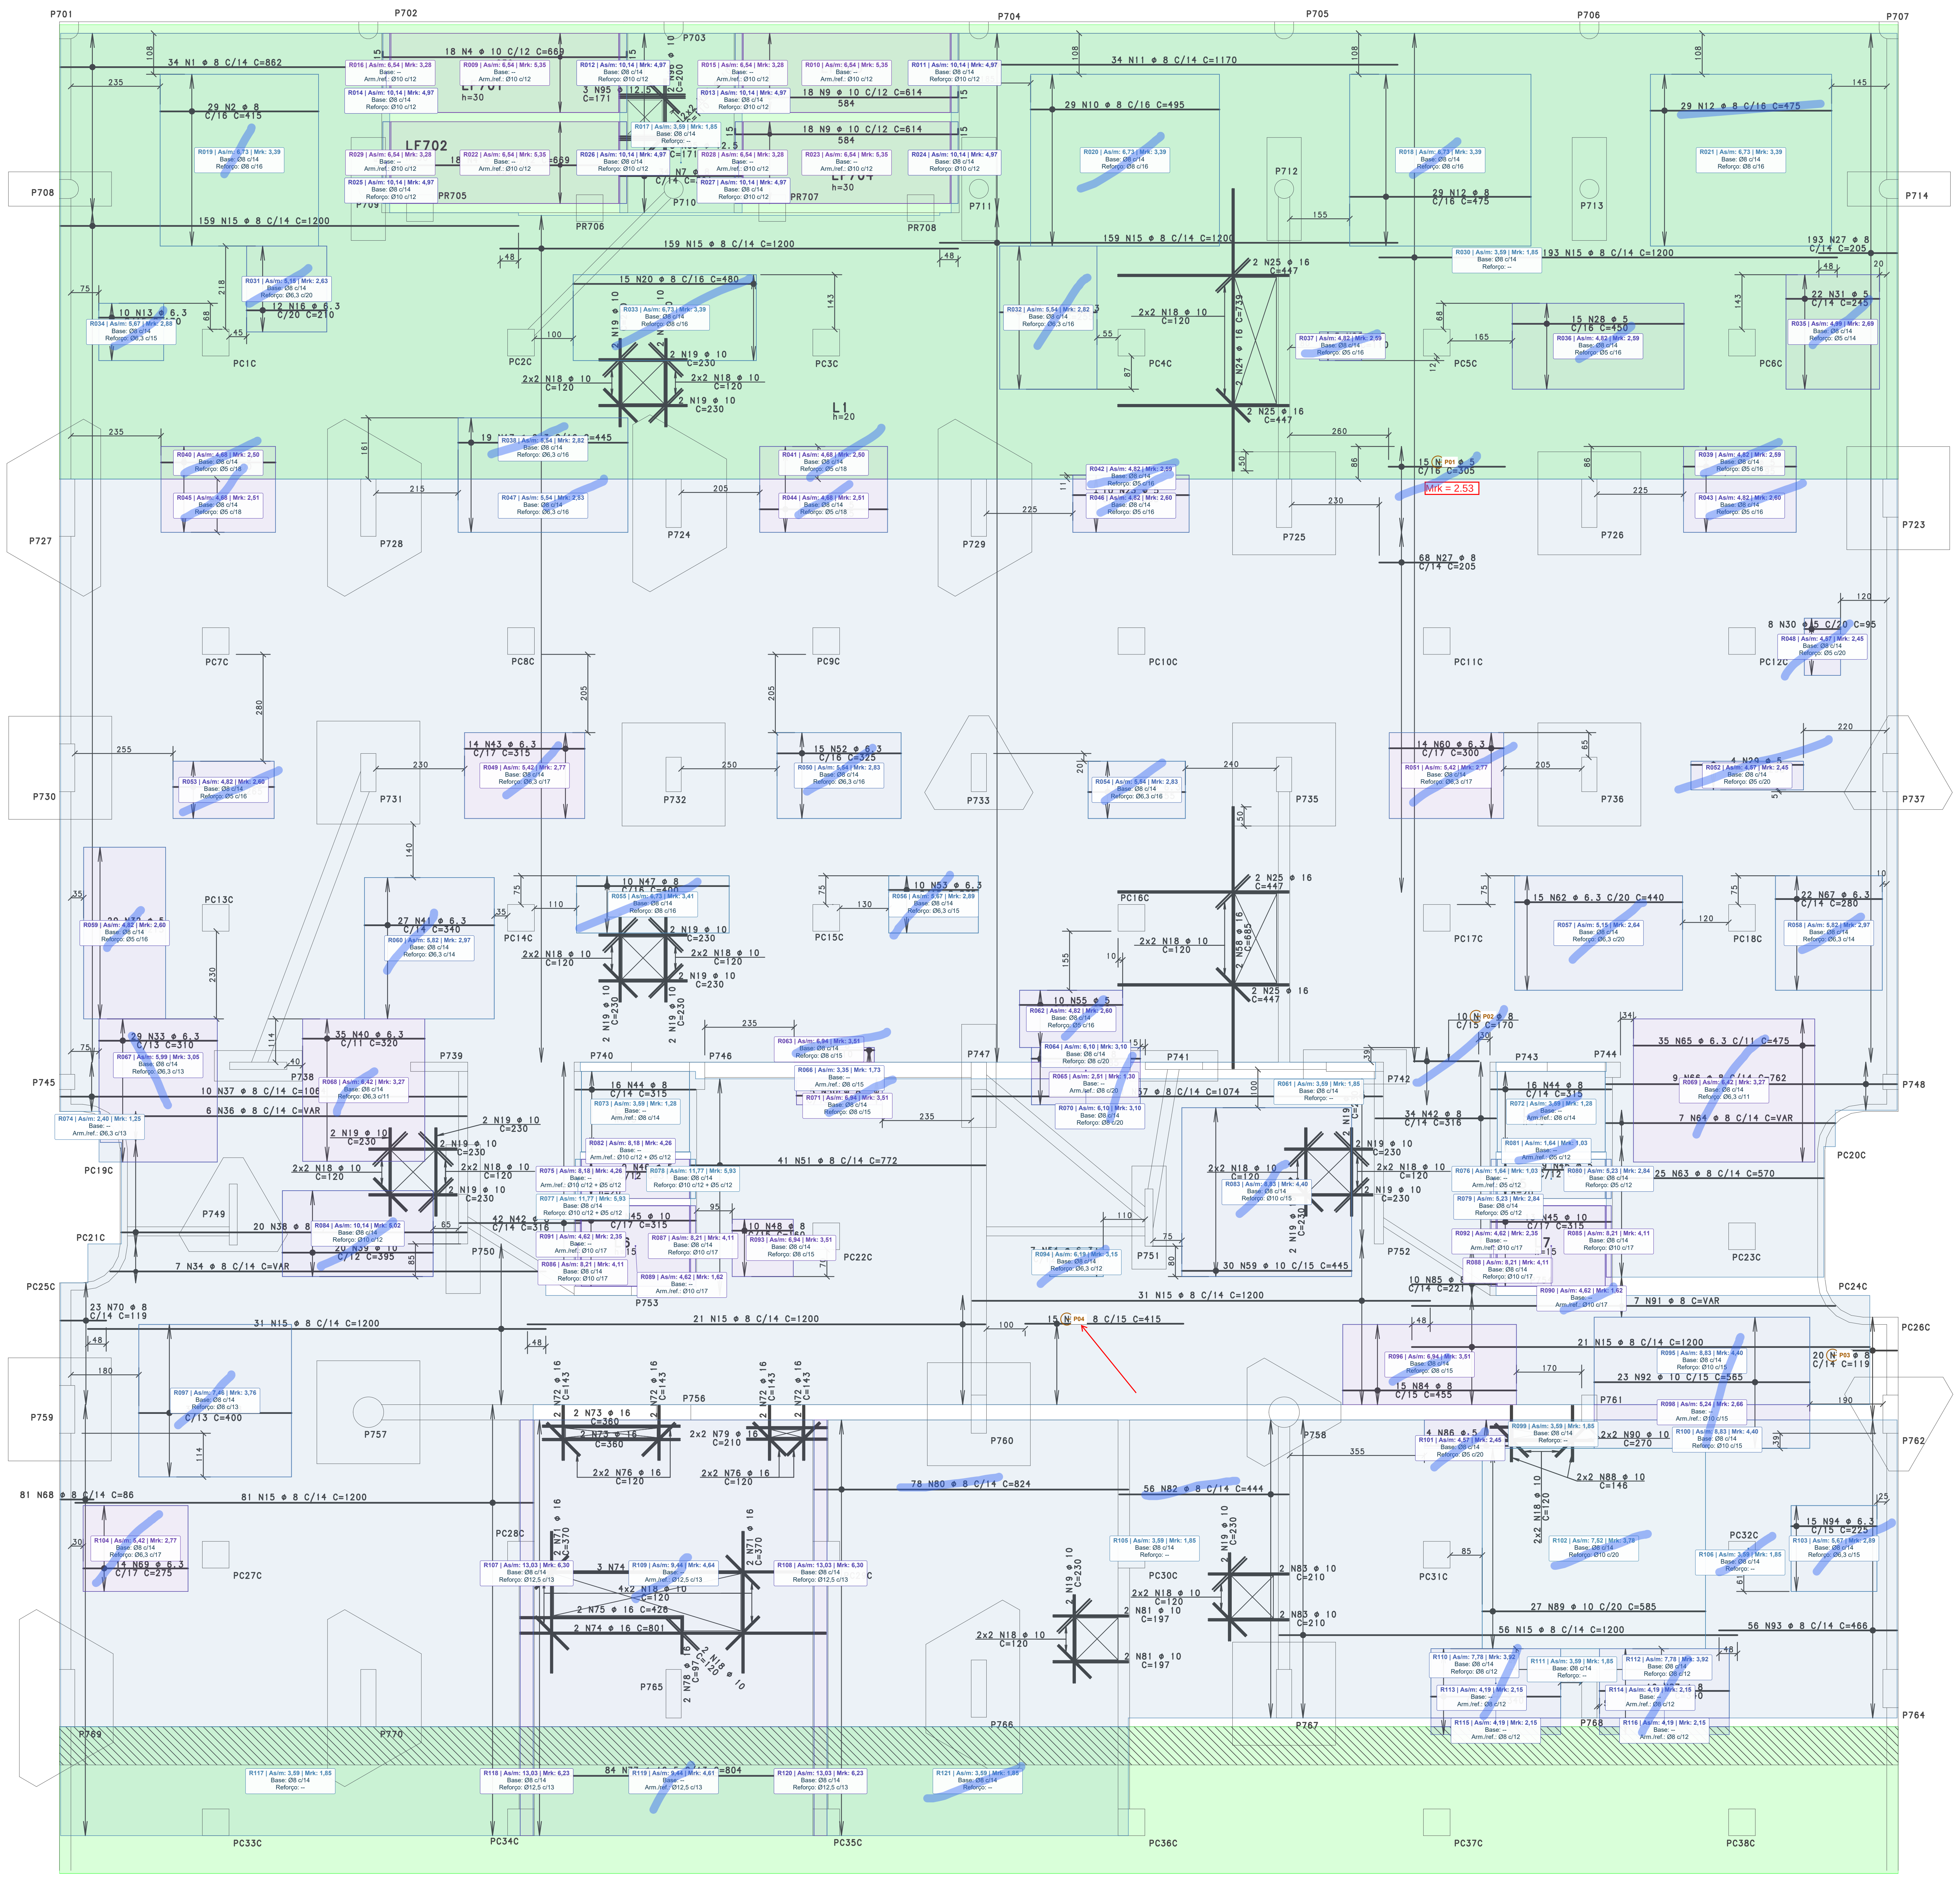

PAVIMENTO TÉRREO PARTE 2 DA LAJE, ARMADURA POSITIVA HORIZONTAL , VER PLANTA 7-305

	AÇO	POS	QUANT	BIT (mm)	COMPRIMENTO UNIT (cm)	COMPRIMENTO TOTAL (cm)
	50A	1	34	8	862	29308
	50A	2	44	8	415	18260
	60B	3	43	5	639	27477
	50A	4	36	10	669	24084
	50A	5	8	10	304	2432
	50A	6	8	10	185	1480
	50A	7	34	8	321	10914
	60B	8	43	5	584	25112
	50A	9	36	10	614	22104
	50A	10	29	8	495	14355
	50A	11	34	8	1170	39780
	50A	12	58	8	475	27550
	50A	13	10	6.3	170	1700
	60B	14	13	5	300	3900
	50A	15	911	8	1200	1093200
	50A	16	12	6.3	210	2520
	50A	17	19	6.3	445	8455
	50A	18	62	10	120	7440
	50A	19	36	10	230	8280
	50A	20	15	8	480	7200
	60B	21	13	5	335	4355
	50A	22	34	6.3	255	8670
	60B	23	25	5	305	7625
	50A	24	2	16	739	1478
	50A	25	8	16	447	3576
	60B	26	5	5	110	550
	50A	27	261	8	205	53505
	60B	28	15	5	450	6750
	60B	29	19	5	295	5605
	60B	30	8	5	95	760
	60B	31	22	5	245	5390
	60B	32	29	5	215	6235
	50A	33	29	6.3	310	8990
	50A	34	7	8	--VAR-	7945
	60B	35	10	5	265	2650
	50A	36	6	8	--VAR-	5598
	50A	37	10	8	1064	10640
	50A	38	20	8	905	18100
	50A	39	20	10	395	7900
	50A	40	35	6.3	320	11200
	50A	41	27	6.3	340	9180
	50A	42	76	8	316	24016
	50A	43	14	6.3	315	4410
	50A	44	32	8	315	10080
	50A	45	26	10	315	8190
	60B	46	18	5	315	5670
	50A	47	41	8	400	16400
	50A	48	10	8	160	1600
	50A	49	3	8	210	630
	50A	50	5	8	225	1125
	50A	51	41	8	772	31652
	50A	52	15	6.3	325	4875
	50A	53	10	6.3	235	2350
	50A	54	7	6.3	140	980
	60B	55	10	5	270	2700
	50A	56	8	8	285	2280
	50A	57	31	8	1074	33294
	50A	58	2	16	685	1370
	50A	59	30	10	445	13350
	50A	60	14	6.3	300	4200
	50A	61	10	8	170	1700
	50A	62	15	6.3	440	6600
	50A	63	25	8	570	14250
	50A	64	7	8	--VAR-	4186
	50A	65	35	6.3	475	16625
	50A	66	9	8	762	6858
	50A	67	22	6.3	280	6160
	50A	68	81	8	86	6966
	50A	69	14	6.3	275	3850
	50A	70	43	8	119	5117
	50A	71	4	16	370	1480
	50A	72	8	16	143	1144
	50A	73	4	16	360	1440
	50A	74	5	16	801	4005
	50A	75	2	16	426	852
	50A	76	8	16	120	960
	50A	77	84	12.5	804	67536
	50A	78	2	16	97	194
	50A	79	4	16	210	840
	50A	80	78	8	824	64272
	50A	81	4	10	197	788
	50A	82	56	8	444	24864
	50A	83	4	10	210	840
	50A	84	15	8	455	6825
	50A	85	10	8	221	2210
	60B	86	4	5	230	920
	50A	87	38	8	340	12920
	50A	88	4	10	146	584
	50A	89	27	10	585	15795
	50A	90	4	10	270	1080
	50A	91	7	8	--VAR-	6209
	50A	92	23	10	565	12995
	50A	93	56	8	466	26096
	50A	94	15	6.3	225	3375
	50A	95	6	12.5	171	1026
	50A	96	2	10	200	400
	50A	97	4	10	110	440

RESUMO TOTAL AÇO CA 50-60

AÇO	BIT (mm)	COMPR (m)	PESO (kg)
60B	5	1057	163
50A	6.3	1041	255
50A	8	16399	6478
50A	10	1282	791
50A	12.5	686	660
50A	16	173	274
Peso Total		60B =	163 kgf
Peso Total		50A =	8458 kgf

LEGENDA

🟩 REGIÃO COM fck 35 MPa

☐ REGIÃO COM fck 40 MPa

REV.	DATA	ALTERAÇÃO	VISTO
01	13/08/26	ATUALIZADA FORMA	DS
00	17/07/26	EMISSÃO INICIAL	MVJ

PROCALK
ESTRUTURAS

RESP. TÉCNICOS
Eng. Edemir C. Simonato
CREA-RS 63038
Eng. Carlos R.M. Morais
CREA-RS 74695

Rua João Abbott, 473/401
Porto Alegre - CEP 90460-150
F. (51)3013.3200
procalk@procalk.com.br
www.procalk.com.br

Obra
WERT PORTO BELO RESIDENCES
PORTO BELO - SC

Assunto
LAJES - MULTI 02 - SETOR 7
PAVIMENTO TÉRREO - PARTE 1

Conteúdo
ARMADURA POSITIVA HORIZONTAL

Cliente: WERT
Número: 24-1454
Desenho: 7-301/1
Identificação: WPBR-EST-EX-7301-PLN-MU2-S07-TE-R01
Desenho: MARCUS
Escala: 1:75
fck: 40/35 MPa
Data: 17/07/2026

Direitos Autorais Reservados Lei N 5194/66

PARA PLOTAGEM UTILIZAR EXCLUSIVAMENTE O ARQUIVO PLT OU PDF.

ATP S07 | 7301 | REGIÕES E ARMADURAS

As/m em cm²/m | Mrk em tf·m/m = |MRd|/1,4 (resistência equivalente, não resistência característica).
h e d em cm; concreto C35/C40 conforme a região do relatório anterior. Valores resistentes em módulo.
Base, reforço e regiões reapresentados sem novo cálculo. Negativas sem base contínua: Base --.
Base -- também indica base não individualizada no relatório; não significa ausência física de armadura.
Pendências / sobreposições com soma não verificada: As/m -- e Mrk --. Armaduras não são somadas nesses casos.
* Posição vertical provisória: envelope horizontal de 20 mm. Demais hipóteses e limites do relatório permanecem.
Rxxx corresponde ao mesmo código do relatório. Pxx marca chamada cuja faixa não foi fechada; sem polígono inventado.
Regiões pequenas: código no desenho e configuração completa nesta legenda. Campos não calculados: --.
Cópia de trabalho - capacidade nominal de seção; não verifica esforços, ancoragem, emendas, ELS ou aprovação da laje.

R001 | As/m 1,96 | Mrk 0,64
Base: --
Arm./ref.: Ø5 c/10
h=12 | C40 | N8

R002 | As/m 1,96 | Mrk 0,64
Base: --
Arm./ref.: Ø5 c/10
h=12 | C40 | N3

R003 | As/m 1,96 | Mrk 0,64
Base: --
Arm./ref.: Ø5 c/10
h=12 | C40 | N3

R004 | As/m 1,96 | Mrk 0,64
Base: --
Arm./ref.: Ø5 c/10
h=12 | C40 | N8

R005 | As/m 1,96 | Mrk 0,64
Base: --
Arm./ref.: Ø5 c/10
h=12 | C40 | N3

R006 | As/m 1,96 | Mrk 0,64
Base: --
Arm./ref.: Ø5 c/10
h=12 | C40 | N8

R007 | As/m 1,96 | Mrk 0,64
Base: --
Arm./ref.: Ø5 c/10
h=12 | C40 | N3

R008 | As/m 1,96 | Mrk 0,64
Base: --
Arm./ref.: Ø5 c/10
h=12 | C40 | N8

R009 | As/m 6,54 | Mrk 5,35
Base: --
Arm./ref.: Ø10 c/12
h=30 | C35 | N4

R010 | As/m 6,54 | Mrk 5,35
Base: --
Arm./ref.: Ø10 c/12
h=30 | C35 | N9

R011 | As/m 10,14 | Mrk 4,97
Base: Ø8 c/14
Reforço: Ø10 c/12
h=20 | C35 | N11,N9

R012 | As/m 10,14 | Mrk 4,97
Base: Ø8 c/14
Reforço: Ø10 c/12
h=20 | C35 | N4,N7

R013 | As/m 10,14 | Mrk 4,97
Base: Ø8 c/14
Reforço: Ø10 c/12
h=20 | C35 | N7,N9

R014 | As/m 10,14 | Mrk 4,97
Base: Ø8 c/14
Reforço: Ø10 c/12
h=20 | C35 | N1,N4

R015 | As/m 6,54 | Mrk 3,28
Base: --
Arm./ref.: Ø10 c/12
h=20 | C35 | N9

R016 | As/m 6,54 | Mrk 3,28
Base: --
Arm./ref.: Ø10 c/12
h=20 | C35 | N4

R017 | As/m 3,59 | Mrk 1,85
Base: Ø8 c/14
Reforço: --
h=20 | C35 | N7

R018 | As/m 6,73 | Mrk 3,39
Base: Ø8 c/14
Reforço: Ø8 c/16
h=20 | C35 | N11,N12,N15

R019 | As/m 6,73 | Mrk 3,39
Base: Ø8 c/14
Reforço: Ø8 c/16
h=20 | C35 | N1,N15,N2

R020 | As/m 6,73 | Mrk 3,39
Base: Ø8 c/14
Reforço: Ø8 c/16
h=20 | C35 | N10,N11,N15

R021 | As/m 6,73 | Mrk 3,39
Base: Ø8 c/14
Reforço: Ø8 c/16
h=20 | C35 | N12,N15,N27

R022 | As/m 6,54 | Mrk 5,35
Base: --
Arm./ref.: Ø10 c/12
h=30 | C35 | N4

R023 | As/m 6,54 | Mrk 5,35
Base: --
Arm./ref.: Ø10 c/12
h=30 | C35 | N9

R024 | As/m 10,14 | Mrk 4,97
Base: Ø8 c/14
Reforço: Ø10 c/12
h=20 | C35 | N11,N9

R025 | As/m 10,14 | Mrk 4,97
Base: Ø8 c/14
Reforço: Ø10 c/12
h=20 | C35 | N1,N4

R026 | As/m 10,14 | Mrk 4,97
Base: Ø8 c/14
Reforço: Ø10 c/12
h=20 | C35 | N4,N7

R027 | As/m 10,14 | Mrk 4,97
Base: Ø8 c/14
Reforço: Ø10 c/12
h=20 | C35 | N7,N9

R028 | As/m 6,54 | Mrk 3,28
Base: --
Arm./ref.: Ø10 c/12
h=20 | C35 | N9

R029 | As/m 6,54 | Mrk 3,28
Base: --
Arm./ref.: Ø10 c/12
h=20 | C35 | N4

R030 | As/m 3,59 | Mrk 1,85
Base: Ø8 c/14
Reforço: --
h=20 | C35 | N1,N11,N15,N27

R031 | As/m 5,15 | Mrk 2,63
Base: Ø8 c/14
Reforço: Ø6,3 c/20
h=20 | C35 | N15,N16

R032 | As/m 5,54 | Mrk 2,82
Base: Ø8 c/14
Reforço: Ø6,3 c/16
h=20 | C35 | N15,N22

R033 | As/m 6,73 | Mrk 3,39
Base: Ø8 c/14
Reforço: Ø8 c/16
h=20 | C35 | N15,N20

R034 | As/m 5,67 | Mrk 2,88
Base: Ø8 c/14
Reforço: Ø6,3 c/15
h=20 | C35 | N13,N15

R035 | As/m 4,99 | Mrk 2,69
Base: Ø8 c/14
Reforço: Ø5 c/14
h=20 | C35 | N15,N27,N31

R036 | As/m 4,82 | Mrk 2,59
Base: Ø8 c/14
Reforço: Ø5 c/16
h=20 | C35 | N15,N28

R037 | As/m 4,82 | Mrk 2,59
Base: Ø8 c/14
Reforço: Ø5 c/16
h=20 | C35 | N15,N26

R038 | As/m 5,54 | Mrk 2,82
Base: Ø8 c/14
Reforço: Ø6,3 c/16
h=20 | C35 | N15,N17

R039 | As/m 4,82 | Mrk 2,59
Base: Ø8 c/14
Reforço: Ø5 c/16
h=20 | C35 | N15,N29

R040 | As/m 4,68 | Mrk 2,50
Base: Ø8 c/14
Reforço: Ø5 c/18
h=20 | C35 | N14,N15

R041 | As/m 4,68 | Mrk 2,50
Base: Ø8 c/14
Reforço: Ø5 c/18
h=20 | C35 | N15,N21

R042 | As/m 4,82 | Mrk 2,59
Base: Ø8 c/14
Reforço: Ø5 c/16
h=20 | C35 | N15,N23

R043 | As/m 4,82 | Mrk 2,60
Base: Ø8 c/14
Reforço: Ø5 c/16
h=20 | C40 | N15,N29

R044 | As/m 4,68 | Mrk 2,51
Base: Ø8 c/14
Reforço: Ø5 c/18
h=20 | C40 | N15,N21

R045 | As/m 4,68 | Mrk 2,51
Base: Ø8 c/14
Reforço: Ø5 c/18
h=20 | C40 | N14,N15

R046 | As/m 4,82 | Mrk 2,60
Base: Ø8 c/14
Reforço: Ø5 c/16
h=20 | C40 | N15,N23

R047 | As/m 5,54 | Mrk 2,83
Base: Ø8 c/14
Reforço: Ø6,3 c/16
h=20 | C40 | N15,N17

R048 | As/m 4,57 | Mrk 2,45
Base: Ø8 c/14
Reforço: Ø5 c/20
h=20 | C40 | N15,N27,N30

R049 | As/m 5,42 | Mrk 2,77
Base: Ø8 c/14
Reforço: Ø6,3 c/17
h=20 | C40 | N15,N43

R050 | As/m 5,54 | Mrk 2,83
Base: Ø8 c/14
Reforço: Ø6,3 c/16
h=20 | C40 | N15,N52

R051 | As/m 5,42 | Mrk 2,77
Base: Ø8 c/14
Reforço: Ø6,3 c/17
h=20 | C40 | N15,N27,N60

R052 | As/m 4,57 | Mrk 2,45
Base: Ø8 c/14
Reforço: Ø5 c/20
h=20 | C40 | N15,N29

R053 | As/m 4,82 | Mrk 2,60
Base: Ø8 c/14
Reforço: Ø5 c/16
h=20 | C40 | N15,N35

R054 | As/m 5,54 | Mrk 2,83
Base: Ø8 c/14
Reforço: Ø6,3 c/16
h=20 | C40 | N15,N22

R055 | As/m 6,73 | Mrk 3,41
Base: Ø8 c/14
Reforço: Ø8 c/16
h=20 | C40 | N15,N47

R056 | As/m 5,67 | Mrk 2,89
Base: Ø8 c/14
Reforço: Ø6,3 c/15
h=20 | C40 | N15,N53

R057 | As/m 5,15 | Mrk 2,64
Base: Ø8 c/14
Reforço: Ø6,3 c/20
h=20 | C40 | N15,N62

R058 | As/m 5,82 | Mrk 2,97
Base: Ø8 c/14
Reforço: Ø6,3 c/14
h=20 | C40 | N15,N27,N67

R059 | As/m 4,82 | Mrk 2,60
Base: Ø8 c/14
Reforço: Ø5 c/16
h=20 | C40 | N15,N32

R060 | As/m 5,82 | Mrk 2,97
Base: Ø8 c/14
Reforço: Ø6,3 c/14
h=20 | C40 | N15,N41

R061 | As/m 3,59 | Mrk 1,85
Base: Ø8 c/14
Reforço: --
h=20 | C40 | N15,N27,N34,N36,N37,N38,N42,N44,N51,N57,N63,N64,N66,N68,N70,N85

R062 | As/m 4,82 | Mrk 2,60
Base: Ø8 c/14
Reforço: Ø5 c/16
h=20 | C40 | N15,N55

R063 | As/m 6,94 | Mrk 3,51
Base: Ø8 c/14
Reforço: Ø8 c/15
h=20 | C40 | N15,N49

R064 | As/m 6,10 | Mrk 3,10
Base: Ø8 c/14
Reforço: Ø8 c/20
h=20 | C40 | N15,N56

R065 | As/m 2,51 | Mrk 1,30
Base: --
Arm./ref.: Ø8 c/20
h=20 | C40 | N56

R066 | As/m 3,35 | Mrk 1,73
Base: --
Arm./ref.: Ø8 c/15
h=20 | C40 | N50

R067 | As/m 5,99 | Mrk 3,05
Base: Ø8 c/14
Reforço: Ø6,3 c/13
h=20 | C40 | N15,N33,N36,N37,N38

R068 | As/m 6,42 | Mrk 3,27
Base: Ø8 c/14
Reforço: Ø6,3 c/11
h=20 | C40 | N15,N36,N37,N38,N40

R069 | As/m 6,42 | Mrk 3,27
Base: Ø8 c/14
Reforço: Ø6,3 c/11
h=20 | C40 | N15,N63,N64,N65,N66

R070 | As/m 6,10 | Mrk 3,10
Base: Ø8 c/14
Reforço: Ø8 c/20
h=20 | C40 | N56,N57

R071 | As/m 6,94 | Mrk 3,51
Base: Ø8 c/14
Reforço: Ø8 c/15
h=20 | C40 | N50,N51

R072 | As/m 3,59 | Mrk 1,28
Base: --
Arm./ref.: Ø8 c/14
h=15 | C40 | N44

R073 | As/m 3,59 | Mrk 1,28
Base: --
Arm./ref.: Ø8 c/14
h=15 | C40 | N44

R074 | As/m 2,40 | Mrk 1,25
Base: --
Arm./ref.: Ø6,3 c/13
h=20 | C40 | N33

R075 | As/m 8,18 | Mrk 4,26
Base: --
Arm./ref.: Ø10 c/12 + Ø5 c/12
h=20 | C40 | N18,N46

R076 | As/m 1,64 | Mrk 1,03
Base: --
Arm./ref.: Ø5 c/12
h=20 | C40 | N46

R077 | As/m 11,77 | Mrk 5,93
Base: Ø8 c/14
Reforço: Ø10 c/12 + Ø5 c/12
h=20 | C40 | N18,N42,N46

R078 | As/m 11,77 | Mrk 5,93
Base: Ø8 c/14
Reforço: Ø10 c/12 + Ø5 c/12
h=20 | C40 | N18,N46,N51

R079 | As/m 5,23 | Mrk 2,84
Base: Ø8 c/14
Reforço: Ø5 c/12
h=20 | C40 | N42,N46

R080 | As/m 5,23 | Mrk 2,84
Base: Ø8 c/14
Reforço: Ø5 c/12
h=20 | C40 | N46,N63

R081 | As/m 1,64 | Mrk 1,03
Base: --
Arm./ref.: Ø5 c/12
h=20 | C40 | N46

R082 | As/m 8,18 | Mrk 4,26
Base: --
Arm./ref.: Ø10 c/12 + Ø5 c/12
h=20 | C40 | N18,N46

R083 | As/m 8,83 | Mrk 4,40
Base: Ø8 c/14
Reforço: Ø10 c/15
h=20 | C40 | N15,N57,N59

R084 | As/m 10,14 | Mrk 5,02
Base: Ø8 c/14
Reforço: Ø10 c/12
h=20 | C40 | N15,N34,N38,N39

R085 | As/m 8,21 | Mrk 4,11
Base: Ø8 c/14
Reforço: Ø10 c/17
h=20 | C40 | N45,N63

R086 | As/m 8,21 | Mrk 4,11
Base: Ø8 c/14
Reforço: Ø10 c/17
h=20 | C40 | N42,N45

R087 | As/m 8,21 | Mrk 4,11
Base: Ø8 c/14
Reforço: Ø10 c/17
h=20 | C40 | N45,N51

R088 | As/m 8,21 | Mrk 4,11
Base: Ø8 c/14
Reforço: Ø10 c/17
h=20 | C40 | N42,N45,N85

R089 | As/m 4,62 | Mrk 1,62
Base: --
Arm./ref.: Ø10 c/17
h=15 | C40 | N45

R090 | As/m 4,62 | Mrk 1,62
Base: --
Arm./ref.: Ø10 c/17
h=15 | C40 | N45

R091 | As/m 4,62 | Mrk 2,35
Base: --
Arm./ref.: Ø10 c/17
h=20 | C40 | N45

R092 | As/m 4,62 | Mrk 2,35
Base: --
Arm./ref.: Ø10 c/17
h=20 | C40 | N45

R093 | As/m 6,94 | Mrk 3,51
Base: Ø8 c/14
Reforço: Ø8 c/15
h=20 | C40 | N48,N51

R094 | As/m 6,19 | Mrk 3,15
Base: Ø8 c/14
Reforço: Ø6,3 c/12
h=20 | C40 | N15,N54

R095 | As/m 8,83 | Mrk 4,40
Base: Ø8 c/14
Reforço: Ø10 c/15
h=20 | C40 | N15,N92

R096 | As/m 6,94 | Mrk 3,51
Base: Ø8 c/14
Reforço: Ø8 c/15
h=20 | C40 | N15,N84

R097 | As/m 7,46 | Mrk 3,76
Base: Ø8 c/14
Reforço: Ø8 c/13
h=20 | C40 | N15,N47

R098 | As/m 5,24 | Mrk 2,66
Base: --
Arm./ref.: Ø10 c/15
h=20 | C40 | N92

R099 | As/m 3,59 | Mrk 1,85
Base: Ø8 c/14
Reforço: --
h=20 | C40 | N15

R100 | As/m 8,83 | Mrk 4,40
Base: Ø8 c/14
Reforço: Ø10 c/15
h=20 | C40 | N15,N92,N93

R101 | As/m 4,57 | Mrk 2,45
Base: Ø8 c/14
Reforço: Ø5 c/20
h=20 | C40 | N15,N86

R102 | As/m 7,52 | Mrk 3,78
Base: Ø8 c/14
Reforço: Ø10 c/20
h=20 | C40 | N15,N89

R103 | As/m 5,67 | Mrk 2,89
Base: Ø8 c/14
Reforço: Ø6,3 c/15
h=20 | C40 | N93,N94

R104 | As/m 5,42 | Mrk 2,77
Base: Ø8 c/14
Reforço: Ø6,3 c/17
h=20 | C40 | N15,N68,N69

R105 | As/m 3,59 | Mrk 1,85
Base: Ø8 c/14
Reforço: --
h=20 | C40 | N15,N80,N82

R106 | As/m 3,59 | Mrk 1,85
Base: Ø8 c/14
Reforço: --
h=20 | C40 | N15,N93

R107 | As/m 13,03 | Mrk 6,30
Base: Ø8 c/14
Reforço: Ø12,5 c/13
h=20 | C40 | N15,N77

R108 | As/m 13,03 | Mrk 6,30
Base: Ø8 c/14
Reforço: Ø12,5 c/13
h=20 | C40 | N77,N80

R109 | As/m 9,44 | Mrk 4,64
Base: --
Arm./ref.: Ø12,5 c/13
h=20 | C40 | N77

R110 | As/m 7,78 | Mrk 3,92
Base: Ø8 c/14
Reforço: Ø8 c/12
h=20 | C40 | N15,N87

R111 | As/m 3,59 | Mrk 1,85
Base: Ø8 c/14
Reforço: --
h=20 | C40 | N15

R112 | As/m 7,78 | Mrk 3,92
Base: Ø8 c/14
Reforço: Ø8 c/12
h=20 | C40 | N15,N87,N93

R113 | As/m 4,19 | Mrk 2,15
Base: --
Arm./ref.: Ø8 c/12
h=20 | C40 | N87

R114 | As/m 4,19 | Mrk 2,15
Base: --
Arm./ref.: Ø8 c/12
h=20 | C40 | N87

R115 | As/m 4,19 | Mrk 2,15
Base: --
Arm./ref.: Ø8 c/12
h=20 | C35 | N87

R116 | As/m 4,19 | Mrk 2,15
Base: --
Arm./ref.: Ø8 c/12
h=20 | C35 | N87

R117 | As/m 3,59 | Mrk 1,85
Base: Ø8 c/14
Reforço: --
h=20 | C35 | N15,N68

R118 | As/m 13,03 | Mrk 6,23
Base: Ø8 c/14
Reforço: Ø12,5 c/13
h=20 | C35 | N15,N77

R119 | As/m 9,44 | Mrk 4,61
Base: --
Arm./ref.: Ø12,5 c/13
h=20 | C35 | N77

R120 | As/m 13,03 | Mrk 6,23
Base: Ø8 c/14
Reforço: Ø12,5 c/13
h=20 | C35 | N77,N80

R121 | As/m 3,59 | Mrk 1,85
Base: Ø8 c/14
Reforço: --
h=20 | C35 | N80

P01 | As/m -- | Mrk --
Base: --
Armadura: Ø5 c/16
Faixa pendente | 7301-O029 | N23

P02 | As/m -- | Mrk --
Base: --
Armadura: Ø8 c/15
Faixa pendente | 7301-O076 | N61

P03 | As/m -- | Mrk --
Base: --
Armadura: Ø8 c/14
Faixa pendente | 7301-O083 | N70

P04 | As/m -- | Mrk --
Base: --
Armadura: Ø8 c/15
Faixa pendente | 7301-O121 | N2