TAMPA DOS RESERVATÓRIOS
ESCALA 1:75

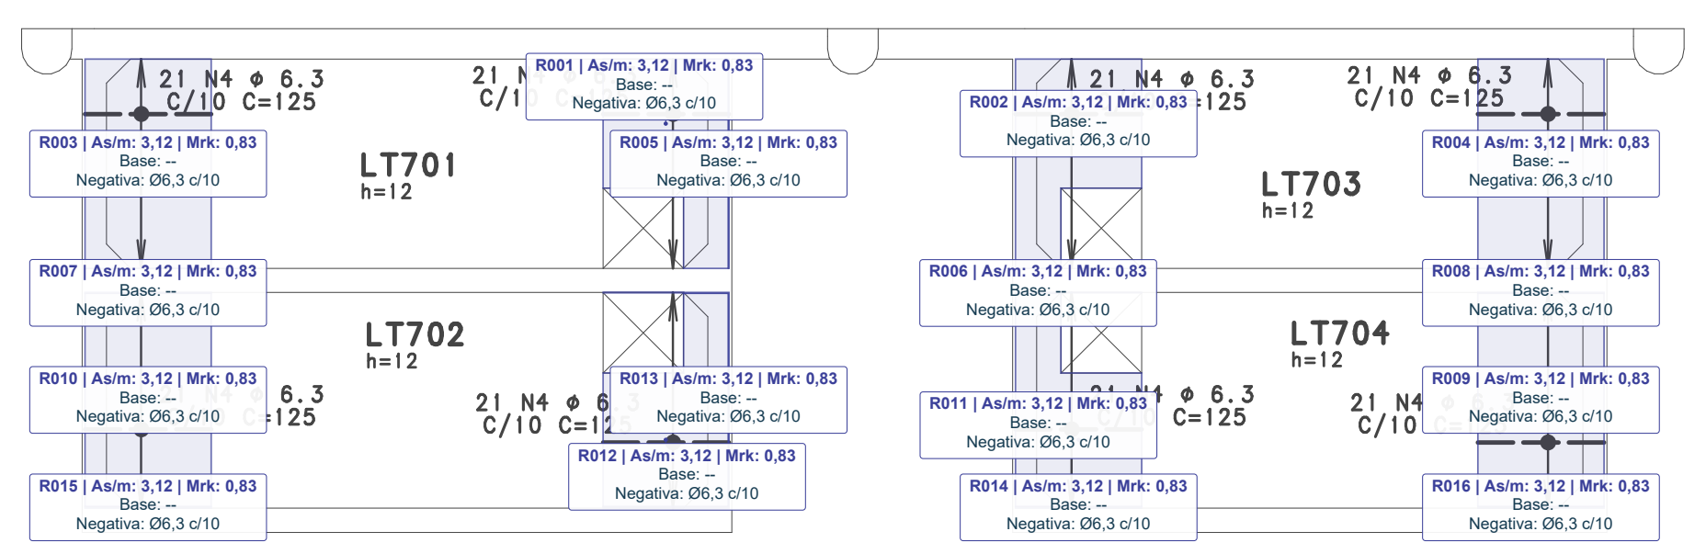

DETALHE CORTE DE BARRAS
SEM ESCALA

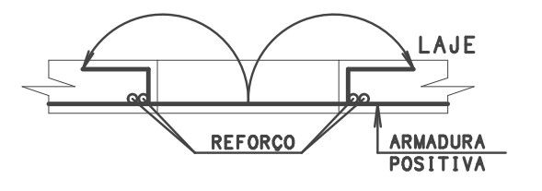

- CORTAR A ARMADURA DA LAJE NO EIXO DO FURO E DOBRAR AS PONTAS CONFORME DETALHE.

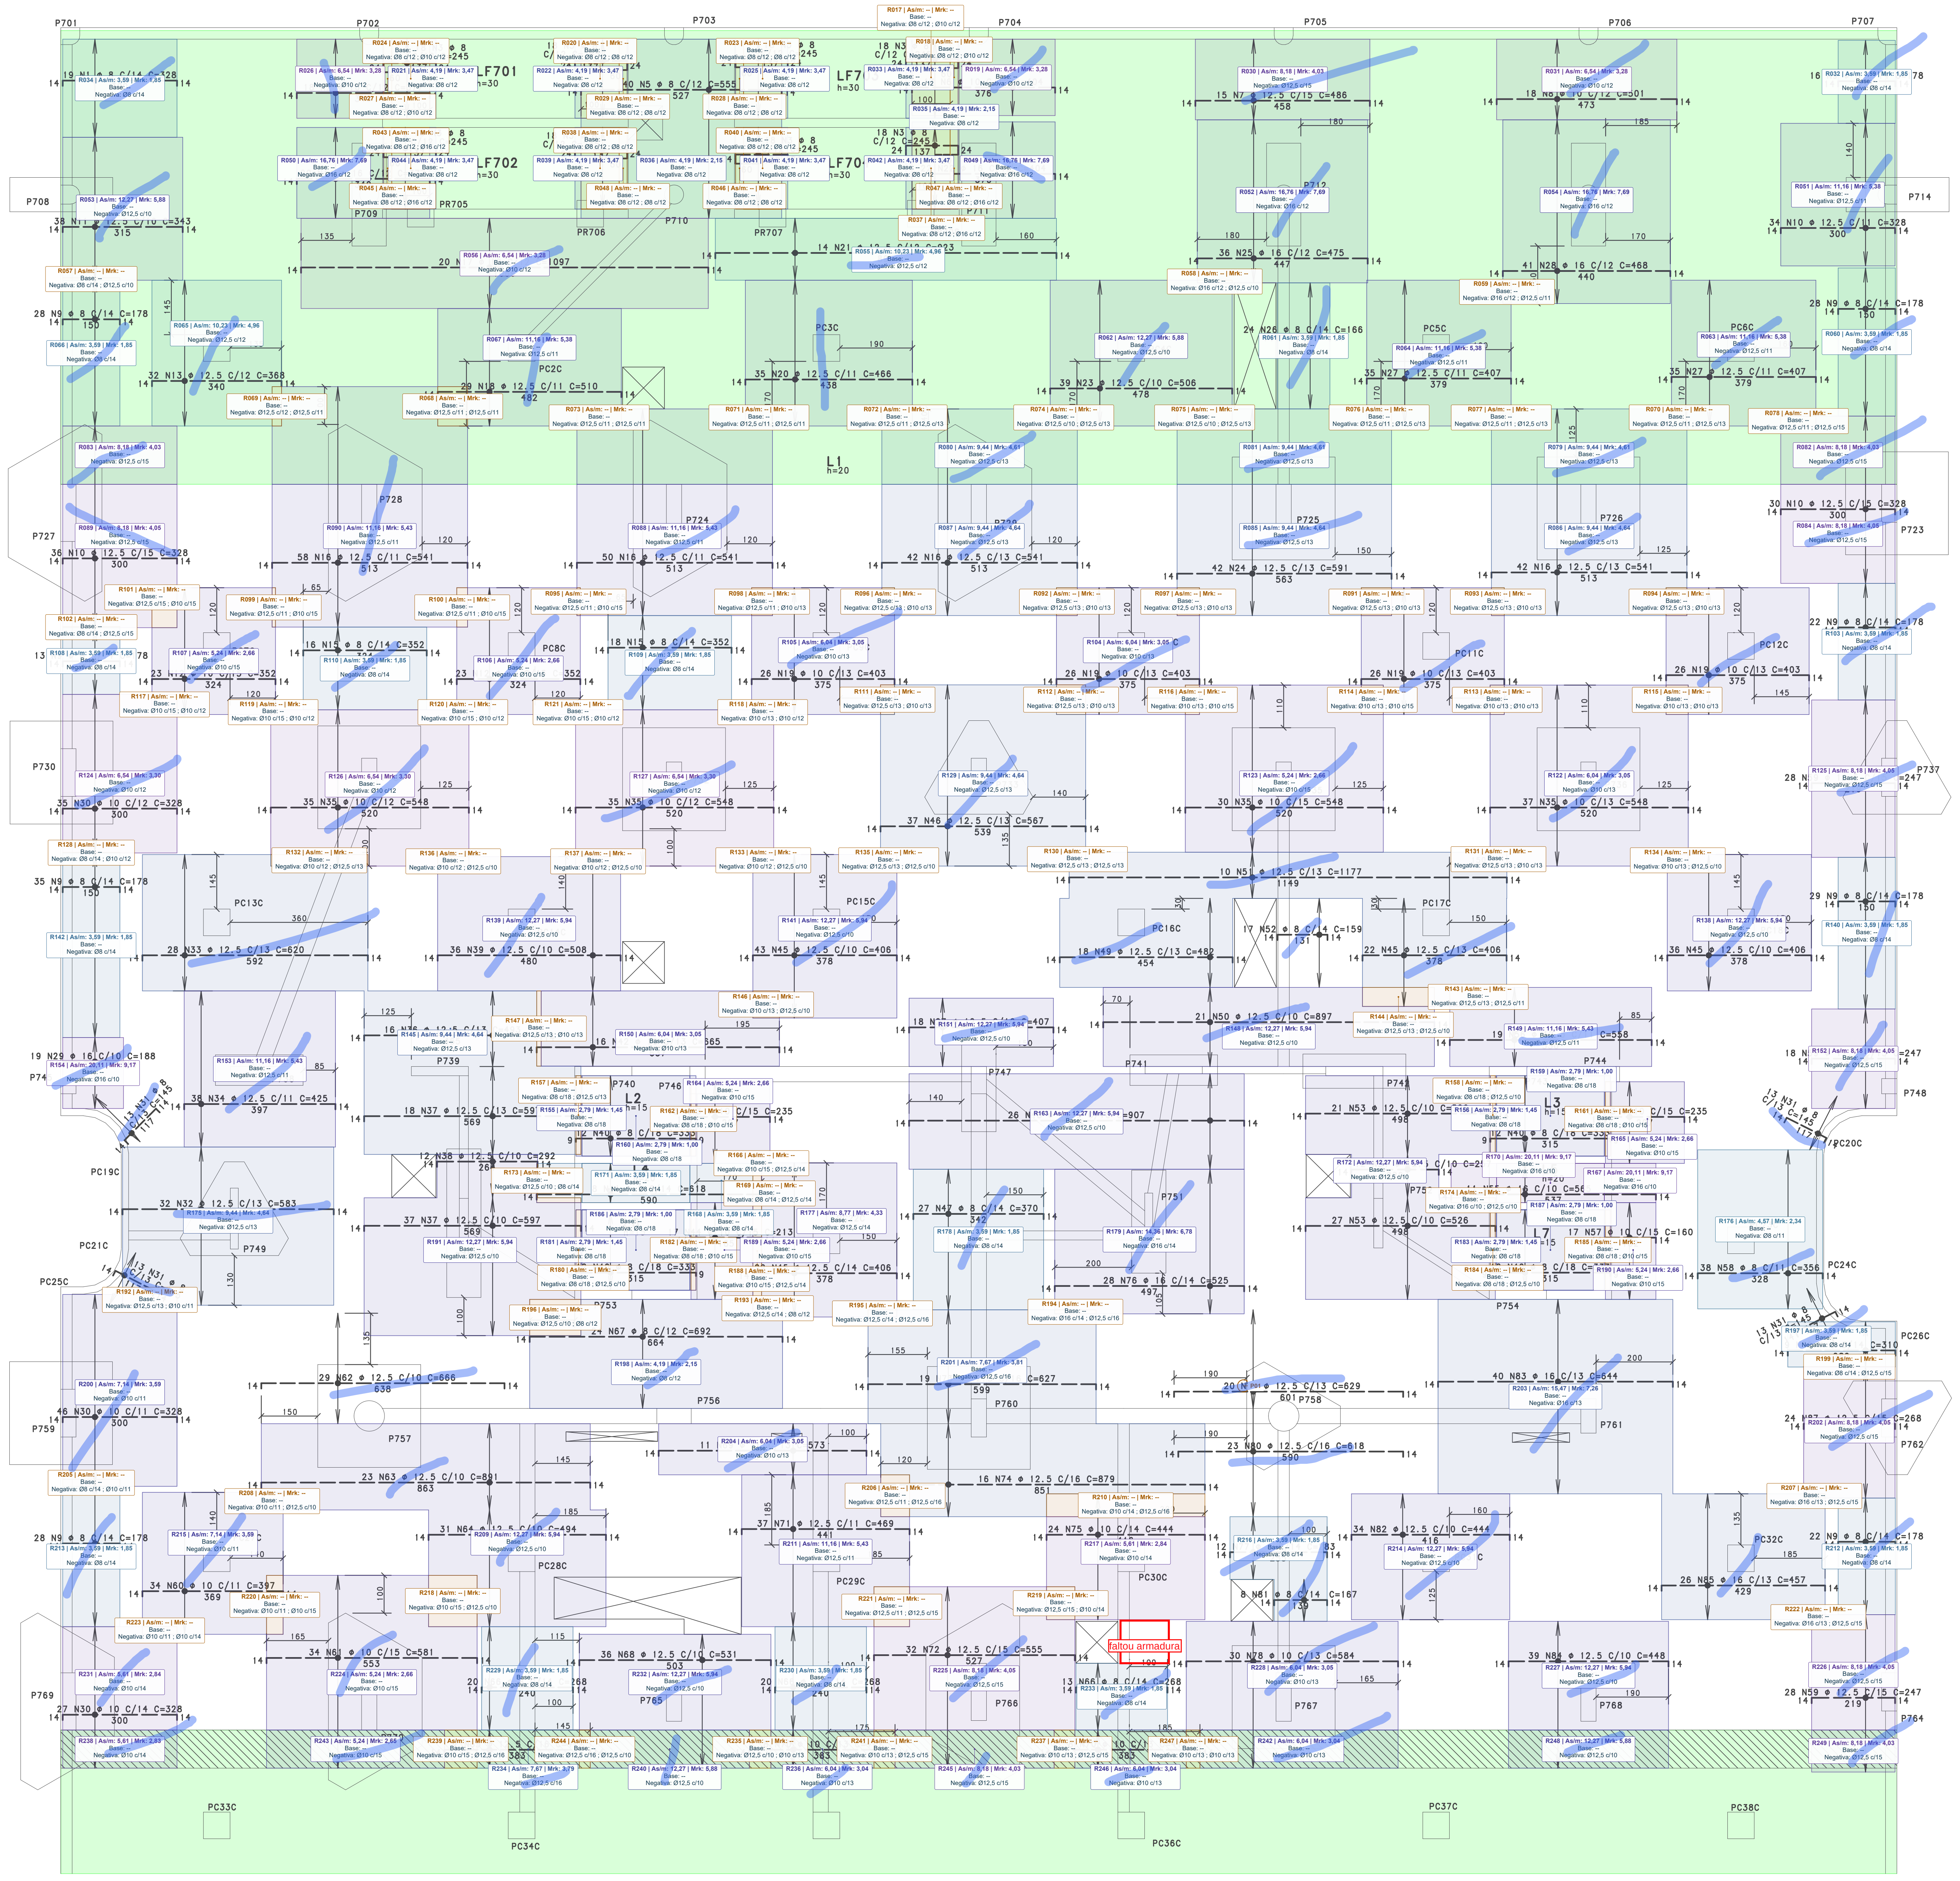

PAVIMENTO TÉRREO PARTE 2 DA LAJE, ARMADURA NEGATIVA HORIZONTAL , VER PLANTA 7-307

AÇO	POS	QUANT	BIT (mm)	COMPRIMENTO UNIT (cm)	COMPRIMENTO TOTAL (cm)
50A	1	19	8	328	6232
50A	2	18	10	377	6786
50A	3	144	8	245	35280
50A	4	168	6.3	125	21000
50A	5	40	8	555	22200
50A	6	17	10	404	6868
50A	7	15	12.5	486	7290
50A	8	18	10	501	9018
50A	9	221	8	178	39338
50A	10	100	12.5	328	32800
50A	11	38	12.5	343	13034
50A	12	46	10	352	16192
50A	13	32	12.5	368	11776
50A	14	20	16	377	7540
50A	15	34	8	352	11968
50A	16	192	12.5	541	103872
50A	17	20	10	1097	21940
50A	18	29	12.5	510	14790
50A	19	104	10	403	41912
50A	20	35	12.5	466	16310
50A	21	14	12.5	923	12922
50A	22	22	16	404	8888
50A	23	39	12.5	506	19734
50A	24	42	12.5	591	24822
50A	25	36	16	475	17100
50A	26	24	8	166	3984
50A	27	88	12.5	407	35816
50A	28	41	16	468	19188
50A	29	19	16	188	3572
50A	30	108	10	328	35424
50A	31	52	8	145	7540
50A	32	32	12.5	583	18656
50A	33	28	12.5	620	17360
50A	34	38	12.5	425	16150
50A	35	137	10	548	75076
50A	36	16	12.5	493	7888
50A	37	55	12.5	597	32835
50A	38	12	12.5	292	3504
50A	39	36	12.5	508	18288
50A	40	48	8	333	15984
50A	41	8	8	618	4944
50A	42	16	10	665	10640
50A	43	30	10	235	7050
50A	44	17	10	213	3621
50A	45	130	12.5	406	52780
50A	46	37	12.5	567	20979
50A	47	27	8	370	9990
50A	48	26	12.5	907	23582
50A	49	18	12.5	482	8676
50A	50	21	12.5	897	18837
50A	51	10	12.5	1177	11770
50A	52	17	8	159	2703
50A	53	48	12.5	526	25248
50A	54	12	12.5	257	3084
50A	55	11	16	565	6215
50A	56	19	12.5	558	10602
50A	57	17	10	160	2720
50A	58	38	8	356	13528
50A	59	74	12.5	247	18278
50A	60	34	10	397	13498
50A	61	34	10	581	19754
50A	62	29	12.5	666	19314
50A	63	23	12.5	891	20493
50A	64	31	12.5	494	15314
50A	65	7	12.5	411	2877
50A	66	53	8	268	14204
50A	67	24	8	692	16608
50A	68	36	12.5	531	19116
50A	69	11	10	573	6303
50A	70	16	10	411	6576
50A	71	37	12.5	469	17353
50A	72	32	12.5	555	17760
50A	73	19	12.5	627	11913
50A	74	16	12.5	879	14064
50A	75	24	10	444	10656
50A	76	28	16	525	14700
50A	77	12	8	283	3396
50A	78	30	10	584	17520
50A	79	20	12.5	629	12580
50A	80	23	12.5	618	14214
50A	81	8	8	167	1336
50A	82	34	12.5	444	15096
50A	83	40	16	644	25760
50A	84	39	12.5	448	17472
50A	85	26	16	457	11882
50A	86	9	8	310	2790
50A	87	24	12.5	268	6432

RESUMO TOTAL AÇO CA 50-60

AÇO	BIT (mm)	COMPR (m)	PESO (kg)
50A	6.3	210	51
50A	8	2120	837
50A	10	3116	1922
50A	12.5	8057	7759
50A	16	1148	1812
Peso Total		50A =	12382 kgf

LEGENDA

🟩 REGIÃO COM fck 35 MPa

☐ REGIÃO COM fck 40 MPa

REV.	DATA	ALTERAÇÃO	VISTO
01	13/08/26	ATUALIZADA FORMA	DS
00	17/07/26	EMISSÃO INICIAL	MVJ

PROCALK
ESTRUTURAS

RESP. TÉCNICOS
Eng. Edemir C. Simonato
CREA-RS 63038
Eng. Carlos R.M. Morais
CREA-RS 74695

Rua João Abbott, 473 / 401
Porto Alegre - CEP 90460-150
F. (51)3013.3200
procalk@procalk.com.br
www.procalk.com.br

Obra
WERT PORTO BELO RESIDENCES
PORTO BELO - SC

Assunto
LAJES - MULTI 02 - SETOR 7
PAVIMENTO TÉRREO - PARTE 1

Conteúdo
ARMADURA NEGATIVA HORIZONTAL

Cliente: WERT
Número: 24-1454
Desenho: 7-303/1
Identificação: WPBR-EST-EX-7303-PLN-MU2-S07-TE-R01
Desenho: MARCUS
Escala: 1:75
fck: 40/35 MPa
Data: 17/07/2026

Direitos Autorais Reservados Lei N 5194/66

100/84

PARA PLOTAGEM UTILIZAR EXCLUSIVAMENTE O ARQUIVO PLT OU PDF.

ATP S07 | 7303 | REGIÕES E ARMADURAS

As/m em cm²/m | Mrk em tf·m/m = |MRd|/1,4 (resistência equivalente, não resistência característica).
h e d em cm; concreto C35/C40 conforme a região do relatório anterior. Valores resistentes em módulo.
Base, reforço e regiões reapresentados sem novo cálculo. Negativas sem base contínua: Base --.
Base -- também indica base não individualizada no relatório; não significa ausência física de armadura.
Pendências / sobreposições com soma não verificada: As/m -- e Mrk --. Armaduras não são somadas nesses casos.
* Posição vertical provisória: envelope horizontal de 20 mm. Demais hipóteses e limites do relatório permanecem.
Rxxx corresponde ao mesmo código do relatório. Pxx marca chamada cuja faixa não foi fechada; sem polígono inventado.
Regiões pequenas: código no desenho e configuração completa nesta legenda. Campos não calculados: --.
Cópia de trabalho - capacidade nominal de seção; não verifica esforços, ancoragem, emendas, ELS ou aprovação da laje.

R001 | As/m 3,12 | Mrk 0,83
Base: --
Negativa: Ø6,3 c/10
h=12 | C40 | N4

R002 | As/m 3,12 | Mrk 0,83
Base: --
Negativa: Ø6,3 c/10
h=12 | C40 | N4

R003 | As/m 3,12 | Mrk 0,83
Base: --
Negativa: Ø6,3 c/10
h=12 | C40 | N4

R004 | As/m 3,12 | Mrk 0,83
Base: --
Negativa: Ø6,3 c/10
h=12 | C40 | N4

R005 | As/m 3,12 | Mrk 0,83
Base: --
Negativa: Ø6,3 c/10
h=12 | C40 | N4

R006 | As/m 3,12 | Mrk 0,83
Base: --
Negativa: Ø6,3 c/10
h=12 | C40 | N4

R007 | As/m 3,12 | Mrk 0,83
Base: --
Negativa: Ø6,3 c/10
h=12 | C40 | N4

R008 | As/m 3,12 | Mrk 0,83
Base: --
Negativa: Ø6,3 c/10
h=12 | C40 | N4

R009 | As/m 3,12 | Mrk 0,83
Base: --
Negativa: Ø6,3 c/10
h=12 | C40 | N4

R010 | As/m 3,12 | Mrk 0,83
Base: --
Negativa: Ø6,3 c/10
h=12 | C40 | N4

R011 | As/m 3,12 | Mrk 0,83
Base: --
Negativa: Ø6,3 c/10
h=12 | C40 | N4

R012 | As/m 3,12 | Mrk 0,83
Base: --
Negativa: Ø6,3 c/10
h=12 | C40 | N4

R013 | As/m 3,12 | Mrk 0,83
Base: --
Negativa: Ø6,3 c/10
h=12 | C40 | N4

R014 | As/m 3,12 | Mrk 0,83
Base: --
Negativa: Ø6,3 c/10
h=12 | C40 | N4

R015 | As/m 3,12 | Mrk 0,83
Base: --
Negativa: Ø6,3 c/10
h=12 | C40 | N4

R016 | As/m 3,12 | Mrk 0,83
Base: --
Negativa: Ø6,3 c/10
h=12 | C40 | N4

R017 | As/m -- | Mrk --
Base: --
Negativa: Ø8 c/12 ; Ø10 c/12
Soma pendente | N3,N6

R018 | As/m -- | Mrk --
Base: --
Negativa: Ø8 c/12 ; Ø10 c/12
Soma pendente | N3,N6

R019 | As/m 6,54 | Mrk 3,28
Base: --
Negativa: Ø10 c/12
h=20 | C35 | N6

R020 | As/m -- | Mrk --
Base: --
Negativa: Ø8 c/12 ; Ø8 c/12
Soma pendente | N3,N5

R021 | As/m 4,19 | Mrk 3,47
Base: --
Negativa: Ø8 c/12
h=30 | C35 | N3

R022 | As/m 4,19 | Mrk 3,47
Base: --
Negativa: Ø8 c/12
h=30 | C35 | N3

R023 | As/m -- | Mrk --
Base: --
Negativa: Ø8 c/12 ; Ø8 c/12
Soma pendente | N3,N5

R024 | As/m -- | Mrk --
Base: --
Negativa: Ø8 c/12 ; Ø10 c/12
Soma pendente | N2,N3

R025 | As/m 4,19 | Mrk 3,47
Base: --
Negativa: Ø8 c/12
h=30 | C35 | N3

R026 | As/m 6,54 | Mrk 3,28
Base: --
Negativa: Ø10 c/12
h=20 | C35 | N2

R027 | As/m -- | Mrk --
Base: --
Negativa: Ø8 c/12 ; Ø10 c/12
Soma pendente | N2,N3

R028 | As/m -- | Mrk --
Base: --
Negativa: Ø8 c/12 ; Ø8 c/12
Soma pendente | N3,N5

R029 | As/m -- | Mrk --
Base: --
Negativa: Ø8 c/12 ; Ø8 c/12
Soma pendente | N3,N5

R030 | As/m 8,18 | Mrk 4,03
Base: --
Negativa: Ø12,5 c/15
h=20 | C35 | N7

R031 | As/m 6,54 | Mrk 3,28
Base: --
Negativa: Ø10 c/12
h=20 | C35 | N8

R032 | As/m 3,59 | Mrk 1,85
Base: --
Negativa: Ø8 c/14
h=20 | C35 | N9

R033 | As/m 4,19 | Mrk 3,47
Base: --
Negativa: Ø8 c/12
h=30 | C35 | N3

R034 | As/m 3,59 | Mrk 1,85
Base: --
Negativa: Ø8 c/14
h=20 | C35 | N1

R035 | As/m 4,19 | Mrk 2,15
Base: --
Negativa: Ø8 c/12
h=20 | C35 | N3

R036 | As/m 4,19 | Mrk 2,15
Base: --
Negativa: Ø8 c/12
h=20 | C35 | N5

R037 | As/m -- | Mrk --
Base: --
Negativa: Ø8 c/12 ; Ø16 c/12
Soma pendente | N22,N3

R038 | As/m -- | Mrk --
Base: --
Negativa: Ø8 c/12 ; Ø8 c/12
Soma pendente | N3,N5

R039 | As/m 4,19 | Mrk 3,47
Base: --
Negativa: Ø8 c/12
h=30 | C35 | N3

R040 | As/m -- | Mrk --
Base: --
Negativa: Ø8 c/12 ; Ø8 c/12
Soma pendente | N3,N5

R041 | As/m 4,19 | Mrk 3,47
Base: --
Negativa: Ø8 c/12
h=30 | C35 | N3

R042 | As/m 4,19 | Mrk 3,47
Base: --
Negativa: Ø8 c/12
h=30 | C35 | N3

R043 | As/m -- | Mrk --
Base: --
Negativa: Ø8 c/12 ; Ø16 c/12
Soma pendente | N14,N3

R044 | As/m 4,19 | Mrk 3,47
Base: --
Negativa: Ø8 c/12
h=30 | C35 | N3

R045 | As/m -- | Mrk --
Base: --
Negativa: Ø8 c/12 ; Ø16 c/12
Soma pendente | N14,N3

R046 | As/m -- | Mrk --
Base: --
Negativa: Ø8 c/12 ; Ø8 c/12
Soma pendente | N3,N5

R047 | As/m -- | Mrk --
Base: --
Negativa: Ø8 c/12 ; Ø16 c/12
Soma pendente | N22,N3

R048 | As/m -- | Mrk --
Base: --
Negativa: Ø8 c/12 ; Ø8 c/12
Soma pendente | N3,N5

R049 | As/m 16,76 | Mrk 7,69
Base: --
Negativa: Ø16 c/12
h=20 | C35 | N22

R050 | As/m 16,76 | Mrk 7,69
Base: --
Negativa: Ø16 c/12
h=20 | C35 | N14

R051 | As/m 11,16 | Mrk 5,38
Base: --
Negativa: Ø12,5 c/11
h=20 | C35 | N10

R052 | As/m 16,76 | Mrk 7,69
Base: --
Negativa: Ø16 c/12
h=20 | C35 | N25

R053 | As/m 12,27 | Mrk 5,88
Base: --
Negativa: Ø12,5 c/10
h=20 | C35 | N11

R054 | As/m 16,76 | Mrk 7,69
Base: --
Negativa: Ø16 c/12
h=20 | C35 | N28

R055 | As/m 10,23 | Mrk 4,96
Base: --
Negativa: Ø12,5 c/12
h=20 | C35 | N21

R056 | As/m 6,54 | Mrk 3,28
Base: --
Negativa: Ø10 c/12
h=20 | C35 | N17

R057 | As/m -- | Mrk --
Base: --
Negativa: Ø8 c/14 ; Ø12,5 c/10
Soma pendente | N11,N9

R058 | As/m -- | Mrk --
Base: --
Negativa: Ø16 c/12 ; Ø12,5 c/10
Soma pendente | N23,N25

R059 | As/m -- | Mrk --
Base: --
Negativa: Ø16 c/12 ; Ø12,5 c/11
Soma pendente | N27,N28

R060 | As/m 3,59 | Mrk 1,85
Base: --
Negativa: Ø8 c/14
h=20 | C35 | N9

R061 | As/m 3,59 | Mrk 1,85
Base: --
Negativa: Ø8 c/14
h=20 | C35 | N26

R062 | As/m 12,27 | Mrk 5,88
Base: --
Negativa: Ø12,5 c/10
h=20 | C35 | N23

R063 | As/m 11,16 | Mrk 5,38
Base: --
Negativa: Ø12,5 c/11
h=20 | C35 | N27

R064 | As/m 11,16 | Mrk 5,38
Base: --
Negativa: Ø12,5 c/11
h=20 | C35 | N27

R065 | As/m 10,23 | Mrk 4,96
Base: --
Negativa: Ø12,5 c/12
h=20 | C35 | N13

R066 | As/m 3,59 | Mrk 1,85
Base: --
Negativa: Ø8 c/14
h=20 | C35 | N9

R067 | As/m 11,16 | Mrk 5,38
Base: --
Negativa: Ø12,5 c/11
h=20 | C35 | N16,N18,N20

R068 | As/m -- | Mrk --
Base: --
Negativa: Ø12,5 c/11 ; Ø12,5 c/11
Soma pendente | N16,N18

R069 | As/m -- | Mrk --
Base: --
Negativa: Ø12,5 c/12 ; Ø12,5 c/11
Soma pendente | N13,N16

R070 | As/m -- | Mrk --
Base: --
Negativa: Ø12,5 c/11 ; Ø12,5 c/13
Soma pendente | N16,N27

R071 | As/m -- | Mrk --
Base: --
Negativa: Ø12,5 c/11 ; Ø12,5 c/11
Soma pendente | N16,N20

R072 | As/m -- | Mrk --
Base: --
Negativa: Ø12,5 c/11 ; Ø12,5 c/13
Soma pendente | N16,N20

R073 | As/m -- | Mrk --
Base: --
Negativa: Ø12,5 c/11 ; Ø12,5 c/11
Soma pendente | N16,N18

R074 | As/m -- | Mrk --
Base: --
Negativa: Ø12,5 c/10 ; Ø12,5 c/13
Soma pendente | N16,N23

R075 | As/m -- | Mrk --
Base: --
Negativa: Ø12,5 c/10 ; Ø12,5 c/13
Soma pendente | N23,N24

R076 | As/m -- | Mrk --
Base: --
Negativa: Ø12,5 c/11 ; Ø12,5 c/13
Soma pendente | N24,N27

R077 | As/m -- | Mrk --
Base: --
Negativa: Ø12,5 c/11 ; Ø12,5 c/13
Soma pendente | N16,N27

R078 | As/m -- | Mrk --
Base: --
Negativa: Ø12,5 c/11 ; Ø12,5 c/15
Soma pendente | N10,N27

R079 | As/m 9,44 | Mrk 4,61
Base: --
Negativa: Ø12,5 c/13
h=20 | C35 | N16

R080 | As/m 9,44 | Mrk 4,61
Base: --
Negativa: Ø12,5 c/13
h=20 | C35 | N16

R081 | As/m 9,44 | Mrk 4,61
Base: --
Negativa: Ø12,5 c/13
h=20 | C35 | N24

R082 | As/m 8,18 | Mrk 4,03
Base: --
Negativa: Ø12,5 c/15
h=20 | C35 | N10

R083 | As/m 8,18 | Mrk 4,03
Base: --
Negativa: Ø12,5 c/15
h=20 | C35 | N10

R084 | As/m 8,18 | Mrk 4,05
Base: --
Negativa: Ø12,5 c/15
h=20 | C40 | N10

R085 | As/m 9,44 | Mrk 4,64
Base: --
Negativa: Ø12,5 c/13
h=20 | C40 | N24

R086 | As/m 9,44 | Mrk 4,64
Base: --
Negativa: Ø12,5 c/13
h=20 | C40 | N16

R087 | As/m 9,44 | Mrk 4,64
Base: --
Negativa: Ø12,5 c/13
h=20 | C40 | N16

R088 | As/m 11,16 | Mrk 5,43
Base: --
Negativa: Ø12,5 c/11
h=20 | C40 | N16

R089 | As/m 8,18 | Mrk 4,05
Base: --
Negativa: Ø12,5 c/15
h=20 | C40 | N10

R090 | As/m 11,16 | Mrk 5,43
Base: --
Negativa: Ø12,5 c/11
h=20 | C40 | N16

R091 | As/m -- | Mrk --
Base: --
Negativa: Ø12,5 c/13 ; Ø10 c/13
Soma pendente | N19,N24

R092 | As/m -- | Mrk --
Base: --
Negativa: Ø12,5 c/13 ; Ø10 c/13
Soma pendente | N16,N19

R093 | As/m -- | Mrk --
Base: --
Negativa: Ø12,5 c/13 ; Ø10 c/13
Soma pendente | N16,N19

R094 | As/m -- | Mrk --
Base: --
Negativa: Ø12,5 c/13 ; Ø10 c/13
Soma pendente | N16,N19

R095 | As/m -- | Mrk --
Base: --
Negativa: Ø12,5 c/11 ; Ø10 c/15
Soma pendente | N12,N16

R096 | As/m -- | Mrk --
Base: --
Negativa: Ø12,5 c/13 ; Ø10 c/13
Soma pendente | N16,N19

R097 | As/m -- | Mrk --
Base: --
Negativa: Ø12,5 c/13 ; Ø10 c/13
Soma pendente | N19,N24

R098 | As/m -- | Mrk --
Base: --
Negativa: Ø12,5 c/11 ; Ø10 c/13
Soma pendente | N16,N19

R099 | As/m -- | Mrk --
Base: --
Negativa: Ø12,5 c/11 ; Ø10 c/15
Soma pendente | N12,N16

R100 | As/m -- | Mrk --
Base: --
Negativa: Ø12,5 c/11 ; Ø10 c/15
Soma pendente | N12,N16

R101 | As/m -- | Mrk --
Base: --
Negativa: Ø12,5 c/15 ; Ø10 c/15
Soma pendente | N10,N12

R102 | As/m -- | Mrk --
Base: --
Negativa: Ø8 c/14 ; Ø12,5 c/15
Soma pendente | N10,N9

R103 | As/m 3,59 | Mrk 1,85
Base: --
Negativa: Ø8 c/14
h=20 | C40 | N9

R104 | As/m 6,04 | Mrk 3,05
Base: --
Negativa: Ø10 c/13
h=20 | C40 | N19

R105 | As/m 6,04 | Mrk 3,05
Base: --
Negativa: Ø10 c/13
h=20 | C40 | N19

R106 | As/m 5,24 | Mrk 2,66
Base: --
Negativa: Ø10 c/15
h=20 | C40 | N12

R107 | As/m 5,24 | Mrk 2,66
Base: --
Negativa: Ø10 c/15
h=20 | C40 | N12

R108 | As/m 3,59 | Mrk 1,85
Base: --
Negativa: Ø8 c/14
h=20 | C40 | N9

R109 | As/m 3,59 | Mrk 1,85
Base: --
Negativa: Ø8 c/14
h=20 | C40 | N15

R110 | As/m 3,59 | Mrk 1,85
Base: --
Negativa: Ø8 c/14
h=20 | C40 | N15

R111 | As/m -- | Mrk --
Base: --
Negativa: Ø12,5 c/13 ; Ø10 c/13
Soma pendente | N19,N46

R112 | As/m -- | Mrk --
Base: --
Negativa: Ø12,5 c/13 ; Ø10 c/13
Soma pendente | N19,N46

R113 | As/m -- | Mrk --
Base: --
Negativa: Ø10 c/13 ; Ø10 c/13
Soma pendente | N19,N35

R114 | As/m -- | Mrk --
Base: --
Negativa: Ø10 c/13 ; Ø10 c/15
Soma pendente | N19,N35

R115 | As/m -- | Mrk --
Base: --
Negativa: Ø10 c/13 ; Ø10 c/13
Soma pendente | N19,N35

R116 | As/m -- | Mrk --
Base: --
Negativa: Ø10 c/13 ; Ø10 c/15
Soma pendente | N19,N35

R117 | As/m -- | Mrk --
Base: --
Negativa: Ø10 c/15 ; Ø10 c/12
Soma pendente | N12,N30

R118 | As/m -- | Mrk --
Base: --
Negativa: Ø10 c/13 ; Ø10 c/12
Soma pendente | N19,N35

R119 | As/m -- | Mrk --
Base: --
Negativa: Ø10 c/15 ; Ø10 c/12
Soma pendente | N12,N35

R120 | As/m -- | Mrk --
Base: --
Negativa: Ø10 c/15 ; Ø10 c/12
Soma pendente | N12,N35

R121 | As/m -- | Mrk --
Base: --
Negativa: Ø10 c/15 ; Ø10 c/12
Soma pendente | N12,N35

R122 | As/m 6,04 | Mrk 3,05
Base: --
Negativa: Ø10 c/13
h=20 | C40 | N19,N35

R123 | As/m 5,24 | Mrk 2,66
Base: --
Negativa: Ø10 c/15
h=20 | C40 | N35

R124 | As/m 6,54 | Mrk 3,30
Base: --
Negativa: Ø10 c/12
h=20 | C40 | N30

R125 | As/m 8,18 | Mrk 4,05
Base: --
Negativa: Ø12,5 c/15
h=20 | C40 | N59

R126 | As/m 6,54 | Mrk 3,30
Base: --
Negativa: Ø10 c/12
h=20 | C40 | N35

R127 | As/m 6,54 | Mrk 3,30
Base: --
Negativa: Ø10 c/12
h=20 | C40 | N35

R128 | As/m -- | Mrk --
Base: --
Negativa: Ø8 c/14 ; Ø10 c/12
Soma pendente | N30,N9

R129 | As/m 9,44 | Mrk 4,64
Base: --
Negativa: Ø12,5 c/13
h=20 | C40 | N45,N46,N49,N51

R130 | As/m -- | Mrk --
Base: --
Negativa: Ø12,5 c/13 ; Ø12,5 c/13
Soma pendente | N46,N51

R131 | As/m -- | Mrk --
Base: --
Negativa: Ø12,5 c/13 ; Ø10 c/13
Soma pendente | N35,N51

R132 | As/m -- | Mrk --
Base: --
Negativa: Ø10 c/12 ; Ø12,5 c/13
Soma pendente | N33,N35

R133 | As/m -- | Mrk --
Base: --
Negativa: Ø10 c/12 ; Ø12,5 c/10
Soma pendente | N35,N45

R134 | As/m -- | Mrk --
Base: --
Negativa: Ø10 c/13 ; Ø12,5 c/10
Soma pendente | N35,N45

R135 | As/m -- | Mrk --
Base: --
Negativa: Ø12,5 c/13 ; Ø12,5 c/10
Soma pendente | N45,N46

R136 | As/m -- | Mrk --
Base: --
Negativa: Ø10 c/12 ; Ø12,5 c/10
Soma pendente | N35,N39

R137 | As/m -- | Mrk --
Base: --
Negativa: Ø10 c/12 ; Ø12,5 c/10
Soma pendente | N35,N39

R138 | As/m 12,27 | Mrk 5,94
Base: --
Negativa: Ø12,5 c/10
h=20 | C40 | N45

R139 | As/m 12,27 | Mrk 5,94
Base: --
Negativa: Ø12,5 c/10
h=20 | C40 | N39

R140 | As/m 3,59 | Mrk 1,85
Base: --
Negativa: Ø8 c/14
h=20 | C40 | N9

R141 | As/m 12,27 | Mrk 5,94
Base: --
Negativa: Ø12,5 c/10
h=20 | C40 | N45

R142 | As/m 3,59 | Mrk 1,85
Base: --
Negativa: Ø8 c/14
h=20 | C40 | N9

R143 | As/m -- | Mrk --
Base: --
Negativa: Ø12,5 c/13 ; Ø12,5 c/11
Soma pendente | N45,N56

R144 | As/m -- | Mrk --
Base: --
Negativa: Ø12,5 c/13 ; Ø12,5 c/10
Soma pendente | N45,N50

R145 | As/m 9,44 | Mrk 4,64
Base: --
Negativa: Ø12,5 c/13
h=20 | C40 | N33,N36,N37

R146 | As/m -- | Mrk --
Base: --
Negativa: Ø10 c/13 ; Ø12,5 c/10
Soma pendente | N42,N45

R147 | As/m -- | Mrk --
Base: --
Negativa: Ø12,5 c/13 ; Ø10 c/13
Soma pendente | N36,N42

R148 | As/m 12,27 | Mrk 5,94
Base: --
Negativa: Ø12,5 c/10
h=20 | C40 | N50

R149 | As/m 11,16 | Mrk 5,43
Base: --
Negativa: Ø12,5 c/11
h=20 | C40 | N56

R150 | As/m 6,04 | Mrk 3,05
Base: --
Negativa: Ø10 c/13
h=20 | C40 | N42

R151 | As/m 12,27 | Mrk 5,94
Base: --
Negativa: Ø12,5 c/10
h=20 | C40 | N27

R152 | As/m 8,18 | Mrk 4,05
Base: --
Negativa: Ø12,5 c/15
h=20 | C40 | N59

R153 | As/m 11,16 | Mrk 5,43
Base: --
Negativa: Ø12,5 c/11
h=20 | C40 | N34

R154 | As/m 20,11 | Mrk 9,17
Base: --
Negativa: Ø16 c/10
h=20 | C40 | N29

R155 | As/m 2,79 | Mrk 1,45
Base: --
Negativa: Ø8 c/18
h=20 | C40 | N40

R156 | As/m 2,79 | Mrk 1,45
Base: --
Negativa: Ø8 c/18
h=20 | C40 | N40

R157 | As/m -- | Mrk --
Base: --
Negativa: Ø8 c/18 ; Ø12,5 c/13
Soma pendente | N37,N40

R158 | As/m -- | Mrk --
Base: --
Negativa: Ø8 c/18 ; Ø12,5 c/10
Soma pendente | N40,N53

R159 | As/m 2,79 | Mrk 1,00
Base: --
Negativa: Ø8 c/18
h=15 | C40 | N40

R160 | As/m 2,79 | Mrk 1,00
Base: --
Negativa: Ø8 c/18
h=15 | C40 | N40

R161 | As/m -- | Mrk --
Base: --
Negativa: Ø8 c/18 ; Ø10 c/15
Soma pendente | N40,N43

R162 | As/m -- | Mrk --
Base: --
Negativa: Ø8 c/18 ; Ø10 c/15
Soma pendente | N40,N43

R163 | As/m 12,27 | Mrk 5,94
Base: --
Negativa: Ø12,5 c/10
h=20 | C40 | N48

R164 | As/m 5,24 | Mrk 2,66
Base: --
Negativa: Ø10 c/15
h=20 | C40 | N43

R165 | As/m 5,24 | Mrk 2,66
Base: --
Negativa: Ø10 c/15
h=20 | C40 | N43

R166 | As/m -- | Mrk --
Base: --
Negativa: Ø10 c/15 ; Ø12,5 c/14
Soma pendente | N43,N45

R167 | As/m 20,11 | Mrk 9,17
Base: --
Negativa: Ø16 c/10
h=20 | C40 | N55

R168 | As/m 3,59 | Mrk 1,85
Base: --
Negativa: Ø8 c/14
h=20 | C40 | N41

R169 | As/m -- | Mrk --
Base: --
Negativa: Ø8 c/14 ; Ø12,5 c/14
Soma pendente | N41,N45

R170 | As/m 20,11 | Mrk 9,17
Base: --
Negativa: Ø16 c/10
h=20 | C40 | N55

R171 | As/m 3,59 | Mrk 1,85
Base: --
Negativa: Ø8 c/14
h=20 | C40 | N41

R172 | As/m 12,27 | Mrk 5,94
Base: --
Negativa: Ø12,5 c/10
h=20 | C40 | N53,N54

R173 | As/m -- | Mrk --
Base: --
Negativa: Ø12,5 c/10 ; Ø8 c/14
Soma pendente | N37,N38,N41

R174 | As/m -- | Mrk --
Base: --
Negativa: Ø16 c/10 ; Ø12,5 c/10
Soma pendente | N53,N55

R175 | As/m 9,44 | Mrk 4,64
Base: --
Negativa: Ø12,5 c/13
h=20 | C40 | N32

R176 | As/m 4,57 | Mrk 2,34
Base: --
Negativa: Ø8 c/11
h=20 | C40 | N58

R177 | As/m 8,77 | Mrk 4,33
Base: --
Negativa: Ø12,5 c/14
h=20 | C40 | N45

R178 | As/m 3,59 | Mrk 1,85
Base: --
Negativa: Ø8 c/14
h=20 | C40 | N47

R179 | As/m 14,36 | Mrk 6,78
Base: --
Negativa: Ø16 c/14
h=20 | C40 | N76

R180 | As/m -- | Mrk --
Base: --
Negativa: Ø8 c/18 ; Ø12,5 c/10
Soma pendente | N37,N40

R181 | As/m 2,79 | Mrk 1,45
Base: --
Negativa: Ø8 c/18
h=20 | C40 | N40

R182 | As/m -- | Mrk --
Base: --
Negativa: Ø8 c/18 ; Ø10 c/15
Soma pendente | N40,N44

R183 | As/m 2,79 | Mrk 1,45
Base: --
Negativa: Ø8 c/18
h=20 | C40 | N40

R184 | As/m -- | Mrk --
Base: --
Negativa: Ø8 c/18 ; Ø12,5 c/10
Soma pendente | N40,N53

R185 | As/m -- | Mrk --
Base: --
Negativa: Ø8 c/18 ; Ø10 c/15
Soma pendente | N40,N57

R186 | As/m 2,79 | Mrk 1,00
Base: --
Negativa: Ø8 c/18
h=15 | C40 | N40

R187 | As/m 2,79 | Mrk 1,00
Base: --
Negativa: Ø8 c/18
h=15 | C40 | N40

R188 | As/m -- | Mrk --
Base: --
Negativa: Ø10 c/15 ; Ø12,5 c/14
Soma pendente | N44,N45

R189 | As/m 5,24 | Mrk 2,66
Base: --
Negativa: Ø10 c/15
h=20 | C40 | N44

R190 | As/m 5,24 | Mrk 2,66
Base: --
Negativa: Ø10 c/15
h=20 | C40 | N57

R191 | As/m 12,27 | Mrk 5,94
Base: --
Negativa: Ø12,5 c/10
h=20 | C40 | N37,N38

R192 | As/m -- | Mrk --
Base: --
Negativa: Ø12,5 c/13 ; Ø10 c/11
Soma pendente | N30,N32

R193 | As/m -- | Mrk --
Base: --
Negativa: Ø12,5 c/14 ; Ø8 c/12
Soma pendente | N45,N67

R194 | As/m -- | Mrk --
Base: --
Negativa: Ø16 c/14 ; Ø12,5 c/16
Soma pendente | N73,N76

R195 | As/m -- | Mrk --
Base: --
Negativa: Ø12,5 c/14 ; Ø12,5 c/16
Soma pendente | N45,N73

R196 | As/m -- | Mrk --
Base: --
Negativa: Ø12,5 c/10 ; Ø8 c/12
Soma pendente | N37,N67

R197 | As/m 3,59 | Mrk 1,85
Base: --
Negativa: Ø8 c/14
h=20 | C40 | N86

R198 | As/m 4,19 | Mrk 2,15
Base: --
Negativa: Ø8 c/12
h=20 | C40 | N67

R199 | As/m -- | Mrk --
Base: --
Negativa: Ø8 c/14 ; Ø12,5 c/15
Soma pendente | N86,N87

R200 | As/m 7,14 | Mrk 3,59
Base: --
Negativa: Ø10 c/11
h=20 | C40 | N30

R201 | As/m 7,67 | Mrk 3,81
Base: --
Negativa: Ø12,5 c/16
h=20 | C40 | N73,N74

R202 | As/m 8,18 | Mrk 4,05
Base: --
Negativa: Ø12,5 c/15
h=20 | C40 | N87

R203 | As/m 15,47 | Mrk 7,26
Base: --
Negativa: Ø16 c/13
h=20 | C40 | N83,N85

R204 | As/m 6,04 | Mrk 3,05
Base: --
Negativa: Ø10 c/13
h=20 | C40 | N69

R205 | As/m -- | Mrk --
Base: --
Negativa: Ø8 c/14 ; Ø10 c/11
Soma pendente | N30,N9

R206 | As/m -- | Mrk --
Base: --
Negativa: Ø12,5 c/11 ; Ø12,5 c/16
Soma pendente | N71,N74

R207 | As/m -- | Mrk --
Base: --
Negativa: Ø16 c/13 ; Ø12,5 c/15
Soma pendente | N85,N87

R208 | As/m -- | Mrk --
Base: --
Negativa: Ø10 c/11 ; Ø12,5 c/10
Soma pendente | N60,N63

R209 | As/m 12,27 | Mrk 5,94
Base: --
Negativa: Ø12,5 c/10
h=20 | C40 | N63,N64

R210 | As/m -- | Mrk --
Base: --
Negativa: Ø10 c/14 ; Ø12,5 c/16
Soma pendente | N74,N75

R211 | As/m 11,16 | Mrk 5,43
Base: --
Negativa: Ø12,5 c/11
h=20 | C40 | N71

R212 | As/m 3,59 | Mrk 1,85
Base: --
Negativa: Ø8 c/14
h=20 | C40 | N9

R213 | As/m 3,59 | Mrk 1,85
Base: --
Negativa: Ø8 c/14
h=20 | C40 | N9

R214 | As/m 12,27 | Mrk 5,94
Base: --
Negativa: Ø12,5 c/10
h=20 | C40 | N82

R215 | As/m 7,14 | Mrk 3,59
Base: --
Negativa: Ø10 c/11
h=20 | C40 | N60

R216 | As/m 3,59 | Mrk 1,85
Base: --
Negativa: Ø8 c/14
h=20 | C40 | N77,N81

R217 | As/m 5,61 | Mrk 2,84
Base: --
Negativa: Ø10 c/14
h=20 | C40 | N75

R218 | As/m -- | Mrk --
Base: --
Negativa: Ø10 c/15 ; Ø12,5 c/10
Soma pendente | N61,N64

R219 | As/m -- | Mrk --
Base: --
Negativa: Ø12,5 c/15 ; Ø10 c/14
Soma pendente | N72,N75

R220 | As/m -- | Mrk --
Base: --
Negativa: Ø10 c/11 ; Ø10 c/15
Soma pendente | N60,N61

R221 | As/m -- | Mrk --
Base: --
Negativa: Ø12,5 c/11 ; Ø12,5 c/15
Soma pendente | N71,N72

R222 | As/m -- | Mrk --
Base: --
Negativa: Ø16 c/13 ; Ø12,5 c/15
Soma pendente | N59,N85

R223 | As/m -- | Mrk --
Base: --
Negativa: Ø10 c/11 ; Ø10 c/14
Soma pendente | N30,N60

R224 | As/m 5,24 | Mrk 2,66
Base: --
Negativa: Ø10 c/15
h=20 | C40 | N61

R225 | As/m 8,18 | Mrk 4,05
Base: --
Negativa: Ø12,5 c/15
h=20 | C40 | N72

R226 | As/m 8,18 | Mrk 4,05
Base: --
Negativa: Ø12,5 c/15
h=20 | C40 | N59

R227 | As/m 12,27 | Mrk 5,94
Base: --
Negativa: Ø12,5 c/10
h=20 | C40 | N84

R228 | As/m 6,04 | Mrk 3,05
Base: --
Negativa: Ø10 c/13
h=20 | C40 | N78

R229 | As/m 3,59 | Mrk 1,85
Base: --
Negativa: Ø8 c/14
h=20 | C40 | N66

R230 | As/m 3,59 | Mrk 1,85
Base: --
Negativa: Ø8 c/14
h=20 | C40 | N66

R231 | As/m 5,61 | Mrk 2,84
Base: --
Negativa: Ø10 c/14
h=20 | C40 | N30

R232 | As/m 12,27 | Mrk 5,94
Base: --
Negativa: Ø12,5 c/10
h=20 | C40 | N68

R233 | As/m 3,59 | Mrk 1,85
Base: --
Negativa: Ø8 c/14
h=20 | C40 | N66

R234 | As/m 7,67 | Mrk 3,79
Base: --
Negativa: Ø12,5 c/16
h=20 | C35 | N65

R235 | As/m -- | Mrk --
Base: --
Negativa: Ø12,5 c/10 ; Ø10 c/13
Soma pendente | N68,N70

R236 | As/m 6,04 | Mrk 3,04
Base: --
Negativa: Ø10 c/13
h=20 | C35 | N70

R237 | As/m -- | Mrk --
Base: --
Negativa: Ø10 c/13 ; Ø12,5 c/15
Soma pendente | N70,N72

R238 | As/m 5,61 | Mrk 2,83
Base: --
Negativa: Ø10 c/14
h=20 | C35 | N30

R239 | As/m -- | Mrk --
Base: --
Negativa: Ø10 c/15 ; Ø12,5 c/16
Soma pendente | N61,N65

R240 | As/m 12,27 | Mrk 5,88
Base: --
Negativa: Ø12,5 c/10
h=20 | C35 | N68

R241 | As/m -- | Mrk --
Base: --
Negativa: Ø10 c/13 ; Ø12,5 c/15
Soma pendente | N70,N72

R242 | As/m 6,04 | Mrk 3,04
Base: --
Negativa: Ø10 c/13
h=20 | C35 | N78

R243 | As/m 5,24 | Mrk 2,65
Base: --
Negativa: Ø10 c/15
h=20 | C35 | N61

R244 | As/m -- | Mrk --
Base: --
Negativa: Ø12,5 c/16 ; Ø12,5 c/10
Soma pendente | N65,N68

R245 | As/m 8,18 | Mrk 4,03
Base: --
Negativa: Ø12,5 c/15
h=20 | C35 | N72

R246 | As/m 6,04 | Mrk 3,04
Base: --
Negativa: Ø10 c/13
h=20 | C35 | N70

R247 | As/m -- | Mrk --
Base: --
Negativa: Ø10 c/13 ; Ø10 c/13
Soma pendente | N70,N78

R248 | As/m 12,27 | Mrk 5,88
Base: --
Negativa: Ø12,5 c/10
h=20 | C35 | N84

R249 | As/m 8,18 | Mrk 4,03
Base: --
Negativa: Ø12,5 c/15
h=20 | C35 | N59

P01 | As/m -- | Mrk --
Base: --
Armadura: Ø12,5 c/13
Faixa pendente | 7303-O127 | N79