TAMPA DOS RESERVATÓRIOS
ESCALA 1:75

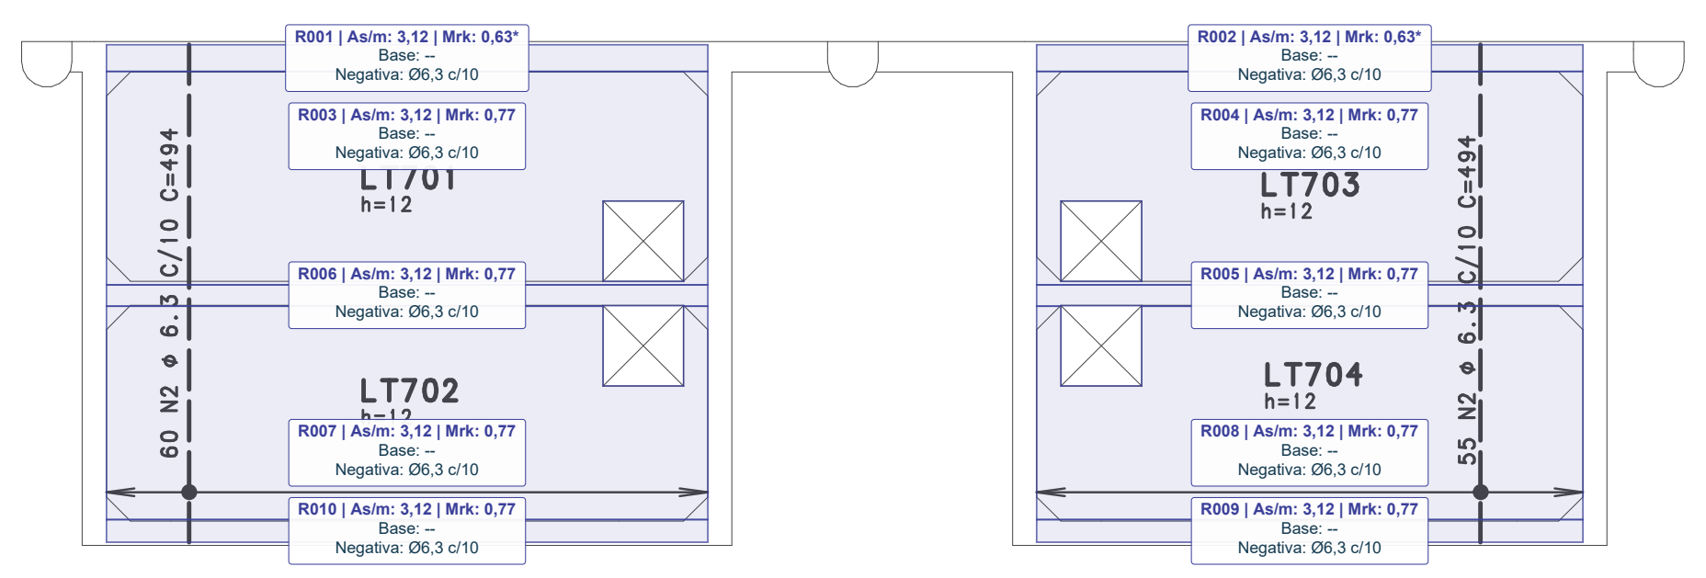
R001 | As/m: 3,12 | Mrk: 0,63*
Base: --
Negativa: Ø6,3 c/10
R002 | As/m: 3,12 | Mrk: 0,63*
Base: --
Negativa: Ø6,3 c/10
R003 | As/m: 3,12 | Mrk: 0,77
R004 | As/m: 3,12 | Mrk: 0,77
LT701
h=12
LT703
h=12
R006 | As/m: 3,12 | Mrk: 0,77
R005 | As/m: 3,12 | Mrk: 0,77
LT702
h=12
LT704
h=12
R007 | As/m: 3,12 | Mrk: 0,77
R008 | As/m: 3,12 | Mrk: 0,77
R010 | As/m: 3,12 | Mrk: 0,77
R009 | As/m: 3,12 | Mrk: 0,77
60 N2 ф 6.3 C/10 C=494
55 N2 ф 6.3 C/10 C=494

DETALHE CORTE DE BARRAS
SEM ESCALA

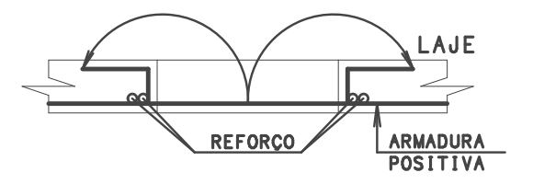

- CORTAR A ARMADURA DA LAJE NO EIXO DO FURO E DOBRAR AS PONTAS CONFORME DETALHE.

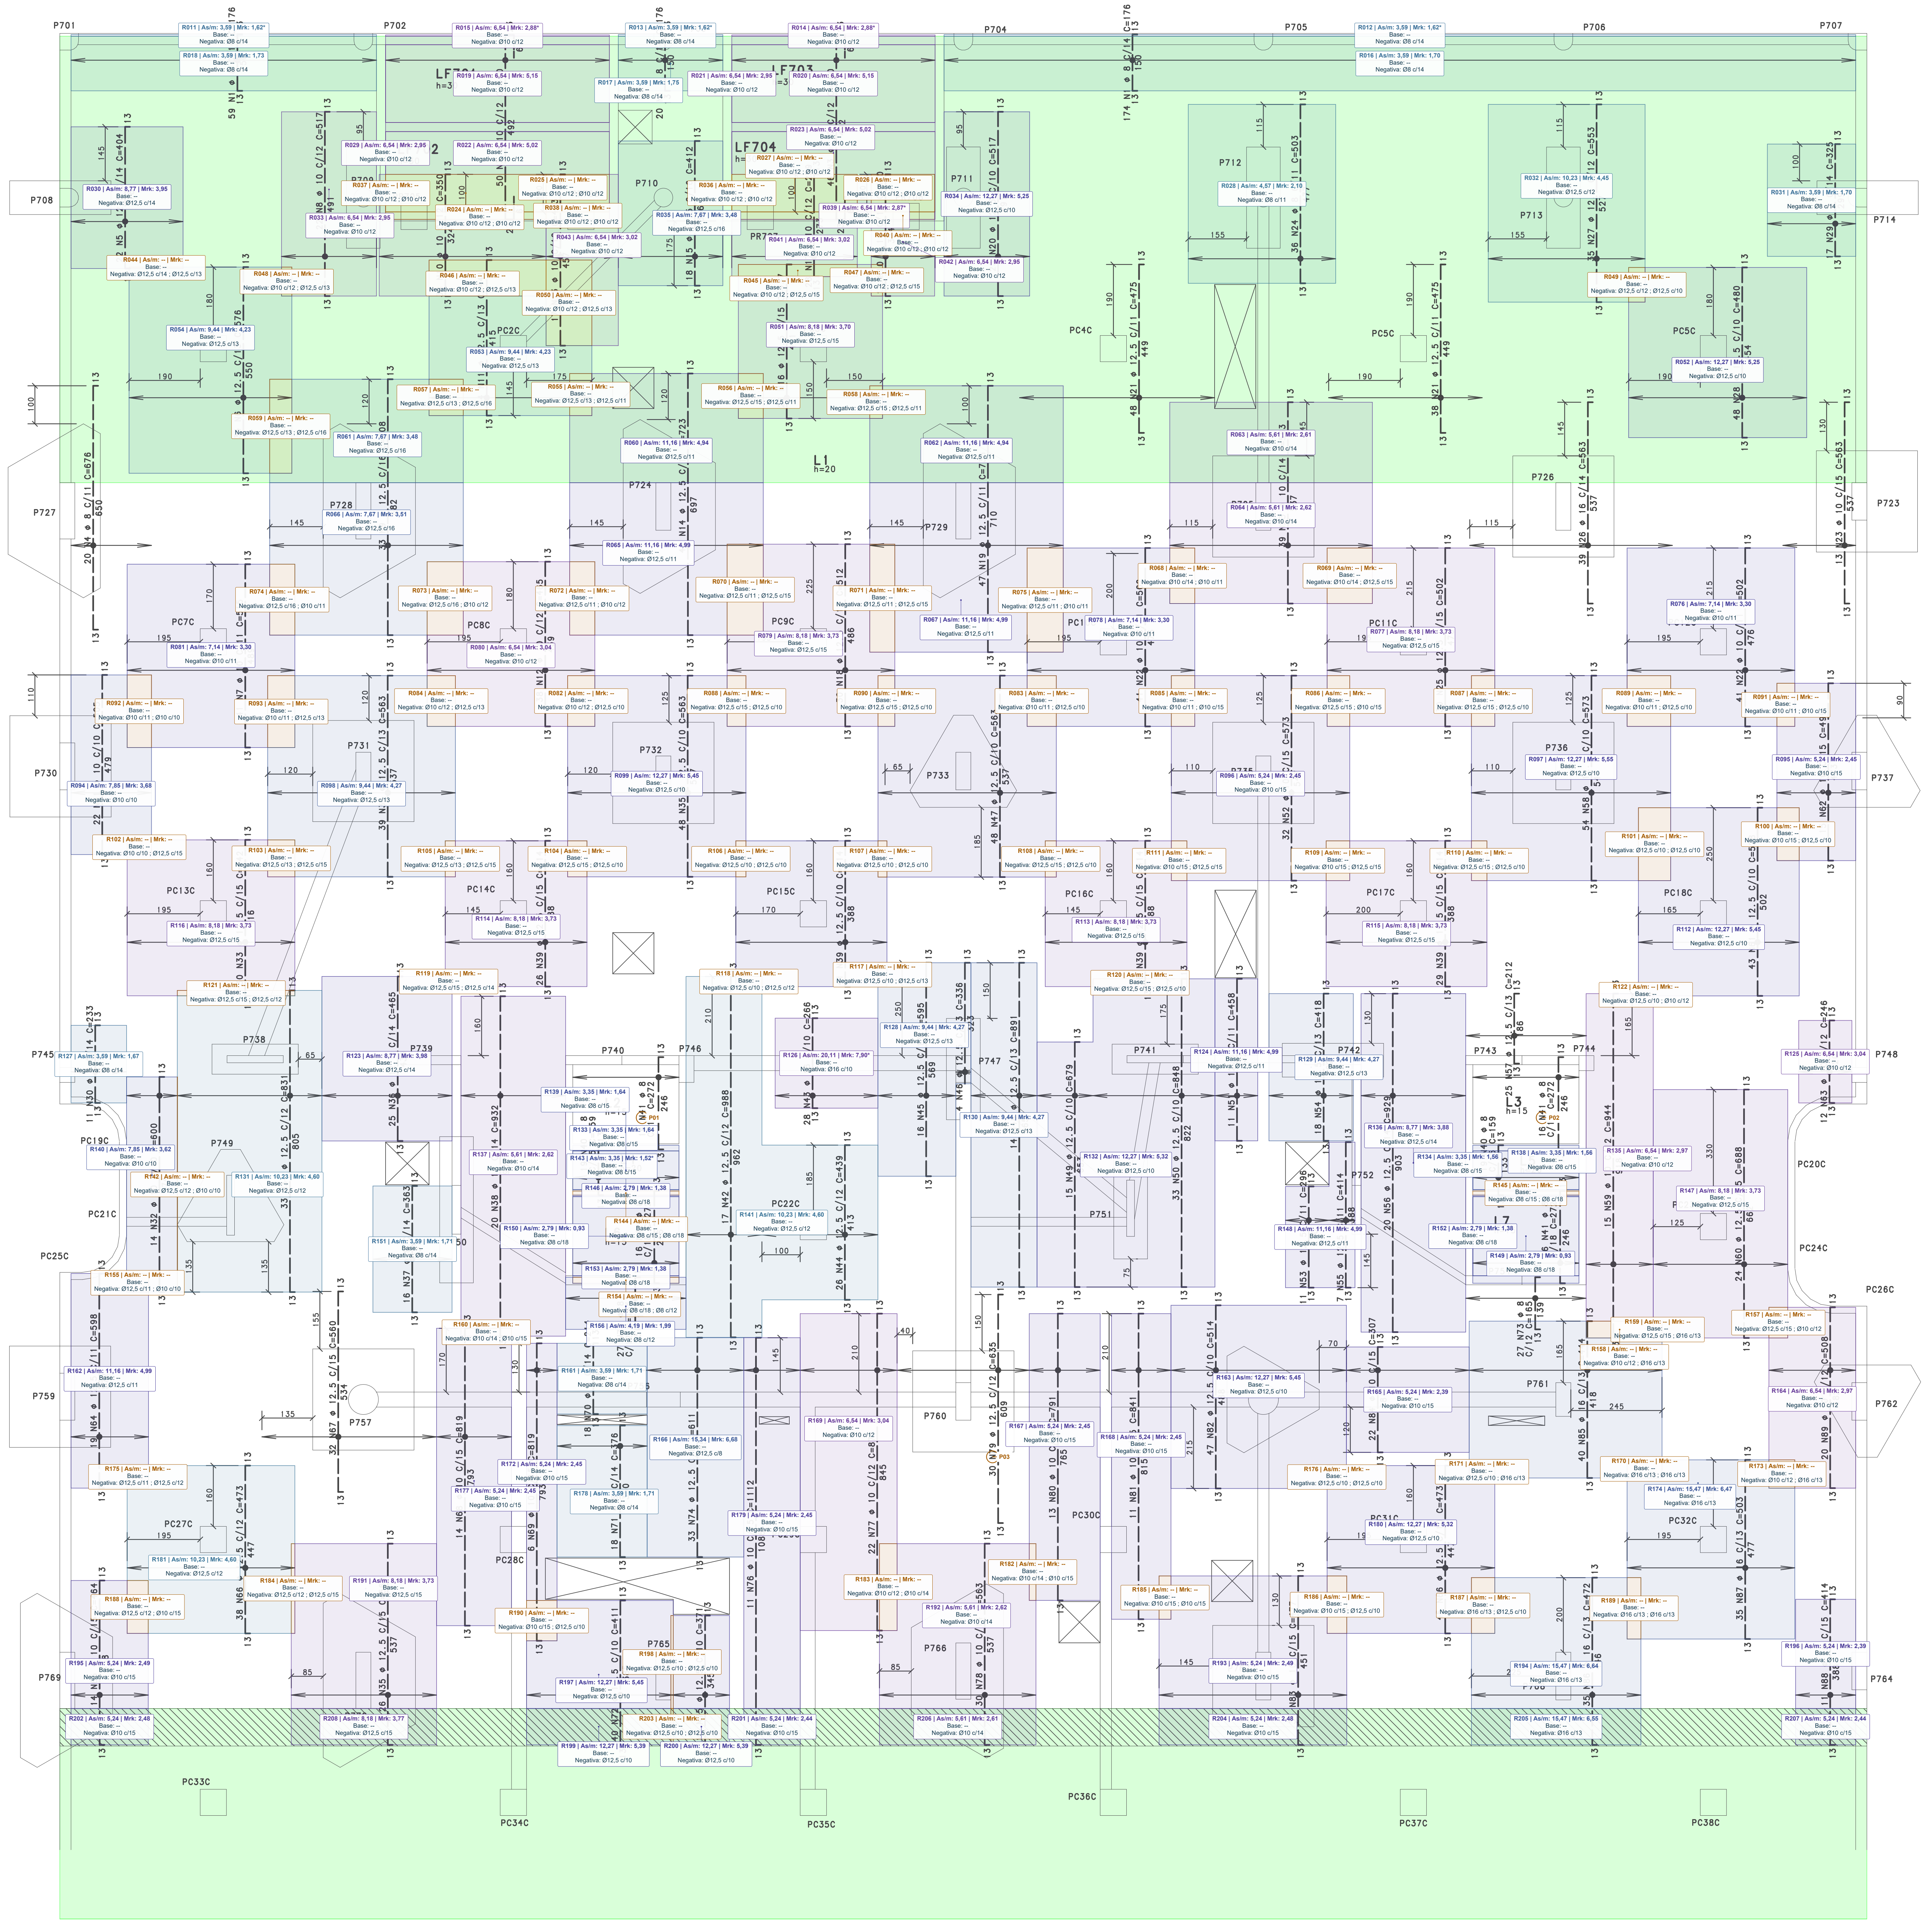

PAVIMENTO TÉRREO PARTE 2 DA LAJE, ARMADURA NEGATIVA VERTICAL , VER PLANTA 7-308

AÇO	POS	QUANT	BIT (mm)	COMPRIMENTO UNIT (cm)	COMPRIMENTO TOTAL (cm)
50A	1	253	8	176	44528
50A	2	115	6.3	494	56810
50A	3	96	10	660	63360
50A	4	20	8	676	13520
50A	5	22	12.5	404	8888
50A	6	34	12.5	576	19584
50A	7	41	10	515	21115
50A	8	22	10	517	11374
50A	9	33	12.5	708	23364
50A	10	53	10	350	18550
50A	11	34	12.5	441	14994
50A	12	38	10	465	17670
50A	13	17	10	483	8211
50A	14	47	12.5	723	33981
50A	15	18	12.5	412	7416
50A	16	26	12.5	437	11362
50A	17	28	10	299	8372
50A	18	30	12.5	512	15360
50A	19	47	12.5	736	34592
50A	20	23	12.5	517	11891
50A	21	86	12.5	475	40850
50A	22	82	10	502	41164
50A	23	52	10	563	29276
50A	24	36	8	503	18108
50A	25	30	12.5	502	15060
50A	26	39	16	563	21957
50A	27	35	12.5	553	19355
50A	28	48	12.5	480	23040
50A	29	17	8	325	5525
50A	30	11	8	233	2563
50A	31	22	10	505	11110
50A	32	14	10	600	8400
50A	33	30	12.5	442	13260
50A	34	33	12.5	831	27423
50A	35	113	12.5	563	63619
50A	36	25	12.5	465	11625
50A	37	16	8	363	5808
50A	38	20	10	932	18640
50A	39	122	12.5	414	50508
50A	40	38	8	159	6042
50A	41	64	8	272	17408
50A	42	17	12.5	988	16796
50A	43	28	16	266	7448
50A	44	26	12.5	439	11414
50A	45	16	12.5	595	9520
50A	46	4	12.5	336	1344
50A	47	48	12.5	563	27024
50A	48	14	12.5	891	12474
50A	49	15	12.5	679	10185
50A	50	33	12.5	848	27984
50A	51	11	12.5	458	5038
50A	52	32	10	573	18336
50A	53	11	12.5	296	3256
50A	54	18	12.5	418	7524
50A	55	7	12.5	414	2898
50A	56	20	12.5	929	18580
50A	57	25	12.5	212	5300
50A	58	54	12.5	573	30942
50A	59	15	10	944	14160
50A	60	24	12.5	688	16512
50A	61	43	12.5	528	22704
50A	62	15	10	499	7485
50A	63	12	10	246	2952
50A	64	19	12.5	598	11362
50A	65	14	10	464	6496
50A	66	83	12.5	473	39259
50A	67	32	12.5	560	17920
50A	68	14	10	819	11466
50A	69	6	10	819	4914
50A	70	18	8	214	3852
50A	71	18	8	376	6768
50A	72	40	12.5	411	16440
50A	73	54	8	165	8910
50A	74	33	12.5	611	20163
50A	75	16	12.5	371	5936
50A	76	11	10	1112	12232
50A	77	22	10	871	19162
50A	78	30	10	563	16890
50A	79	30	12.5	635	19050
50A	80	13	10	791	10283
50A	81	11	10	841	9251
50A	82	47	12.5	514	24158
50A	83	34	10	477	16218
50A	84	22	10	307	6754
50A	85	40	16	444	17760
50A	86	35	16	472	16520
50A	87	35	16	503	17605
50A	88	11	10	414	4554
50A	89	20	10	508	10160

RESUMO TOTAL AÇO CA 50-60

AÇO	BIT (mm)	COMPR (m)	PESO (kg)
50A	6.3	568	139
50A	8	1330	525
50A	10	4286	2644
50A	12.5	8300	7992
50A	16	813	1283
Peso Total		50A =	12584 kgf

LEGENDA

🟩 REGIÃO COM fck 35 MPa

☐ REGIÃO COM fck 40 MPa

REV.	DATA	ALTERAÇÃO	VISTO
01	13/08/26	ATUALIZADA FORMA	DS
00	17/07/26	EMISSÃO INICIAL	MVJ

PROCALK
ESTRUTURAS

RESP. TÉCNICOS
Eng. Edemir C. Simonato
CREA-RS 63038
Eng. Carlos R.M. Morais
CREA-RS 74695

Rua João Abbott, 473/401
Porto Alegre - CEP 90460-150
F. (51)3013.3200
procalk@procalk.com.br
www.procalk.com.br

Obra: WERT PORTO BELO RESIDENCES
PORTO BELO - SC
Assunto: LAJES - MULTI 02 - SETOR 7
PAVIMENTO TÉRREO - PARTE 1
Conteúdo: ARMADURA NEGATIVA VERTICAL
Cliente: WERT
Número: 24-1454
Desenho: 7-304/1
Identificação: WPBR-EST-EX-7304-PLN-MU2-S07-TE-R01
Desenho: MARCUS
Escala: 1:75
fck: 40/35 MPa
Data: 17/07/2026

PARA PLOTAGEM UTILIZAR EXCLUSIVAMENTE O ARQUIVO PLT OU PDF.

Direitos Autorais Reservados Lei N 5194/66

ATP S07 | 7304 | REGIÕES E ARMADURAS

As/m em cm²/m | Mrk em tf·m/m = |MRd|/1,4 (resistência equivalente, não resistência característica).
h e d em cm; concreto C35/C40 conforme a região do relatório anterior. Valores resistentes em módulo.
Base, reforço e regiões reapresentados sem novo cálculo. Negativas sem base contínua: Base --.
Base -- também indica base não individualizada no relatório; não significa ausência física de armadura.
Pendências / sobreposições com soma não verificada: As/m -- e Mrk --. Armaduras não são somadas nesses casos.
* Posição vertical provisória: envelope horizontal de 20 mm. Demais hipóteses e limites do relatório permanecem.
Rxxx corresponde ao mesmo código do relatório. Pxx marca chamada cuja faixa não foi fechada; sem polígono inventado.
Regiões pequenas: código no desenho e configuração completa nesta legenda. Campos não calculados: --.
Cópia de trabalho - capacidade nominal de seção; não verifica esforços, ancoragem, emendas, ELS ou aprovação da laje.

R001 | As/m 3,12 | Mrk 0,63*
Base: --
Negativa: Ø6,3 c/10
h=12 | C40 | N2

R002 | As/m 3,12 | Mrk 0,63*
Base: --
Negativa: Ø6,3 c/10
h=12 | C40 | N2

R003 | As/m 3,12 | Mrk 0,77
Base: --
Negativa: Ø6,3 c/10
h=12 | C40 | N2

R004 | As/m 3,12 | Mrk 0,77
Base: --
Negativa: Ø6,3 c/10
h=12 | C40 | N2

R005 | As/m 3,12 | Mrk 0,77
Base: --
Negativa: Ø6,3 c/10
h=12 | C40 | N2

R006 | As/m 3,12 | Mrk 0,77
Base: --
Negativa: Ø6,3 c/10
h=12 | C40 | N2

R007 | As/m 3,12 | Mrk 0,77
Base: --
Negativa: Ø6,3 c/10
h=12 | C40 | N2

R008 | As/m 3,12 | Mrk 0,77
Base: --
Negativa: Ø6,3 c/10
h=12 | C40 | N2

R009 | As/m 3,12 | Mrk 0,77
Base: --
Negativa: Ø6,3 c/10
h=12 | C40 | N2

R010 | As/m 3,12 | Mrk 0,77
Base: --
Negativa: Ø6,3 c/10
h=12 | C40 | N2

R011 | As/m 3,59 | Mrk 1,62*
Base: --
Negativa: Ø8 c/14
h=20 | C40 | N1

R012 | As/m 3,59 | Mrk 1,62*
Base: --
Negativa: Ø8 c/14
h=20 | C40 | N1

R013 | As/m 3,59 | Mrk 1,62*
Base: --
Negativa: Ø8 c/14
h=20 | C40 | N1

R014 | As/m 6,54 | Mrk 2,88*
Base: --
Negativa: Ø10 c/12
h=20 | C40 | N3

R015 | As/m 6,54 | Mrk 2,88*
Base: --
Negativa: Ø10 c/12
h=20 | C40 | N3

R016 | As/m 3,59 | Mrk 1,70
Base: --
Negativa: Ø8 c/14
h=20 | C35 | N1

R017 | As/m 3,59 | Mrk 1,75
Base: --
Negativa: Ø8 c/14
h=20 | C35 | N1

R018 | As/m 3,59 | Mrk 1,73
Base: --
Negativa: Ø8 c/14
h=20 | C35 | N1

R019 | As/m 6,54 | Mrk 5,15
Base: --
Negativa: Ø10 c/12
h=30 | C35 | N3

R020 | As/m 6,54 | Mrk 5,15
Base: --
Negativa: Ø10 c/12
h=30 | C35 | N3

R021 | As/m 6,54 | Mrk 2,95
Base: --
Negativa: Ø10 c/12
h=20 | C35 | N3

R022 | As/m 6,54 | Mrk 5,02
Base: --
Negativa: Ø10 c/12
h=30 | C35 | N3

R023 | As/m 6,54 | Mrk 5,02
Base: --
Negativa: Ø10 c/12
h=30 | C35 | N3

R024 | As/m -- | Mrk --
Base: --
Negativa: Ø10 c/12 ; Ø10 c/12
Soma pendente | N10,N3

R025 | As/m -- | Mrk --
Base: --
Negativa: Ø10 c/12 ; Ø10 c/12
Soma pendente | N13,N3

R026 | As/m -- | Mrk --
Base: --
Negativa: Ø10 c/12 ; Ø10 c/12
Soma pendente | N10,N3

R027 | As/m -- | Mrk --
Base: --
Negativa: Ø10 c/12 ; Ø10 c/12
Soma pendente | N17,N3

R028 | As/m 4,57 | Mrk 2,10
Base: --
Negativa: Ø8 c/11
h=20 | C35 | N24

R029 | As/m 6,54 | Mrk 2,95
Base: --
Negativa: Ø10 c/12
h=20 | C35 | N10,N3

R030 | As/m 8,77 | Mrk 3,95
Base: --
Negativa: Ø12,5 c/14
h=20 | C35 | N5

R031 | As/m 3,59 | Mrk 1,70
Base: --
Negativa: Ø8 c/14
h=20 | C35 | N29

R032 | As/m 10,23 | Mrk 4,45
Base: --
Negativa: Ø12,5 c/12
h=20 | C35 | N27

R033 | As/m 6,54 | Mrk 2,95
Base: --
Negativa: Ø10 c/12
h=20 | C35 | N8

R034 | As/m 12,27 | Mrk 5,25
Base: --
Negativa: Ø12,5 c/10
h=20 | C35 | N20

R035 | As/m 7,67 | Mrk 3,48
Base: --
Negativa: Ø12,5 c/16
h=20 | C35 | N15

R036 | As/m -- | Mrk --
Base: --
Negativa: Ø10 c/12 ; Ø10 c/12
Soma pendente | N17,N3

R037 | As/m -- | Mrk --
Base: --
Negativa: Ø10 c/12 ; Ø10 c/12
Soma pendente | N10,N3

R038 | As/m -- | Mrk --
Base: --
Negativa: Ø10 c/12 ; Ø10 c/12
Soma pendente | N13,N3

R039 | As/m 6,54 | Mrk 2,87*
Base: --
Negativa: Ø10 c/12
h=20 | C35 | N3

R040 | As/m -- | Mrk --
Base: --
Negativa: Ø10 c/12 ; Ø10 c/12
Soma pendente | N10,N3

R041 | As/m 6,54 | Mrk 3,02
Base: --
Negativa: Ø10 c/12
h=20 | C35 | N17

R042 | As/m 6,54 | Mrk 2,95
Base: --
Negativa: Ø10 c/12
h=20 | C35 | N10,N3

R043 | As/m 6,54 | Mrk 3,02
Base: --
Negativa: Ø10 c/12
h=20 | C35 | N13

R044 | As/m -- | Mrk --
Base: --
Negativa: Ø12,5 c/14 ; Ø12,5 c/13
Soma pendente | N5,N6

R045 | As/m -- | Mrk --
Base: --
Negativa: Ø10 c/12 ; Ø12,5 c/15
Soma pendente | N16,N17

R046 | As/m -- | Mrk --
Base: --
Negativa: Ø10 c/12 ; Ø12,5 c/13
Soma pendente | N10,N11

R047 | As/m -- | Mrk --
Base: --
Negativa: Ø10 c/12 ; Ø12,5 c/15
Soma pendente | N10,N16

R048 | As/m -- | Mrk --
Base: --
Negativa: Ø10 c/12 ; Ø12,5 c/13
Soma pendente | N6,N8

R049 | As/m -- | Mrk --
Base: --
Negativa: Ø12,5 c/12 ; Ø12,5 c/10
Soma pendente | N27,N28

R050 | As/m -- | Mrk --
Base: --
Negativa: Ø10 c/12 ; Ø12,5 c/13
Soma pendente | N11,N13

R051 | As/m 8,18 | Mrk 3,70
Base: --
Negativa: Ø12,5 c/15
h=20 | C35 | N16

R052 | As/m 12,27 | Mrk 5,25
Base: --
Negativa: Ø12,5 c/10
h=20 | C35 | N28

R053 | As/m 9,44 | Mrk 4,23
Base: --
Negativa: Ø12,5 c/13
h=20 | C35 | N11

R054 | As/m 9,44 | Mrk 4,23
Base: --
Negativa: Ø12,5 c/13
h=20 | C35 | N6

R055 | As/m -- | Mrk --
Base: --
Negativa: Ø12,5 c/13 ; Ø12,5 c/11
Soma pendente | N11,N14

R056 | As/m -- | Mrk --
Base: --
Negativa: Ø12,5 c/15 ; Ø12,5 c/11
Soma pendente | N14,N16

R057 | As/m -- | Mrk --
Base: --
Negativa: Ø12,5 c/13 ; Ø12,5 c/16
Soma pendente | N11,N9

R058 | As/m -- | Mrk --
Base: --
Negativa: Ø12,5 c/15 ; Ø12,5 c/11
Soma pendente | N16,N19

R059 | As/m -- | Mrk --
Base: --
Negativa: Ø12,5 c/13 ; Ø12,5 c/16
Soma pendente | N6,N9

R060 | As/m 11,16 | Mrk 4,94
Base: --
Negativa: Ø12,5 c/11
h=20 | C35 | N14

R061 | As/m 7,67 | Mrk 3,48
Base: --
Negativa: Ø12,5 c/16
h=20 | C35 | N9

R062 | As/m 11,16 | Mrk 4,94
Base: --
Negativa: Ø12,5 c/11
h=20 | C35 | N19

R063 | As/m 5,61 | Mrk 2,61
Base: --
Negativa: Ø10 c/14
h=20 | C35 | N23

R064 | As/m 5,61 | Mrk 2,62
Base: --
Negativa: Ø10 c/14
h=20 | C40 | N23

R065 | As/m 11,16 | Mrk 4,99
Base: --
Negativa: Ø12,5 c/11
h=20 | C40 | N14

R066 | As/m 7,67 | Mrk 3,51
Base: --
Negativa: Ø12,5 c/16
h=20 | C40 | N9

R067 | As/m 11,16 | Mrk 4,99
Base: --
Negativa: Ø12,5 c/11
h=20 | C40 | N19

R068 | As/m -- | Mrk --
Base: --
Negativa: Ø10 c/14 ; Ø10 c/11
Soma pendente | N22,N23

R069 | As/m -- | Mrk --
Base: --
Negativa: Ø10 c/14 ; Ø12,5 c/15
Soma pendente | N23,N25

R070 | As/m -- | Mrk --
Base: --
Negativa: Ø12,5 c/11 ; Ø12,5 c/15
Soma pendente | N14,N18

R071 | As/m -- | Mrk --
Base: --
Negativa: Ø12,5 c/11 ; Ø12,5 c/15
Soma pendente | N18,N19

R072 | As/m -- | Mrk --
Base: --
Negativa: Ø12,5 c/11 ; Ø10 c/12
Soma pendente | N12,N14

R073 | As/m -- | Mrk --
Base: --
Negativa: Ø12,5 c/16 ; Ø10 c/12
Soma pendente | N12,N9

R074 | As/m -- | Mrk --
Base: --
Negativa: Ø12,5 c/16 ; Ø10 c/11
Soma pendente | N7,N9

R075 | As/m -- | Mrk --
Base: --
Negativa: Ø12,5 c/11 ; Ø10 c/11
Soma pendente | N19,N22

R076 | As/m 7,14 | Mrk 3,30
Base: --
Negativa: Ø10 c/11
h=20 | C40 | N22

R077 | As/m 8,18 | Mrk 3,73
Base: --
Negativa: Ø12,5 c/15
h=20 | C40 | N25

R078 | As/m 7,14 | Mrk 3,30
Base: --
Negativa: Ø10 c/11
h=20 | C40 | N22

R079 | As/m 8,18 | Mrk 3,73
Base: --
Negativa: Ø12,5 c/15
h=20 | C40 | N18

R080 | As/m 6,54 | Mrk 3,04
Base: --
Negativa: Ø10 c/12
h=20 | C40 | N12

R081 | As/m 7,14 | Mrk 3,30
Base: --
Negativa: Ø10 c/11
h=20 | C40 | N7

R082 | As/m -- | Mrk --
Base: --
Negativa: Ø10 c/12 ; Ø12,5 c/10
Soma pendente | N12,N35

R083 | As/m -- | Mrk --
Base: --
Negativa: Ø10 c/11 ; Ø12,5 c/10
Soma pendente | N22,N47

R084 | As/m -- | Mrk --
Base: --
Negativa: Ø10 c/12 ; Ø12,5 c/13
Soma pendente | N12,N35

R085 | As/m -- | Mrk --
Base: --
Negativa: Ø10 c/11 ; Ø10 c/15
Soma pendente | N22,N52

R086 | As/m -- | Mrk --
Base: --
Negativa: Ø12,5 c/15 ; Ø10 c/15
Soma pendente | N25,N52

R087 | As/m -- | Mrk --
Base: --
Negativa: Ø12,5 c/15 ; Ø12,5 c/10
Soma pendente | N25,N58

R088 | As/m -- | Mrk --
Base: --
Negativa: Ø12,5 c/15 ; Ø12,5 c/10
Soma pendente | N18,N35

R089 | As/m -- | Mrk --
Base: --
Negativa: Ø10 c/11 ; Ø12,5 c/10
Soma pendente | N22,N58

R090 | As/m -- | Mrk --
Base: --
Negativa: Ø12,5 c/15 ; Ø12,5 c/10
Soma pendente | N18,N47

R091 | As/m -- | Mrk --
Base: --
Negativa: Ø10 c/11 ; Ø10 c/15
Soma pendente | N22,N62

R092 | As/m -- | Mrk --
Base: --
Negativa: Ø10 c/11 ; Ø10 c/10
Soma pendente | N31,N7

R093 | As/m -- | Mrk --
Base: --
Negativa: Ø10 c/11 ; Ø12,5 c/13
Soma pendente | N35,N7

R094 | As/m 7,85 | Mrk 3,68
Base: --
Negativa: Ø10 c/10
h=20 | C40 | N31

R095 | As/m 5,24 | Mrk 2,45
Base: --
Negativa: Ø10 c/15
h=20 | C40 | N62

R096 | As/m 5,24 | Mrk 2,45
Base: --
Negativa: Ø10 c/15
h=20 | C40 | N52

R097 | As/m 12,27 | Mrk 5,55
Base: --
Negativa: Ø12,5 c/10
h=20 | C40 | N58

R098 | As/m 9,44 | Mrk 4,27
Base: --
Negativa: Ø12,5 c/13
h=20 | C40 | N35

R099 | As/m 12,27 | Mrk 5,45
Base: --
Negativa: Ø12,5 c/10
h=20 | C40 | N35,N39,N47

R100 | As/m -- | Mrk --
Base: --
Negativa: Ø10 c/15 ; Ø12,5 c/10
Soma pendente | N61,N62

R101 | As/m -- | Mrk --
Base: --
Negativa: Ø12,5 c/10 ; Ø12,5 c/10
Soma pendente | N58,N61

R102 | As/m -- | Mrk --
Base: --
Negativa: Ø10 c/10 ; Ø12,5 c/15
Soma pendente | N31,N33

R103 | As/m -- | Mrk --
Base: --
Negativa: Ø12,5 c/13 ; Ø12,5 c/15
Soma pendente | N33,N35

R104 | As/m -- | Mrk --
Base: --
Negativa: Ø12,5 c/15 ; Ø12,5 c/10
Soma pendente | N35,N39

R105 | As/m -- | Mrk --
Base: --
Negativa: Ø12,5 c/13 ; Ø12,5 c/15
Soma pendente | N35,N39

R106 | As/m -- | Mrk --
Base: --
Negativa: Ø12,5 c/10 ; Ø12,5 c/10
Soma pendente | N35,N39

R107 | As/m -- | Mrk --
Base: --
Negativa: Ø12,5 c/10 ; Ø12,5 c/10
Soma pendente | N39,N47

R108 | As/m -- | Mrk --
Base: --
Negativa: Ø12,5 c/15 ; Ø12,5 c/10
Soma pendente | N39,N47

R109 | As/m -- | Mrk --
Base: --
Negativa: Ø10 c/15 ; Ø12,5 c/15
Soma pendente | N39,N52

R110 | As/m -- | Mrk --
Base: --
Negativa: Ø12,5 c/15 ; Ø12,5 c/10
Soma pendente | N39,N58

R111 | As/m -- | Mrk --
Base: --
Negativa: Ø10 c/15 ; Ø12,5 c/15
Soma pendente | N39,N52

R112 | As/m 12,27 | Mrk 5,45
Base: --
Negativa: Ø12,5 c/10
h=20 | C40 | N61

R113 | As/m 8,18 | Mrk 3,73
Base: --
Negativa: Ø12,5 c/15
h=20 | C40 | N39

R114 | As/m 8,18 | Mrk 3,73
Base: --
Negativa: Ø12,5 c/15
h=20 | C40 | N39

R115 | As/m 8,18 | Mrk 3,73
Base: --
Negativa: Ø12,5 c/15
h=20 | C40 | N39

R116 | As/m 8,18 | Mrk 3,73
Base: --
Negativa: Ø12,5 c/15
h=20 | C40 | N33

R117 | As/m -- | Mrk --
Base: --
Negativa: Ø12,5 c/10 ; Ø12,5 c/13
Soma pendente | N39,N45

R118 | As/m -- | Mrk --
Base: --
Negativa: Ø12,5 c/10 ; Ø12,5 c/12
Soma pendente | N39,N42

R119 | As/m -- | Mrk --
Base: --
Negativa: Ø12,5 c/15 ; Ø12,5 c/14
Soma pendente | N36,N39

R120 | As/m -- | Mrk --
Base: --
Negativa: Ø12,5 c/15 ; Ø12,5 c/10
Soma pendente | N39,N50

R121 | As/m -- | Mrk --
Base: --
Negativa: Ø12,5 c/15 ; Ø12,5 c/12
Soma pendente | N33,N34

R122 | As/m -- | Mrk --
Base: --
Negativa: Ø12,5 c/10 ; Ø10 c/12
Soma pendente | N59,N61

R123 | As/m 8,77 | Mrk 3,98
Base: --
Negativa: Ø12,5 c/14
h=20 | C40 | N36

R124 | As/m 11,16 | Mrk 4,99
Base: --
Negativa: Ø12,5 c/11
h=20 | C40 | N51

R125 | As/m 6,54 | Mrk 3,04
Base: --
Negativa: Ø10 c/12
h=20 | C40 | N63

R126 | As/m 20,11 | Mrk 7,90*
Base: --
Negativa: Ø16 c/10
h=20 | C40 | N43

R127 | As/m 3,59 | Mrk 1,67
Base: --
Negativa: Ø8 c/14
h=20 | C40 | N30

R128 | As/m 9,44 | Mrk 4,27
Base: --
Negativa: Ø12,5 c/13
h=20 | C40 | N45,N46

R129 | As/m 9,44 | Mrk 4,27
Base: --
Negativa: Ø12,5 c/13
h=20 | C40 | N54

R130 | As/m 9,44 | Mrk 4,27
Base: --
Negativa: Ø12,5 c/13
h=20 | C40 | N48

R131 | As/m 10,23 | Mrk 4,60
Base: --
Negativa: Ø12,5 c/12
h=20 | C40 | N34

R132 | As/m 12,27 | Mrk 5,32
Base: --
Negativa: Ø12,5 c/10
h=20 | C40 | N49,N50

R133 | As/m 3,35 | Mrk 1,64
Base: --
Negativa: Ø8 c/15
h=20 | C40 | N40

R134 | As/m 3,35 | Mrk 1,56
Base: --
Negativa: Ø8 c/15
h=20 | C40 | N40

R135 | As/m 6,54 | Mrk 2,97
Base: --
Negativa: Ø10 c/12
h=20 | C40 | N59

R136 | As/m 8,77 | Mrk 3,88
Base: --
Negativa: Ø12,5 c/14
h=20 | C40 | N56

R137 | As/m 5,61 | Mrk 2,62
Base: --
Negativa: Ø10 c/14
h=20 | C40 | N38

R138 | As/m 3,35 | Mrk 1,56
Base: --
Negativa: Ø8 c/15
h=20 | C40 | N40

R139 | As/m 3,35 | Mrk 1,64
Base: --
Negativa: Ø8 c/15
h=20 | C40 | N40

R140 | As/m 7,85 | Mrk 3,62
Base: --
Negativa: Ø10 c/10
h=20 | C40 | N32

R141 | As/m 10,23 | Mrk 4,60
Base: --
Negativa: Ø12,5 c/12
h=20 | C40 | N42,N44

R142 | As/m -- | Mrk --
Base: --
Negativa: Ø12,5 c/12 ; Ø10 c/10
Soma pendente | N32,N34

R143 | As/m 3,35 | Mrk 1,52*
Base: --
Negativa: Ø8 c/15
h=20 | C40 | N40

R144 | As/m -- | Mrk --
Base: --
Negativa: Ø8 c/15 ; Ø8 c/18
Soma pendente | N40,N41

R145 | As/m -- | Mrk --
Base: --
Negativa: Ø8 c/15 ; Ø8 c/18
Soma pendente | N40,N41

R146 | As/m 2,79 | Mrk 1,38
Base: --
Negativa: Ø8 c/18
h=20 | C40 | N41

R147 | As/m 8,18 | Mrk 3,73
Base: --
Negativa: Ø12,5 c/15
h=20 | C40 | N60

R148 | As/m 11,16 | Mrk 4,99
Base: --
Negativa: Ø12,5 c/11
h=20 | C40 | N53,N55

R149 | As/m 2,79 | Mrk 0,93
Base: --
Negativa: Ø8 c/18
h=15 | C40 | N41

R150 | As/m 2,79 | Mrk 0,93
Base: --
Negativa: Ø8 c/18
h=15 | C40 | N41

R151 | As/m 3,59 | Mrk 1,71
Base: --
Negativa: Ø8 c/14
h=20 | C40 | N37

R152 | As/m 2,79 | Mrk 1,38
Base: --
Negativa: Ø8 c/18
h=20 | C40 | N41

R153 | As/m 2,79 | Mrk 1,38
Base: --
Negativa: Ø8 c/18
h=20 | C40 | N41

R154 | As/m -- | Mrk --
Base: --
Negativa: Ø8 c/18 ; Ø8 c/12
Soma pendente | N41,N73

R155 | As/m -- | Mrk --
Base: --
Negativa: Ø12,5 c/11 ; Ø10 c/10
Soma pendente | N32,N64

R156 | As/m 4,19 | Mrk 1,99
Base: --
Negativa: Ø8 c/12
h=20 | C40 | N73

R157 | As/m -- | Mrk --
Base: --
Negativa: Ø12,5 c/15 ; Ø10 c/12
Soma pendente | N60,N89

R158 | As/m -- | Mrk --
Base: --
Negativa: Ø10 c/12 ; Ø16 c/13
Soma pendente | N59,N85

R159 | As/m -- | Mrk --
Base: --
Negativa: Ø12,5 c/15 ; Ø16 c/13
Soma pendente | N60,N85

R160 | As/m -- | Mrk --
Base: --
Negativa: Ø10 c/14 ; Ø10 c/15
Soma pendente | N38,N68

R161 | As/m 3,59 | Mrk 1,71
Base: --
Negativa: Ø8 c/14
h=20 | C40 | N70

R162 | As/m 11,16 | Mrk 4,99
Base: --
Negativa: Ø12,5 c/11
h=20 | C40 | N64

R163 | As/m 12,27 | Mrk 5,45
Base: --
Negativa: Ø12,5 c/10
h=20 | C40 | N82

R164 | As/m 6,54 | Mrk 2,97
Base: --
Negativa: Ø10 c/12
h=20 | C40 | N89

R165 | As/m 5,24 | Mrk 2,39
Base: --
Negativa: Ø10 c/15
h=20 | C40 | N84

R166 | As/m 15,34 | Mrk 6,68
Base: --
Negativa: Ø12,5 c/8
h=20 | C40 | N74

R167 | As/m 5,24 | Mrk 2,45
Base: --
Negativa: Ø10 c/15
h=20 | C40 | N80

R168 | As/m 5,24 | Mrk 2,45
Base: --
Negativa: Ø10 c/15
h=20 | C40 | N81

R169 | As/m 6,54 | Mrk 3,04
Base: --
Negativa: Ø10 c/12
h=20 | C40 | N77

R170 | As/m -- | Mrk --
Base: --
Negativa: Ø16 c/13 ; Ø16 c/13
Soma pendente | N85,N87

R171 | As/m -- | Mrk --
Base: --
Negativa: Ø12,5 c/10 ; Ø16 c/13
Soma pendente | N66,N85

R172 | As/m 5,24 | Mrk 2,45
Base: --
Negativa: Ø10 c/15
h=20 | C40 | N69

R173 | As/m -- | Mrk --
Base: --
Negativa: Ø10 c/12 ; Ø16 c/13
Soma pendente | N87,N89

R174 | As/m 15,47 | Mrk 6,47
Base: --
Negativa: Ø16 c/13
h=20 | C40 | N85,N87

R175 | As/m -- | Mrk --
Base: --
Negativa: Ø12,5 c/11 ; Ø12,5 c/12
Soma pendente | N64,N66

R176 | As/m -- | Mrk --
Base: --
Negativa: Ø12,5 c/10 ; Ø12,5 c/10
Soma pendente | N66,N82

R177 | As/m 5,24 | Mrk 2,45
Base: --
Negativa: Ø10 c/15
h=20 | C40 | N68

R178 | As/m 3,59 | Mrk 1,71
Base: --
Negativa: Ø8 c/14
h=20 | C40 | N71

R179 | As/m 5,24 | Mrk 2,45
Base: --
Negativa: Ø10 c/15
h=20 | C40 | N76

R180 | As/m 12,27 | Mrk 5,32
Base: --
Negativa: Ø12,5 c/10
h=20 | C40 | N66

R181 | As/m 10,23 | Mrk 4,60
Base: --
Negativa: Ø12,5 c/12
h=20 | C40 | N66

R182 | As/m -- | Mrk --
Base: --
Negativa: Ø10 c/14 ; Ø10 c/15
Soma pendente | N78,N80

R183 | As/m -- | Mrk --
Base: --
Negativa: Ø10 c/12 ; Ø10 c/14
Soma pendente | N77,N78

R184 | As/m -- | Mrk --
Base: --
Negativa: Ø12,5 c/12 ; Ø12,5 c/15
Soma pendente | N35,N66

R185 | As/m -- | Mrk --
Base: --
Negativa: Ø10 c/15 ; Ø10 c/15
Soma pendente | N81,N83

R186 | As/m -- | Mrk --
Base: --
Negativa: Ø10 c/15 ; Ø12,5 c/10
Soma pendente | N66,N83

R187 | As/m -- | Mrk --
Base: --
Negativa: Ø16 c/13 ; Ø12,5 c/10
Soma pendente | N66,N86

R188 | As/m -- | Mrk --
Base: --
Negativa: Ø12,5 c/12 ; Ø10 c/15
Soma pendente | N65,N66

R189 | As/m -- | Mrk --
Base: --
Negativa: Ø16 c/13 ; Ø16 c/13
Soma pendente | N86,N87

R190 | As/m -- | Mrk --
Base: --
Negativa: Ø10 c/15 ; Ø12,5 c/10
Soma pendente | N69,N72

R191 | As/m 8,18 | Mrk 3,73
Base: --
Negativa: Ø12,5 c/15
h=20 | C40 | N35

R192 | As/m 5,61 | Mrk 2,62
Base: --
Negativa: Ø10 c/14
h=20 | C40 | N78

R193 | As/m 5,24 | Mrk 2,49
Base: --
Negativa: Ø10 c/15
h=20 | C40 | N83

R194 | As/m 15,47 | Mrk 6,64
Base: --
Negativa: Ø16 c/13
h=20 | C40 | N86

R195 | As/m 5,24 | Mrk 2,49
Base: --
Negativa: Ø10 c/15
h=20 | C40 | N65

R196 | As/m 5,24 | Mrk 2,39
Base: --
Negativa: Ø10 c/15
h=20 | C40 | N88

R197 | As/m 12,27 | Mrk 5,45
Base: --
Negativa: Ø12,5 c/10
h=20 | C40 | N72,N75

R198 | As/m -- | Mrk --
Base: --
Negativa: Ø12,5 c/10 ; Ø12,5 c/10
Soma pendente | N72,N75

R199 | As/m 12,27 | Mrk 5,39
Base: --
Negativa: Ø12,5 c/10
h=20 | C35 | N72

R200 | As/m 12,27 | Mrk 5,39
Base: --
Negativa: Ø12,5 c/10
h=20 | C35 | N75

R201 | As/m 5,24 | Mrk 2,44
Base: --
Negativa: Ø10 c/15
h=20 | C35 | N76

R202 | As/m 5,24 | Mrk 2,48
Base: --
Negativa: Ø10 c/15
h=20 | C35 | N65

R203 | As/m -- | Mrk --
Base: --
Negativa: Ø12,5 c/10 ; Ø12,5 c/10
Soma pendente | N72,N75

R204 | As/m 5,24 | Mrk 2,48
Base: --
Negativa: Ø10 c/15
h=20 | C35 | N83

R205 | As/m 15,47 | Mrk 6,55
Base: --
Negativa: Ø16 c/13
h=20 | C35 | N86

R206 | As/m 5,61 | Mrk 2,61
Base: --
Negativa: Ø10 c/14
h=20 | C35 | N78

R207 | As/m 5,24 | Mrk 2,44
Base: --
Negativa: Ø10 c/15
h=20 | C35 | N88

R208 | As/m 8,18 | Mrk 3,77
Base: --
Negativa: Ø12,5 c/15
h=20 | C35 | N35

P01 | As/m -- | Mrk --
Base: --
Armadura: Ø8 c/18
Faixa pendente | 7304-O002 | N41

P02 | As/m -- | Mrk --
Base: --
Armadura: Ø8 c/18
Faixa pendente | 7304-O007 | N41

P03 | As/m -- | Mrk --
Base: --
Armadura: Ø12,5 c/12
Faixa pendente | 7304-O085 | N79

19/10/2026 | ATP S07 | mesmas regiões e resultados do relatório preliminar | Concretopy