PAVIMENTO TÉRREO PARTE 1 DA LAJE, ARMADURA POSITIVA VERTICAL , VER PLANTA 7-302

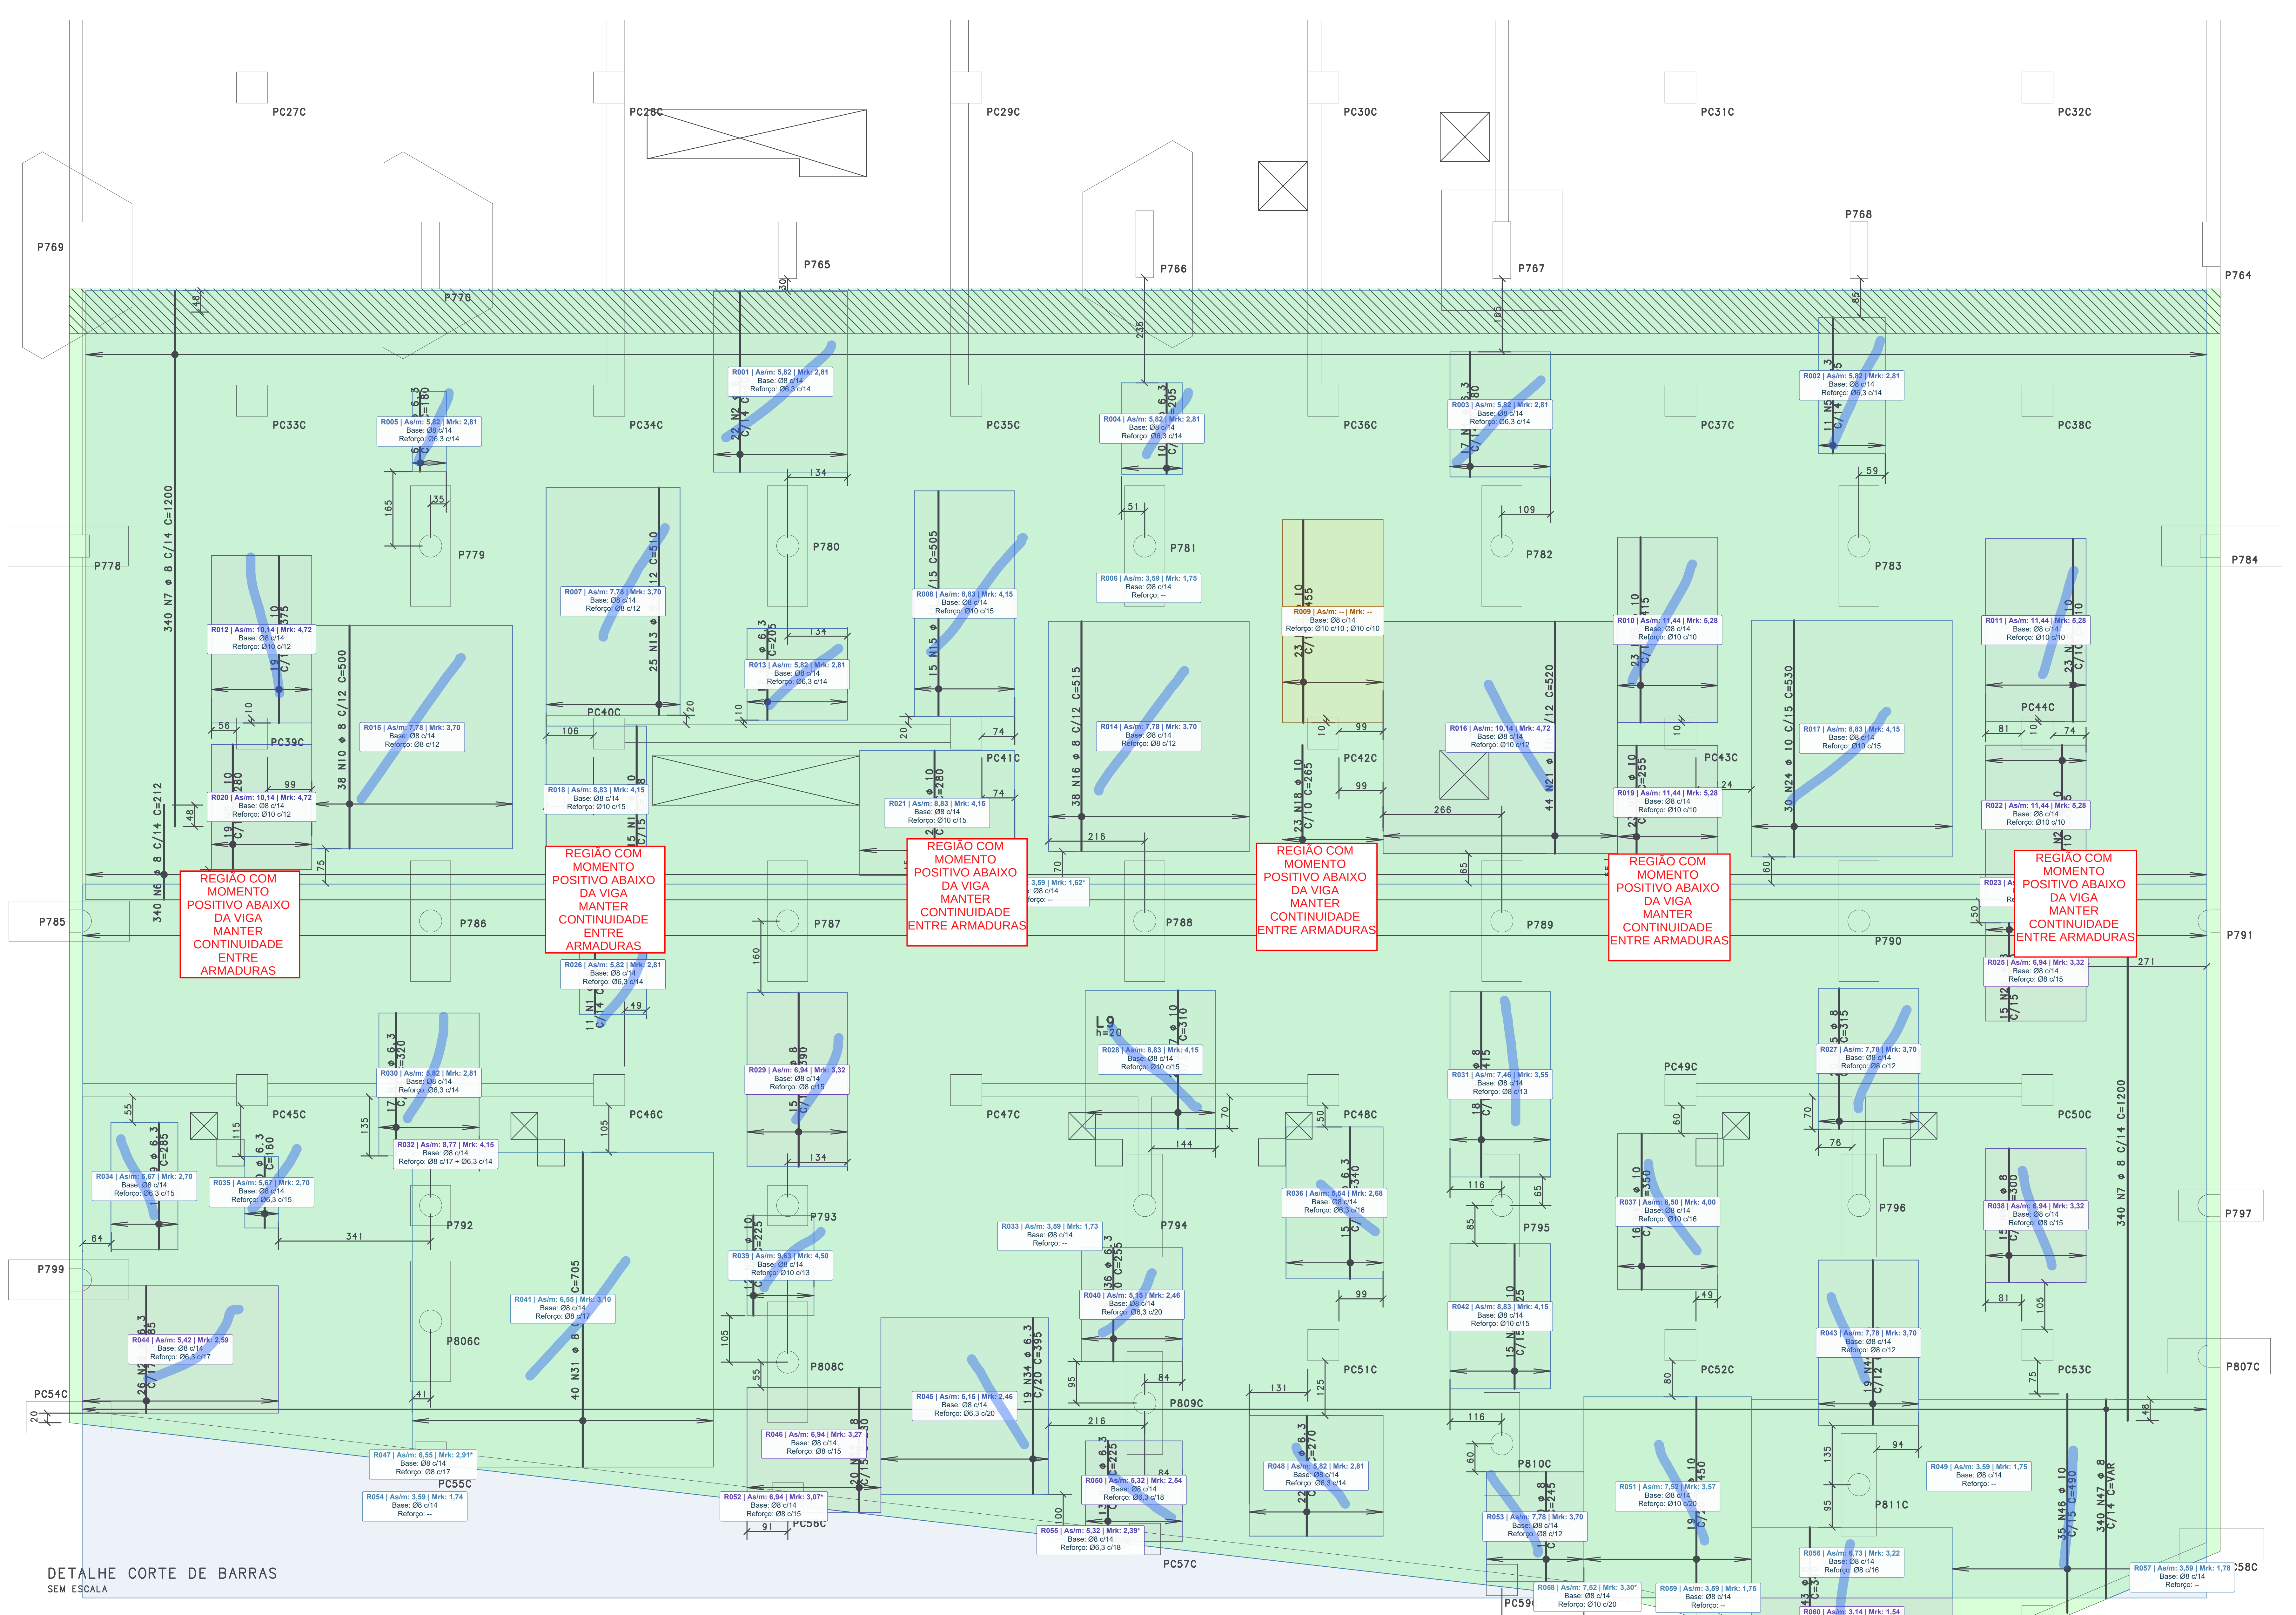

DETALHE CORTE DE BARRAS
SEM ESCALA

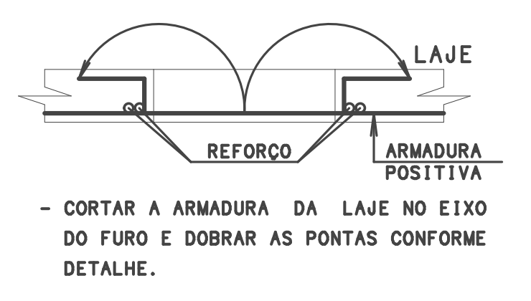

- CORTAR A ARMADURA DA LAJE NO EIXO DO FURO E DOBRAR AS PONTAS CONFORME DETALHE.

	AÇO	POS	QUANT	BIT (mm)	COMPRIMENTO UNIT (cm)	COMPRIMENTO TOTAL (cm)
	50A	1	17	6.3	180	3060
	50A	2	22	6.3	405	8910
	50A	3	27	6.3	205	5535
	50A	4	17	6.3	280	4760
	50A	5	11	6.3	305	3355
	50A	6	340	8	212	72080
	50A	7	680	8	1200	816000
	50A	8	43	10	280	12040
	50A	9	19	10	375	7125
	50A	10	38	8	500	19000
	50A	11	17	6.3	320	5440
	50A	12	15	10	328	4920
	50A	13	25	8	510	12750
	50A	14	15	8	390	5850
	50A	15	15	10	505	7575
	50A	16	38	8	515	19570
	50A	17	20	10	310	6200
	50A	18	23	10	265	6095
	50A	19	23	10	455	10465
	50A	20	18	8	415	7470
	50A	21	44	10	520	22880
	50A	22	23	10	255	5865
	50A	23	23	10	415	9545
	50A	24	30	10	530	15900
	50A	25	20	8	315	6300
	50A	26	15	8	220	3300
	50A	27	23	10	345	7935
	50A	28	23	10	410	9430
	50A	29	36	6.3	285	10260
	50A	30	5	6.3	160	800
	50A	31	40	8	705	28200
	50A	32	12	10	225	2700
	50A	33	20	8	280	5600
	50A	34	19	6.3	395	7505
	50A	35	13	6.3	225	2925
	50A	36	12	6.3	255	3060
	50A	37	22	6.3	270	5940
	50A	38	15	6.3	340	5100
	50A	39	15	10	325	4875
	50A	40	19	8	245	4655
	50A	41	16	10	350	5600
	50A	42	19	10	450	8550
	50A	43	29	8	340	9860
	50A	44	19	8	370	7030
	50A	45	15	8	300	4500
	50A	46	35	10	490	17150
	50A	47	340	8	--VAR--	111180

RESUMO TOTAL AÇO CA 50-60			
AÇO	BIT (mm)	COMPR (m)	PESO (kg)
50A	6.3	667	163
50A	8	11333	4477
50A	10	1649	1017
Peso Total		50A =	5657 kgf

LEGENDA

🟩 REGIÃO COM fck 35 MPa

⬜ REGIÃO COM fck 40 MPa

REV.	DATA	ALTERAÇÃO	VISTO
00	17/07/26	EMISSÃO INICIAL	MVJ

PROCALK
ESTRUTURAS

RESP. TÉCNICOS
Eng. Edemir C. Simonato
CREA-RS 63038
Eng. Carlos R.M. Morais
CREA-RS 74695

Rua João Abbott, 473/401
Porto Alegre - CEP 90460-150
F. (51)3013.3200
procalk@procalk.com.br
www.procalk.com.br

Obra
WERT PORTO BELO RESIDENCES
PORTO BELO - SC

Assunto
LAJES - MULTI 02 - SETOR 7
PAVIMENTO TÉRREO - PARTE 2

Conteúdo
ARMADURA POSITIVA VERTICAL

Cliente: WERT
Número: 24-1454
Desenho: 7-306/0
Identificação: WPBR-EST-EX-7306-PLN-MU2-S07-TE-R00
Desenho: MARCUS
Escala: 1:75
fck: 40/35 MPa
Data: 17/07/2026

Direitos Autorais Reservados Lei N 5194/66

100/59.4

PARA PLOTAGEM UTILIZAR EXCLUSIVAMENTE O ARQUIVO PLT OU PDF.

PROCALK ESTRUTURAS PL ARP73000006.PLT 17/07/2026 14:37:10

ATP S07 | 7306 | REGIÕES E ARMADURAS

As/m em cm²/m | Mrk em tf·m/m = |MRd|/1,4 (resistência equivalente, não resistência característica).
h e d em cm; concreto C35/C40 conforme a região do relatório anterior. Valores resistentes em módulo.
Base, reforço e regiões reapresentados sem novo cálculo. Negativas sem base contínua: Base --.
Base -- também indica base não individualizada no relatório; não significa ausência física de armadura.
Pendências / sobreposições com soma não verificada: As/m -- e Mrk --. Armaduras não são somadas nesses casos.
* Posição vertical provisória: envelope horizontal de 20 mm. Demais hipóteses e limites do relatório permanecem.
Rxxx corresponde ao mesmo código do relatório. Pxx marca chamada cuja faixa não foi fechada; sem polígono inventado.
Regiões pequenas: código no desenho e configuração completa nesta legenda. Campos não calculados: --.
Cópia de trabalho - capacidade nominal de seção; não verifica esforços, ancoragem, emendas, ELS ou aprovação da laje.

R001 | As/m 5,82 | Mrk 2,81
Base: Ø8 c/14
Reforço: Ø6,3 c/14
h=20 | C35 | N2,N7

R002 | As/m 5,82 | Mrk 2,81
Base: Ø8 c/14
Reforço: Ø6,3 c/14
h=20 | C35 | N5,N7

R003 | As/m 5,82 | Mrk 2,81
Base: Ø8 c/14
Reforço: Ø6,3 c/14
h=20 | C35 | N4,N7

R004 | As/m 5,82 | Mrk 2,81
Base: Ø8 c/14
Reforço: Ø6,3 c/14
h=20 | C35 | N3,N7

R005 | As/m 5,82 | Mrk 2,81
Base: Ø8 c/14
Reforço: Ø6,3 c/14
h=20 | C35 | N1,N7

R006 | As/m 3,59 | Mrk 1,75
Base: Ø8 c/14
Reforço: --
h=20 | C35 | N6,N7

R007 | As/m 7,78 | Mrk 3,70
Base: Ø8 c/14
Reforço: Ø8 c/12
h=20 | C35 | N13,N7

R008 | As/m 8,83 | Mrk 4,15
Base: Ø8 c/14
Reforço: Ø10 c/15
h=20 | C35 | N15,N7

R009 | As/m -- | Mrk --
Base: Ø8 c/14
Reforço: Ø10 c/10 ; Ø10 c/10
Soma pendente | N18,N19,N7

R010 | As/m 11,44 | Mrk 5,28
Base: Ø8 c/14
Reforço: Ø10 c/10
h=20 | C35 | N23,N7

R011 | As/m 11,44 | Mrk 5,28
Base: Ø8 c/14
Reforço: Ø10 c/10
h=20 | C35 | N28,N7

R012 | As/m 10,14 | Mrk 4,72
Base: Ø8 c/14
Reforço: Ø10 c/12
h=20 | C35 | N7,N9

R013 | As/m 5,82 | Mrk 2,81
Base: Ø8 c/14
Reforço: Ø6,3 c/14
h=20 | C35 | N3,N7

R014 | As/m 7,78 | Mrk 3,70
Base: Ø8 c/14
Reforço: Ø8 c/12
h=20 | C35 | N16,N6,N7

R015 | As/m 7,78 | Mrk 3,70
Base: Ø8 c/14
Reforço: Ø8 c/12
h=20 | C35 | N10,N6,N7

R016 | As/m 10,14 | Mrk 4,72
Base: Ø8 c/14
Reforço: Ø10 c/12
h=20 | C35 | N21,N6,N7

R017 | As/m 8,83 | Mrk 4,15
Base: Ø8 c/14
Reforço: Ø10 c/15
h=20 | C35 | N24,N6,N7

R018 | As/m 8,83 | Mrk 4,15
Base: Ø8 c/14
Reforço: Ø10 c/15
h=20 | C35 | N12,N6,N7

R019 | As/m 11,44 | Mrk 5,28
Base: Ø8 c/14
Reforço: Ø10 c/10
h=20 | C35 | N22,N6,N7

R020 | As/m 10,14 | Mrk 4,72
Base: Ø8 c/14
Reforço: Ø10 c/12
h=20 | C35 | N6,N7,N8

R021 | As/m 8,83 | Mrk 4,15
Base: Ø8 c/14
Reforço: Ø10 c/15
h=20 | C35 | N6,N7,N8

R022 | As/m 11,44 | Mrk 5,28
Base: Ø8 c/14
Reforço: Ø10 c/10
h=20 | C35 | N27,N6,N7

R023 | As/m 11,44 | Mrk 4,84*
Base: Ø8 c/14
Reforço: Ø10 c/10
h=20 | C35 | N27,N6,N7

R024 | As/m 3,59 | Mrk 1,62*
Base: Ø8 c/14
Reforço: --
h=20 | C35 | N6,N7

R025 | As/m 6,94 | Mrk 3,32
Base: Ø8 c/14
Reforço: Ø8 c/15
h=20 | C35 | N26,N7

R026 | As/m 5,82 | Mrk 2,81
Base: Ø8 c/14
Reforço: Ø6,3 c/14
h=20 | C35 | N1,N7

R027 | As/m 7,78 | Mrk 3,70
Base: Ø8 c/14
Reforço: Ø8 c/12
h=20 | C35 | N25,N7

R028 | As/m 8,83 | Mrk 4,15
Base: Ø8 c/14
Reforço: Ø10 c/15
h=20 | C35 | N17,N7

R029 | As/m 6,94 | Mrk 3,32
Base: Ø8 c/14
Reforço: Ø8 c/15
h=20 | C35 | N14,N7

R030 | As/m 5,82 | Mrk 2,81
Base: Ø8 c/14
Reforço: Ø6,3 c/14
h=20 | C35 | N11,N7

R031 | As/m 7,46 | Mrk 3,55
Base: Ø8 c/14
Reforço: Ø8 c/13
h=20 | C35 | N20,N7

R032 | As/m 8,77 | Mrk 4,15
Base: Ø8 c/14
Reforço: Ø8 c/17 + Ø6,3 c/14
h=20 | C35 | N11,N31,N7

R033 | As/m 3,59 | Mrk 1,73
Base: Ø8 c/14
Reforço: --
h=20 | C35 | N47,N7

R034 | As/m 5,67 | Mrk 2,70
Base: Ø8 c/14
Reforço: Ø6,3 c/15
h=20 | C35 | N29,N7

R035 | As/m 5,67 | Mrk 2,70
Base: Ø8 c/14
Reforço: Ø6,3 c/15
h=20 | C35 | N30,N7

R036 | As/m 5,54 | Mrk 2,68
Base: Ø8 c/14
Reforço: Ø6,3 c/16
h=20 | C35 | N38,N7

R037 | As/m 8,50 | Mrk 4,00
Base: Ø8 c/14
Reforço: Ø10 c/16
h=20 | C35 | N41,N7

R038 | As/m 6,94 | Mrk 3,32
Base: Ø8 c/14
Reforço: Ø8 c/15
h=20 | C35 | N45,N7

R039 | As/m 9,63 | Mrk 4,50
Base: Ø8 c/14
Reforço: Ø10 c/13
h=20 | C35 | N32,N7

R040 | As/m 5,15 | Mrk 2,46
Base: Ø8 c/14
Reforço: Ø6,3 c/20
h=20 | C35 | N36,N7

R041 | As/m 6,55 | Mrk 3,10
Base: Ø8 c/14
Reforço: Ø8 c/17
h=20 | C35 | N31,N47,N7

R042 | As/m 8,83 | Mrk 4,15
Base: Ø8 c/14
Reforço: Ø10 c/15
h=20 | C35 | N39,N7

R043 | As/m 7,78 | Mrk 3,70
Base: Ø8 c/14
Reforço: Ø8 c/12
h=20 | C35 | N44,N47,N7

R044 | As/m 5,42 | Mrk 2,59
Base: Ø8 c/14
Reforço: Ø6,3 c/17
h=20 | C35 | N29,N47,N7

R045 | As/m 5,15 | Mrk 2,46
Base: Ø8 c/14
Reforço: Ø6,3 c/20
h=20 | C35 | N34,N47,N7

R046 | As/m 6,94 | Mrk 3,27
Base: Ø8 c/14
Reforço: Ø8 c/15
h=20 | C35 | N33,N47,N7

R047 | As/m 6,55 | Mrk 2,91*
Base: Ø8 c/14
Reforço: Ø8 c/17
h=20 | C40 | N31,N47

R048 | As/m 5,82 | Mrk 2,81
Base: Ø8 c/14
Reforço: Ø6,3 c/14
h=20 | C35 | N37,N47,N7

R049 | As/m 3,59 | Mrk 1,75
Base: Ø8 c/14
Reforço: --
h=20 | C35 | N47,N7

R050 | As/m 5,32 | Mrk 2,54
Base: Ø8 c/14
Reforço: Ø6,3 c/18
h=20 | C35 | N35,N47

R051 | As/m 7,52 | Mrk 3,57
Base: Ø8 c/14
Reforço: Ø10 c/20
h=20 | C35 | N42,N47,N7

R052 | As/m 6,94 | Mrk 3,07*
Base: Ø8 c/14
Reforço: Ø8 c/15
h=20 | C40 | N33,N47

R053 | As/m 7,78 | Mrk 3,70
Base: Ø8 c/14
Reforço: Ø8 c/12
h=20 | C35 | N40,N47

R054 | As/m 3,59 | Mrk 1,74
Base: Ø8 c/14
Reforço: --
h=20 | C40 | N47

R055 | As/m 5,32 | Mrk 2,39*
Base: Ø8 c/14
Reforço: Ø6,3 c/18
h=20 | C40 | N35,N47

R056 | As/m 6,73 | Mrk 3,22
Base: Ø8 c/14
Reforço: Ø8 c/16
h=20 | C35 | N43,N47

R057 | As/m 3,59 | Mrk 1,78
Base: Ø8 c/14
Reforço: --
h=20 | C40 | N47

R058 | As/m 7,52 | Mrk 3,30*
Base: Ø8 c/14
Reforço: Ø10 c/20
h=20 | C40 | N42,N47

R059 | As/m 3,59 | Mrk 1,75
Base: Ø8 c/14
Reforço: --
h=20 | C35 | N47

R060 | As/m 3,14 | Mrk 1,54
Base: --
Arm./ref.: Ø8 c/16
h=20 | C35 | N43

R061 | As/m 3,14 | Mrk 1,54
Base: --
Arm./ref.: Ø8 c/16
h=20 | C40 | N43

R062 | As/m 3,14 | Mrk 1,54
Base: --
Arm./ref.: Ø8 c/16
h=20 | C40 | N43